HỒ SƠ BẢN VẼ KIẾN TRÚC

GIAI ĐOẠN: THIẾT KẾ THI CÔNG

CÔNG TRÌNH: NHÀ PHỐ 5x18m, 3 TẦNG + TUM

CHỦ ĐẦU TƯ: CHỦ ĐẦU TƯ (MẪU)

ĐƠN VỊ THIẾT KẾ: AUTOCAD MCP

ĐỊA ĐIỂM XÂY DỰNG: Mẫu minh họa

NGÀY: 11/2026

GHI CHÚ:NHÀ THẦU THI CÔNG KIỂM TRA KÍCH THƯỚC THỰC TẾ, NẾU THẤY CÓ XUNG ĐỘT CẦN BÁO LẠI CHO THIẾT KẾ VÀ QUẢN LÝ KỸ THUẬT.

LẦN NỘP	NỘI DUNG ĐIỀU CHỈNH	NGÀY NỘP
1		
2		
3		
4		

GHI CHÚ - Note:

CHỦ ĐẦU TƯ - Client:
CHỦ ĐẦU TƯ (MẪU)

DỰ ÁN - Project:
NHÀ PHỐ 5x18m, 3 TẦNG + TUM
Mẫu minh họa

HẠNG MỤC - Item:
KIẾN TRÚC

TƯ VẤN THIẾT KẾ - Consultant:
AUTOCAD MCP

CHỦ NHIỆM TK - Chief of Project	
CHỦ TRÌ TK - Chief of Division	
THIẾT KẾ - Designed by AutoCAD MCP	
KIỂM TRA - Checked by ...	

TÊN BẢN VẼ - Drawing name:
TỜ BÌA

SỐ HĐ - Contract No:	PHIÊN BẢN - Version 01
GIAI ĐOẠN - Phase: TKTC	KÝ HIỆU BẢN VẼ - Drawing No: KT-BIA
TỶ LỆ - Scale: 1:50	HOÀN THÀNH - Finish: 03/11/2026

DANH MỤC BẢN VẼ - KIẾN TRÚC

STT	KÝ HIỆU	TÊN BẢN VẼ	TỶ LỆ	KHỔ GIẤY	GHI CHÚ
1	KT-BIA	TỜ BÌA		A2	
2	KT-00	DANH MỤC BẢN VẼ KIẾN TRÚC	1:50	A2	
3	KT-01	MẶT BẰNG TẦNG 1, TẦNG 2, TẦNG 3	1:100	A2	
4	KT-02	MẶT BẰNG TUM, MẶT BẰNG MÁI	1:100	A2	
5	KT-03	MẶT ĐỨNG CHÍNH, MẶT ĐỨNG SAU, MẶT ĐỨNG BÊN	1:100	A2	
6	KT-04	MẶT CẮT A-A, B-B	1:100	A2	
7	KT-05	CHI TIẾT CẦU THANG	NHƯ HÌNH	A2	
8	KT-06	BẢNG THỐNG KÊ CỬA ĐI, CỬA SỔ	1:50	A2	

GHI CHÚ:NHÀ THẦU THI CÔNG KIỂM TRA KÍCH THƯỚC THỰC TẾ, NẾU THẤY CÓ XUNG ĐỘT CẦN BÁO LẠI CHO THIẾT KẾ VÀ QUẢN LÝ KỸ THUẬT.

LẦN NỘP	NỘI DUNG ĐIỀU CHỈNH	NGÀY NỘP
1		
2		
3		
4		

GHI CHÚ - Note:

CHỦ ĐẦU TƯ - Client:

CHỦ ĐẦU TƯ (MẪU)

DỰ ÁN - Project:

NHÀ PHỐ 5x18m, 3 TẦNG + TUM

Mẫu minh họa

HẠNG MỤC - Item:

KIẾN TRÚC

TƯ VẤN THIẾT KẾ - Consultant:


AUTOCAD MCP

CHỦ NHIỆM TK - Chief of Project	
CHỦ TRÌ TK - Chief of Division	
THIẾT KẾ - Designed by AutoCAD MCP	
KIỂM TRA - Checked by ...	

TÊN BẢN VẼ - Drawing name:


DANH MỤC BẢN VẼ KIẾN TRÚC

SỐ HĐ - Contract No:	PHIÊN BẢN - Version 01
GIAI ĐOẠN - Phase: TKTC	KÝ HIỆU BẢN VẼ - Drawing No KT-00
TỶ LỆ - Scale: 1:50	HOÀN THÀNH - Finish: 03/11/2026

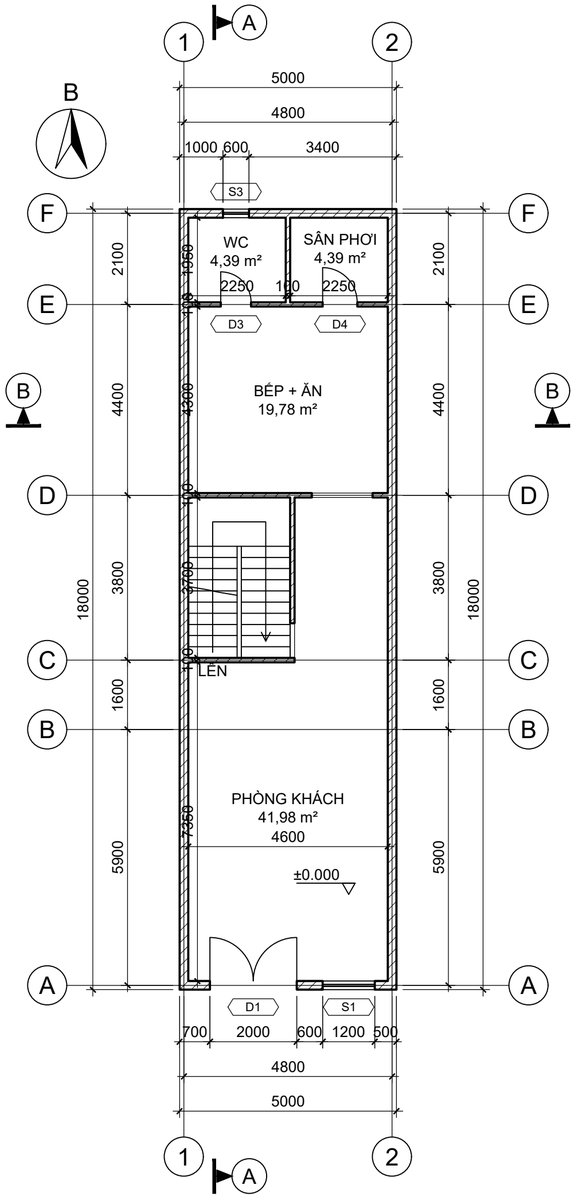


MẶT BẰNG TẦNG 1

TỶ LỆ: 1/100

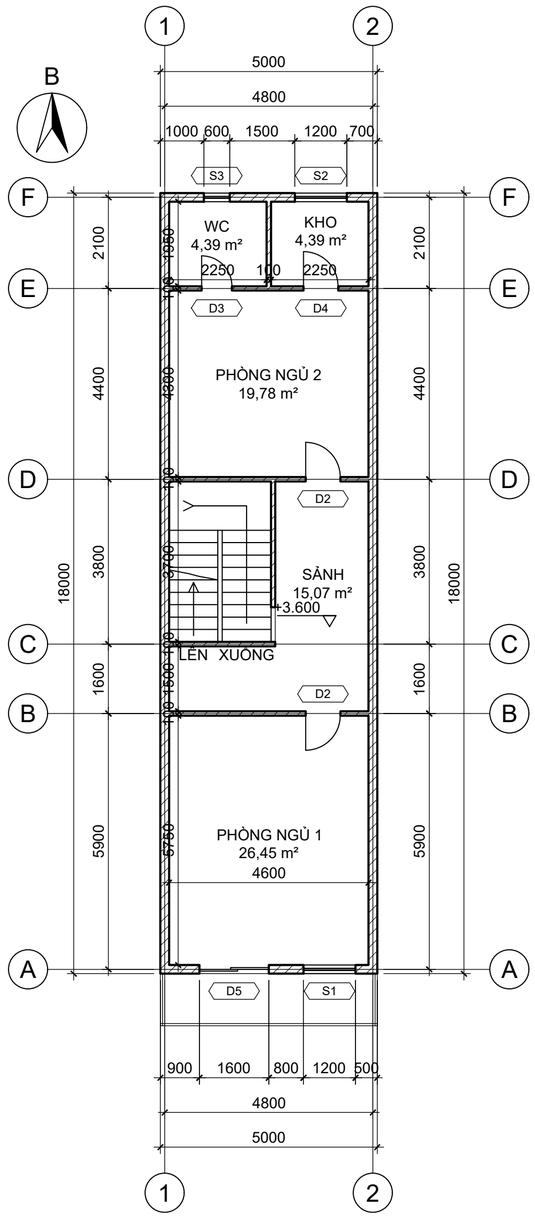

MẶT BẰNG TẦNG 2

TỶ LỆ: 1/100

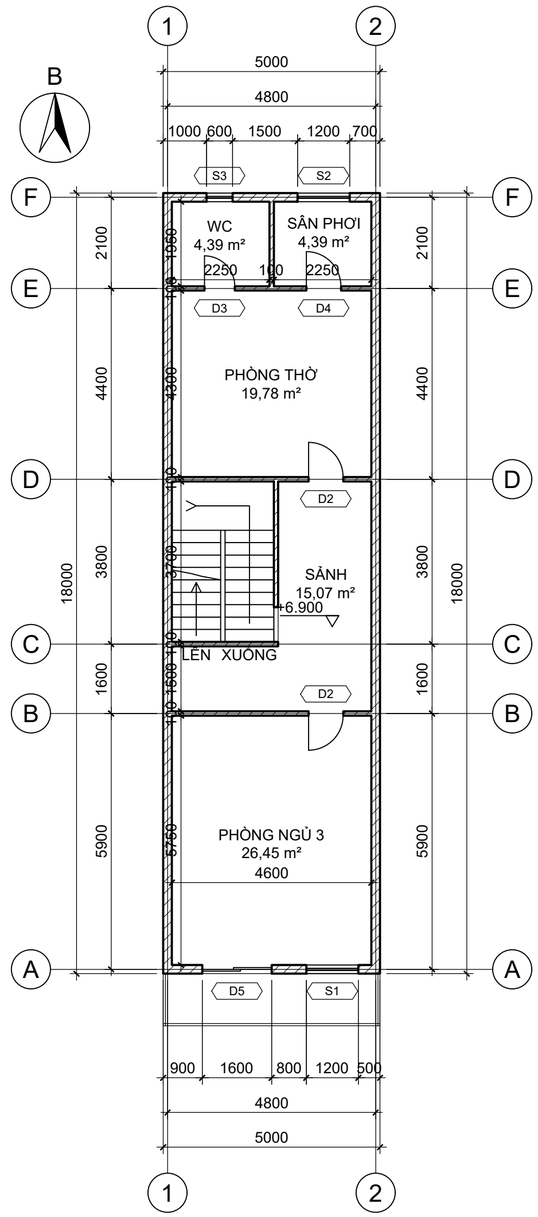

MẶT BẰNG TẦNG 3

TỶ LỆ: 1/100

LẦN NỘP	NỘI DUNG ĐIỀU CHỈNH	NGÀY NỘP
1		
2		
3		
4		

GHI CHÚ - Note:

CHỦ ĐẦU TƯ - Client:

CHỦ ĐẦU TƯ (MẪU)

DỰ ÁN - Project:

NHÀ PHỐ 5x18m, 3 TẦNG + TUM

Mẫu minh họa

HẠNG MỤC - Item:

KIẾN TRÚC

TƯ VẤN THIẾT KẾ - Consultant:

AUTOCAD MCP


CHỦ NHIỆM TK - Chief of Project	
CHỦ TRÌ TK - Chief of Division	
THIẾT KẾ - Designed by AutoCAD MCP	
KIỂM TRA - Checked by ...	

TÊN BẢN VẼ - Drawing name:

MẶT BẰNG TẦNG 1, TẦNG 2, TẦNG 3


SỐ HĐ - Contract No:	PHIÊN BẢN - Version 01
GIAI ĐOẠN - Phase: TKTC	KÝ HIỆU BẢN VẼ - Drawing No KT-01
TỶ LỆ - Scale: 1:100	HOÀN THÀNH - Finish: 03/11/2026

GHI CHÚ:NHÀ THẦU THI CÔNG KIỂM TRA KÍCH THƯỚC THỰC TẾ, NẾU THẤY CÓ XUNG ĐỘT CẦN BÁO LẠI CHO THIẾT KẾ VÀ QUẢN LÝ KỸ THUẬT.

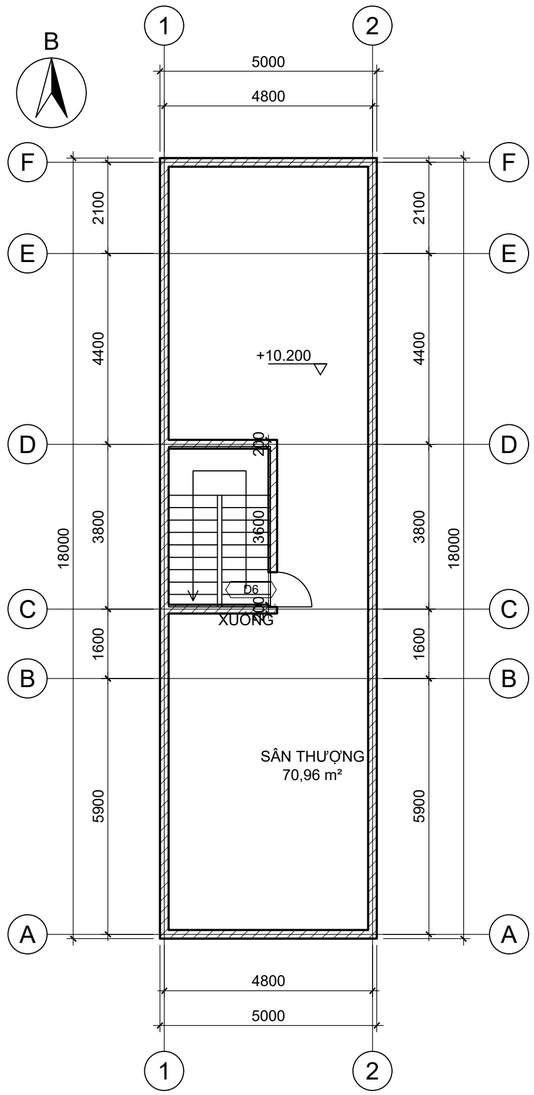

MẶT BẰNG TUM

TỶ LỆ: 1/100

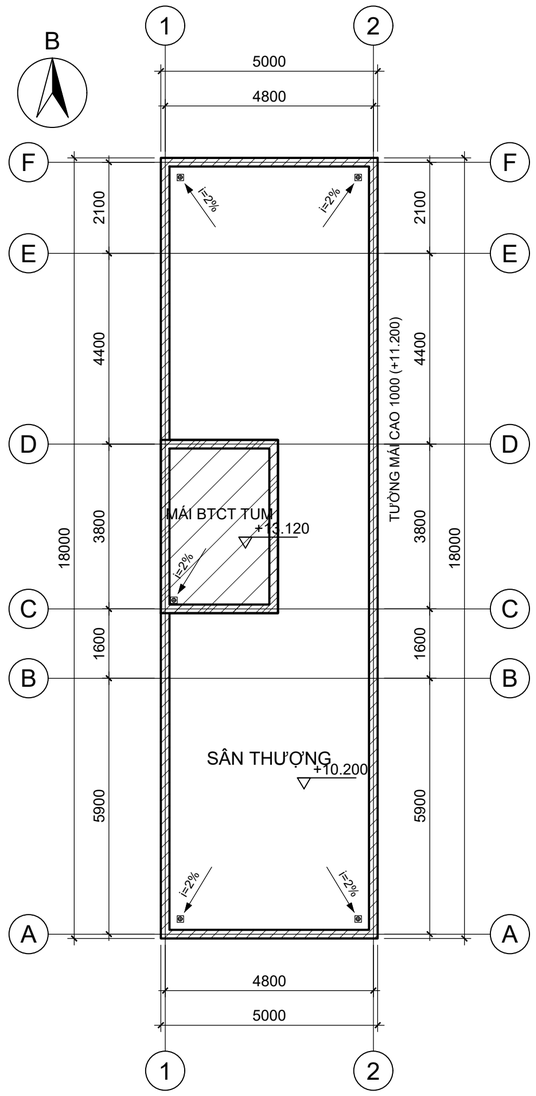

MẶT BẰNG MÁI

TỶ LỆ: 1/100

GHI CHÚ:

1. Mái BTCT chống thấm, láng vữa tạo dốc i=2% về phễu thu.
2. Ống thoát nước mưa uPVC Ø90 từ mỗi phễu thu xuống hệ thoát nước sân.
3. Tường mái cao 1000, có gờ chắn nước và chỉ nhỏ giọt trên đỉnh.

LẦN NỘP	NỘI DUNG ĐIỀU CHỈNH	NGÀY NỘP
1		
2		
3		
4		

GHI CHÚ - Note:

CHỦ ĐẦU TƯ - Client:

CHỦ ĐẦU TƯ (MẪU)

DỰ ÁN - Project:

NHÀ PHỐ 5x18m, 3 TẦNG + TUM

Mẫu minh họa

HẠNG MỤC - Item:

KIẾN TRÚC

TƯ VẤN THIẾT KẾ - Consultant:

AUTOCAD MCP


CHỦ NHIỆM TK - Chief of Project	
CHỦ TRÌ TK - Chief of Division	
THIẾT KẾ - Designed by AutoCAD MCP	
KIỂM TRA - Checked by ...	

TÊN BẢN VẼ - Drawing name:

MẶT BẰNG TUM, MẶT BẰNG MÁI


SỐ HĐ - Contract No:	PHIÊN BẢN - Version 01
GIAI ĐOẠN - Phase: TKTC	KÝ HIỆU BẢN VẼ - Drawing No KT-02
TỶ LỆ - Scale: 1:100	HOÀN THÀNH - Finish: 03/11/2026

GHI CHÚ:NHÀ THẦU THI CÔNG KIỂM TRA KÍCH THƯỚC THỰC TẾ, NẾU THẤY CÓ XUNG ĐỘT CẦN BÁO LẠI CHO THIẾT KẾ VÀ QUẢN LÝ KỸ THUẬT.

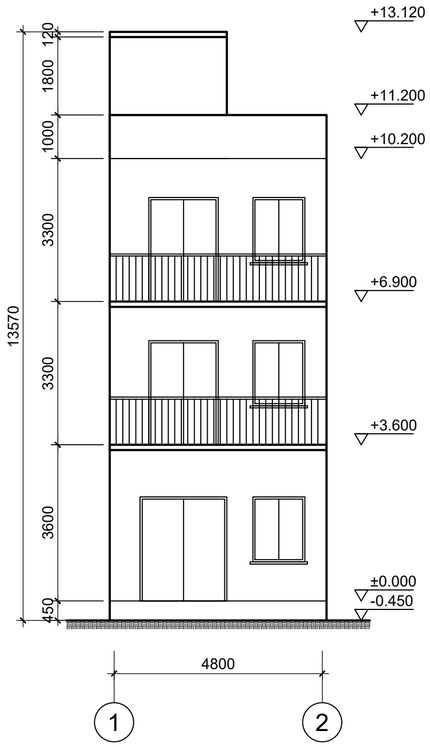


MẶT ĐỨNG CHÍNH (TRỤC A)

TỶ LỆ: 1/100

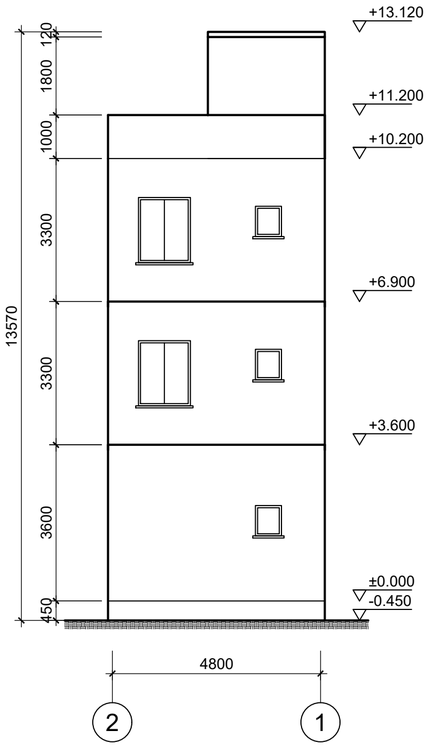

MẶT ĐỨNG SAU (TRỤC F)

TỶ LỆ: 1/100

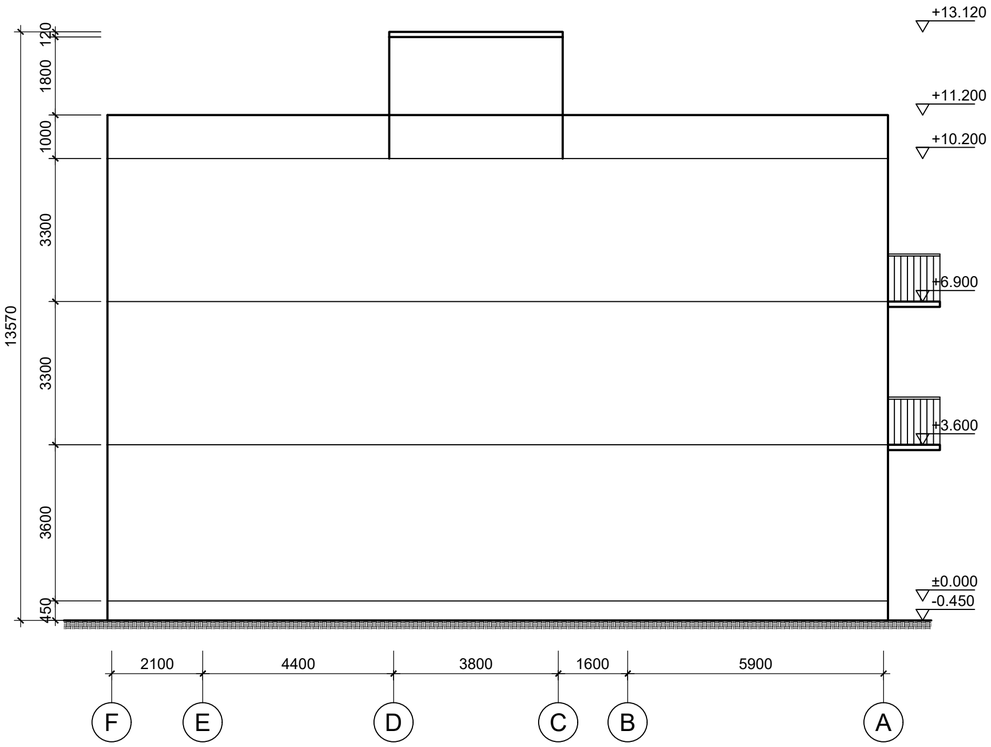

MẶT ĐỨNG TRỤC F-A

TỶ LỆ: 1/100

LẦN NỘP	NỘI DUNG ĐIỀU CHỈNH	NGÀY NỘP
1		
2		
3		
4		

GHI CHÚ - Note:

CHỦ ĐẦU TƯ - Client:

CHỦ ĐẦU TƯ (MẪU)

DỰ ÁN - Project:

NHÀ PHỐ 5x18m, 3 TẦNG + TUM

Mẫu minh họa

HẠNG MỤC - Item:

KIẾN TRÚC

TƯ VẤN THIẾT KẾ - Consultant:

AUTOCAD MCP


CHỦ NHIỆM TK - Chief of Project	
CHỦ TRÌ TK - Chief of Division	
THIẾT KẾ - Designed by AutoCAD MCP	
KIỂM TRA - Checked by ...	

TÊN BẢN VẼ - Drawing name:

MẶT ĐỨNG CHÍNH, MẶT ĐỨNG SAU, MẶT ĐỨNG BÊN


SỐ HĐ - Contract No:	PHIÊN BẢN - Version 01
GIAI ĐOẠN - Phase: TKTC	KÝ HIỆU BẢN VẼ - Drawing No KT-03
TỶ LỆ - Scale: 1:100	HOÀN THÀNH - Finish: 03/11/2026

GHI CHÚ:NHÀ THẦU THI CÔNG KIỂM TRA KÍCH THƯỚC THỰC TẾ, NẾU THẤY CÓ XUNG ĐỘT CẦN BÁO LẠI CHO THIẾT KẾ VÀ QUẢN LÝ KỸ THUẬT.

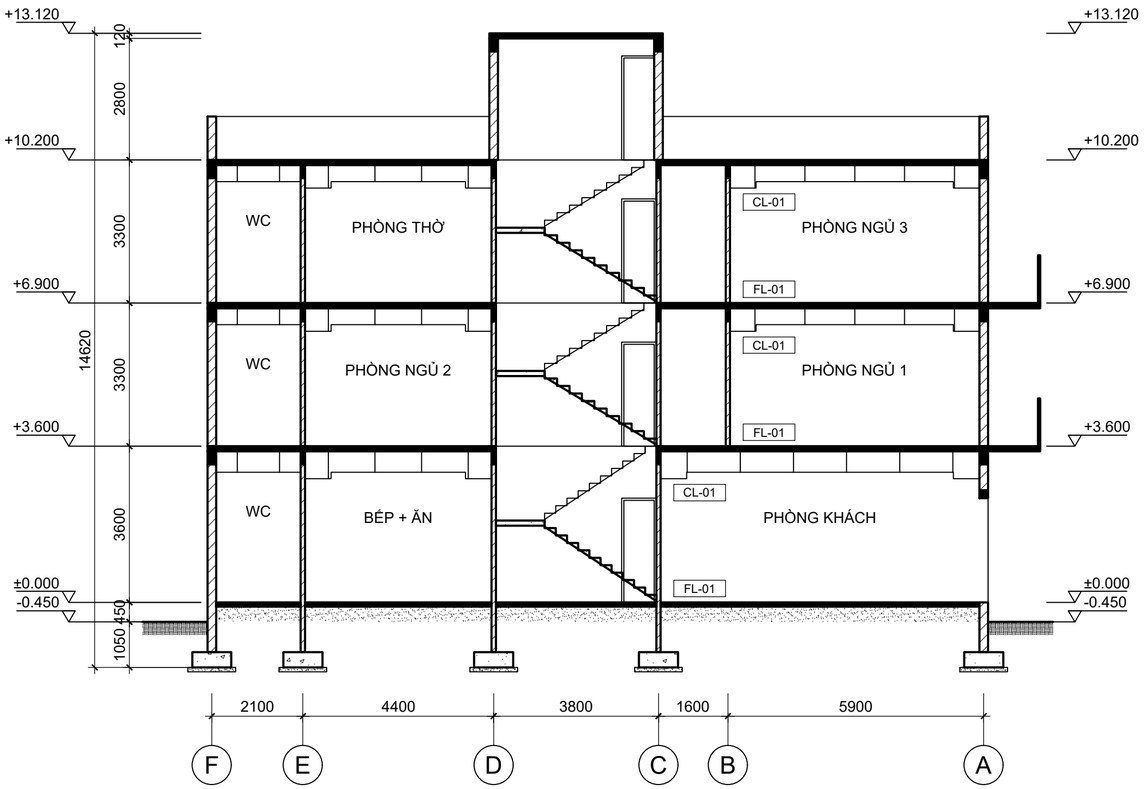

MẶT CẮT A-A

TỶ LỆ: 1/100

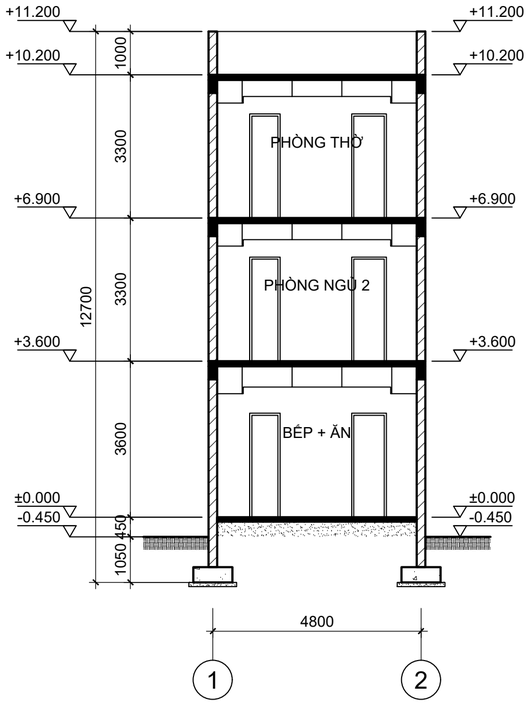

MẶT CẮT B-B

TỶ LỆ: 1/100

LẦN NỘP	NỘI DUNG ĐIỀU CHỈNH	NGÀY NỘP
1		
2		
3		
4		

GHI CHÚ - Note:

CHỦ ĐẦU TƯ - Client:

CHỦ ĐẦU TƯ (MẪU)

DỰ ÁN - Project:

NHÀ PHỐ 5x18m, 3 TẦNG + TUM

Mẫu minh họa

HẠNG MỤC - Item: KIẾN TRÚC

TƯ VẤN THIẾT KẾ - Consultant:

AUTOCAD MCP


CHỦ NHIỆM TK - Chief of Project	
CHỦ TRÌ TK - Chief of Division	
THIẾT KẾ - Designed by: AutoCAD MCP	
KIỂM TRA - Checked by: ...	

TÊN BẢN VẼ - Drawing name:

MẶT CẮT A-A, B-B


SỐ HĐ - Contract No:	PHIÊN BẢN - Version: 01
GIAI ĐOẠN - Phase: TKTC	KÝ HIỆU BẢN VẼ - Drawing No: KT-04
TỶ LỆ - Scale: 1:100	HOÀN THÀNH - Finish: 03/11/2026

GHI CHÚ: NHÀ THẦU THI CÔNG KIỂM TRA KÍCH THƯỚC THỰC TẾ, NẾU THẤY CÓ XUNG ĐỘT CẦN BÁO LẠI CHO THIẾT KẾ VÀ QUẢN LÝ KỸ THUẬT.

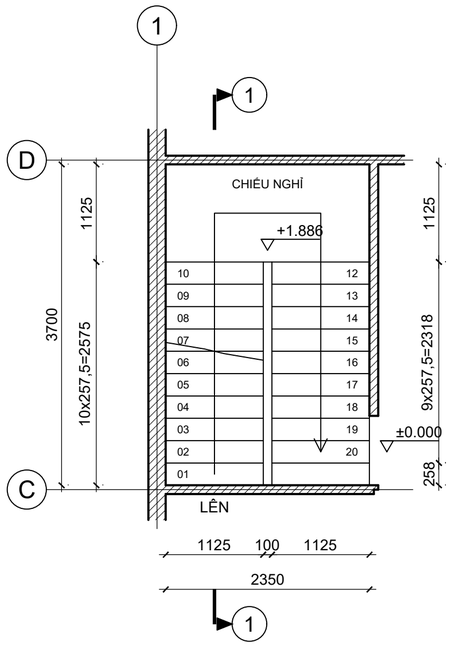


MẶT BẰNG THANG TẦNG 1

TỶ LỆ: 1/50

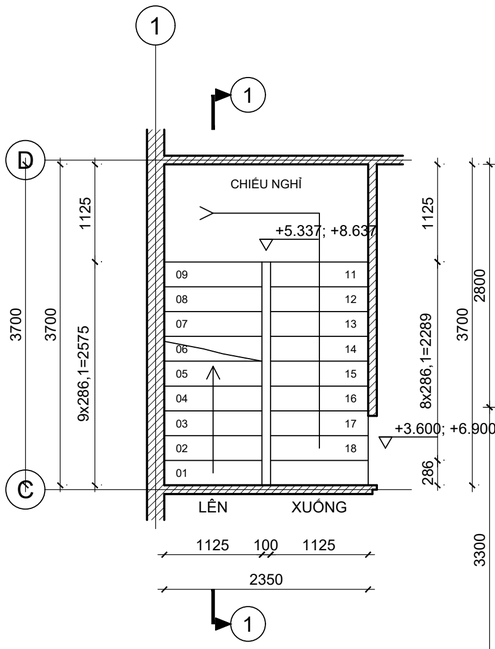

MẶT BẰNG THANG TẦNG 2, 3

TỶ LỆ: 1/50

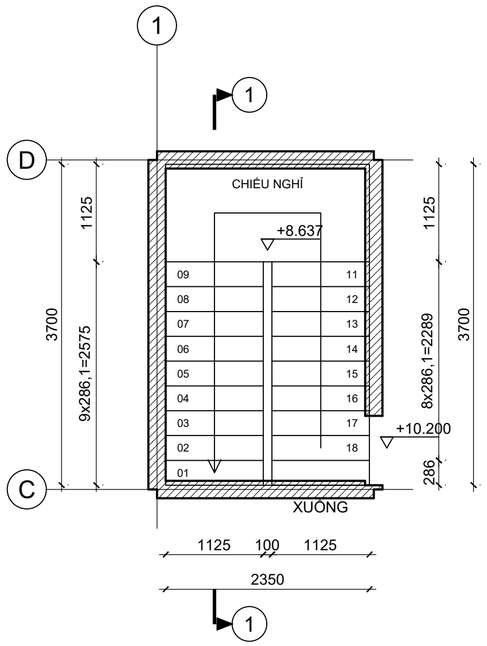


MẶT BẰNG THANG TUM

TỶ LỆ: 1/50


GHI CHÚ:

1. CẤU TẠO BẬC THANG (TH): Mặt bậc, cổ bậc đá granite dày 20, mũi bậc xẻ 2 rãnh chống trơn; Lớp vữa XM M75 dày 20; Bậc xây gạch thẻ VXM M75; Bản thang BTCT dày 120 (xem KC); Trát trần VXM M75 dày 15, bả matit, sơn nước hoàn thiện.
2. CẤU TẠO CHIẾU NGHỈ (CN): Đá granite dày 20; Lớp vữa XM M75 dày 20; Bản chiếu nghỉ BTCT dày 120 (xem KC); Trát trần VXM M75 dày 15, bả matit, sơn nước hoàn thiện.
3. Tay vịn gỗ tự nhiên 60x80, thanh đứng sắt hộp 14x14 (2 thanh mỗi bậc), sơn tĩnh điện; lan can cao 900 tính từ mũi bậc.
4. Chiều cao bậc h = 171,4, bề rộng bậc b = 257,5: 2h + b = 600 (nên 600 ÷ 650).
5. Về thang rộng 1125, chiếu nghỉ rộng 1125, khe giữa 2 vế 100.

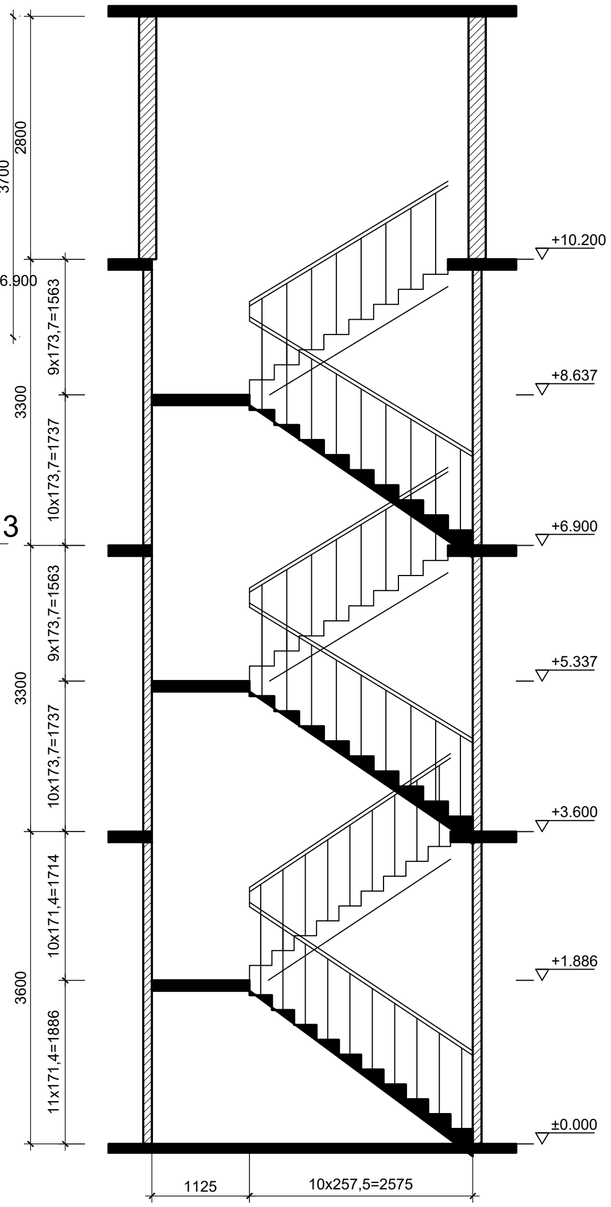

MẶT CẮT 1-1

TỶ LỆ: 1/50

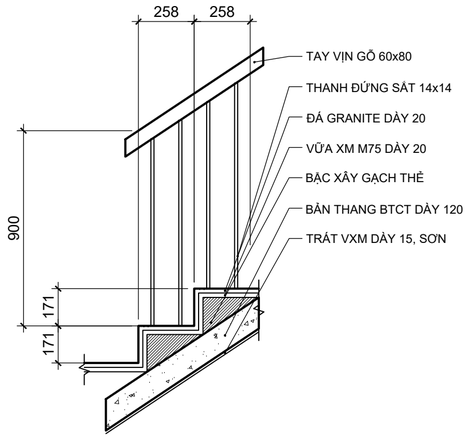

CHI TIẾT BẬC THANG

TỶ LỆ: 1/20

LẦN NỘP	NỘI DUNG ĐIỀU CHỈNH	NGÀY NỘP
1		
2		
3		
4		

GHI CHÚ - Note:

CHỦ ĐẦU TƯ - Client:

CHỦ ĐẦU TƯ (MẪU)

DỰ ÁN - Project:

NHÀ PHỐ 5x18m, 3 TẦNG + TUM

Mẫu minh họa

HẠNG MỤC - Item:

KIẾN TRÚC

TƯ VẤN THIẾT KẾ - Consultant:

AUTOCAD MCP


CHỦ NHIỆM TK - Chief of Project	
CHỦ TRÌ TK - Chief of Division	
THIẾT KẾ - Designed by: AutoCAD MCP	
KIỂM TRA - Checked by: ...	

TÊN BẢN VẼ - Drawing name:

CHI TIẾT CẦU THANG

SỐ HĐ - Contract No:	PHIÊN BẢN - Version: 01
GIAI ĐOẠN - Phase: TKTC	KÝ HIỆU BẢN VẼ - Drawing No: KT-05
TỶ LỆ - Scale: NHƯ HÌNH	HOÀN THÀNH - Finish: 03/11/2026

GHI CHÚ:NHÀ THẦU THI CÔNG KIỂM TRA KÍCH THƯỚC THỰC TẾ, NẾU THẤY CÓ XUNG ĐỘT CẦN BÁO LẠI CHO THIẾT KẾ VÀ QUẢN LÝ KỸ THUẬT.

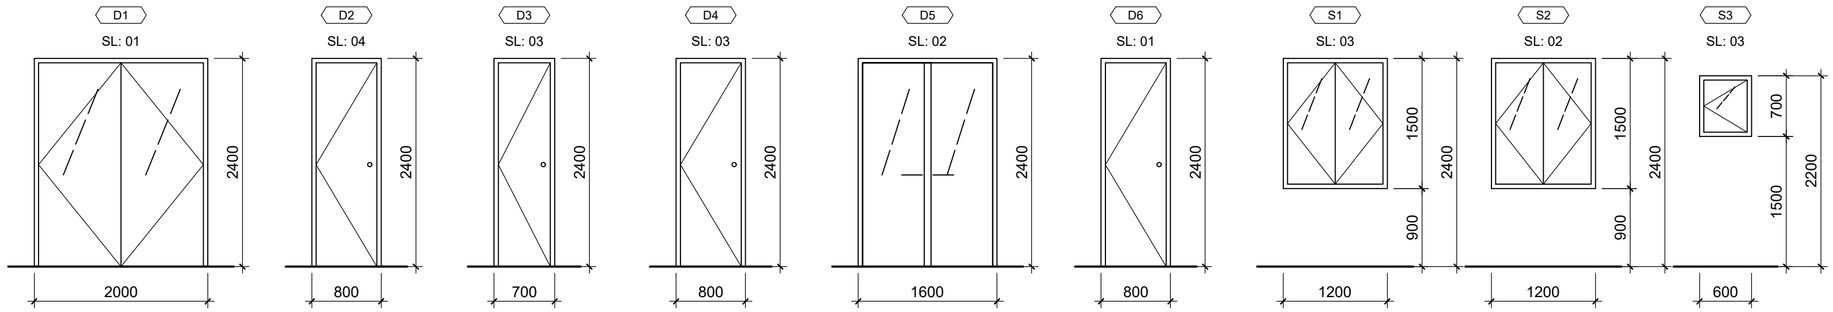

DANH MỤC CÁC LOẠI CỬA						
KÝ HIỆU	LOẠI CỬA	KÍCH THƯỚC (R x C)	CAO BẬU	SỐ LƯỢNG	VỊ TRÍ	VẬT LIỆU, MÔ TẢ
D1	Cửa đi 2 cánh mở quay	2000 x 2400		1	TẦNG 1: 1	Cửa nhôm hệ, kính cường lực 8 mm, phụ kiện đồng bộ
D2	Cửa đi 1 cánh mở quay	800 x 2400		4	TẦNG 2: 2; TẦNG 3: 2	Cửa gỗ công nghiệp, khung bao gỗ, sơn PU, phụ kiện đồng bộ
D3	Cửa đi 1 cánh mở quay	700 x 2400		3	TẦNG 1: 1; TẦNG 2: 1; TẦNG 3: 1	Cửa gỗ công nghiệp, khung bao gỗ, sơn PU, phụ kiện đồng bộ
D4	Cửa đi 1 cánh mở quay	800 x 2400		3	TẦNG 1: 1; TẦNG 2: 1; TẦNG 3: 1	Cửa gỗ công nghiệp, khung bao gỗ, sơn PU, phụ kiện đồng bộ
D5	Cửa đi lùa 2 cánh	1600 x 2400		2	TẦNG 2: 1; TẦNG 3: 1	Cửa lùa nhôm hệ, kính cường lực 8 mm
D6	Cửa đi 1 cánh mở quay	800 x 2400		1	TUM: 1	Cửa gỗ công nghiệp, khung bao gỗ, sơn PU, phụ kiện đồng bộ
S1	Cửa sổ mở quay	1200 x 1500	900	3	TẦNG 1: 1; TẦNG 2: 1; TẦNG 3: 1	Cửa sổ nhôm hệ, kính cường lực 6,38 mm, có song bảo vệ
S2	Cửa sổ mở quay	1200 x 1500	900	2	TẦNG 2: 1; TẦNG 3: 1	Cửa sổ nhôm hệ, kính cường lực 6,38 mm, có song bảo vệ
S3	Cửa sổ mở quay	600 x 700	1500	3	TẦNG 1: 1; TẦNG 2: 1; TẦNG 3: 1	Cửa sổ nhôm hệ, kính cường lực 6,38 mm, có song bảo vệ

BẢNG THỐNG KÊ CỬA ĐI, CỬA SỔ

TỶ LỆ: 1/50

GHI CHÚ:NHÀ THẦU THI CÔNG KIỂM TRA KÍCH THƯỚC THỰC TẾ, NẾU THẤY CÓ XUNG ĐỘT CẦN BÁO LẠI CHO THIẾT KẾ VÀ QUẢN LÝ KỸ THUẬT.

LẦN NỘP	NỘI DUNG ĐIỀU CHỈNH	NGÀY NỘP
1		
2		
3		
4		

GHI CHÚ - Note:

CHỦ ĐẦU TƯ - Client:

CHỦ ĐẦU TƯ (MẪU)

DỰ ÁN - Project:

NHÀ PHỐ 5x18m, 3 TẦNG + TUM

Mẫu minh họa

HẠNG MỤC - Item:

KIẾN TRÚC

TƯ VẤN THIẾT KẾ - Consultant:

AUTOCAD MCP

CHỦ NHIỆM TK - Chief of Project	
CHỦ TRÌ TK - Chief of Division	
THIẾT KẾ - Designed by AutoCAD MCP	
KIỂM TRA - Checked by ...	

TÊN BẢN VẼ - Drawing name:

BẢNG THỐNG KÊ CỬA ĐI, CỬA SỔ

SỐ HĐ - Contract No:	PHIÊN BẢN - Version 01
GIAI ĐOẠN - Phase: TKTC	KÝ HIỆU BẢN VẼ - Drawing No: KT-06
TỶ LỆ - Scale: 1:50	HOÀN THÀNH - Finish: 03/11/2026