HỒ SƠ BẢN VẼ NỘI THẤT

GIAI ĐOẠN: THIẾT KẾ THI CÔNG

CÔNG TRÌNH: NHÀ PHỐ 5x18m, 3 TẦNG + TUM

CHỦ ĐẦU TƯ: CHỦ ĐẦU TƯ (MẪU)

ĐƠN VỊ THIẾT KẾ: AUTOCAD MCP

ĐỊA ĐIỂM XÂY DỰNG: Mẫu minh họa

NGÀY: 11/2026

LẦN NỘP	NỘI DUNG ĐIỀU CHỈNH	NGÀY NỘP
1		
2		
3		
4		

GHI CHÚ - Note:

CHỦ ĐẦU TƯ - Client:
CHỦ ĐẦU TƯ (MẪU)

DỰ ÁN - Project:
NHÀ PHỐ 5x18m, 3 TẦNG + TUM
Mẫu minh họa

HẠNG MỤC - Item: NỘI THẤT

TƯ VẤN THIẾT KẾ - Consultant:
AUTOCAD MCP

CHỦ NHIỆM TK - Chief of Project:	
CHỦ TRÌ TK - Chief of Division:	
THIẾT KẾ - Designed by: AutoCAD MCP	
KIỂM TRA - Checked by:	

TÊN BẢN VẼ - Drawing name:
TỜ BÌA

SỐ HĐ - Contract No.	PHIÊN BẢN - Version: 01
GIAI ĐOẠN - Phase: TKTC	KÝ HIỆU BẢN VẼ - Drawing No.: NT-BIA
TỶ LỆ - Scale: 1:25	HOÀN THÀNH - Finish: 03/11/2026

GHI CHÚ: NHÀ THẦU THI CÔNG KIỂM TRA KÍCH THƯỚC THỰC TẾ, NẾU THẤY CÓ XUNG ĐỘT CẦN BÁO LẠI CHO THIẾT KẾ VÀ QUẢN LÝ KỸ THUẬT.

DANH MỤC BẢN VẼ - NỘI THẤT					
STT	KÝ HIỆU	TÊN BẢN VẼ	TỶ LỆ	KHỔ GIẤY	GHI CHÚ
1	NT-BIA	TỜ BÌA		A0	
2	NT-00	DANH MỤC BẢN VẼ NỘI THẤT	1:25	A0	
3	NT-01	MẶT BẰNG BỐ TRÍ NỘI THẤT TẦNG 1, 2, 3	1:50	A0	
4	NT-02	MẶT BẰNG HOÀN THIỆN SÀN TẦNG 1, 2, 3	1:50	A0	
5	NT-03	MẶT BẰNG HOÀN THIỆN TƯỜNG TẦNG 1, 2, 3	1:50	A0	
6	NT-04	MẶT BẰNG HOÀN THIỆN TRẦN TẦNG 1, 2, 3	1:50	A0	
7	NT-05	MẶT BẰNG BỐ TRÍ ĐÈN TẦNG 1, 2, 3	1:50	A0	
8	NT-06	MẶT ĐỨNG NỘI THẤT PHÒNG NGỦ 1 TẦNG 2	1:20	A0	
9	NT-07	BẢNG THỐNG KÊ VẬT LIỆU HOÀN THIỆN	1:50	A0	

GHI CHÚ: NHÀ THẦU THI CÔNG KIỂM TRA KÍCH THƯỚC THỰC TẾ, NẾU THẤY CÓ XUNG ĐỘT CẦN BÁO LẠI CHO THIẾT KẾ VÀ QUẢN LÝ KỸ THUẬT.

LẦN NỘP	NỘI DUNG ĐIỀU CHỈNH	NGÀY NỘP
1		
2		
3		
4		

Ghi CHÚ - Note:

CHỦ ĐẦU TƯ - Client:
CHỦ ĐẦU TƯ (MẪU)

DỰ ÁN - Project:
NHÀ PHỐ 5x18m, 3 TẦNG + TUM
Mẫu minh họa


HẠNG MỤC - Item:
NỘI THẤT

TƯ VẤN THIẾT KẾ - Consultant:
AUTOCAD MCP

CHỦ NHIỆM TK - Chief of Project:
CHỦ TRÌ TK - Chief of Division:
THIẾT KẾ - Designed by: AutoCAD MCP
KIỂM TRA - Checked by:


TÊN BẢN VẼ - Drawing name:
DANH MỤC BẢN VẼ NỘI THẤT

SỐ HĐ - Contract No.:
PHIÊN BẢN - Version: 01
Giai đoạn - Phase: TKTC
KÝ HIỆU BẢN VẼ - Drawing No.: NT-00
TỶ LỆ - Scale: 1:25
HOÀN THÀNH - Finish: 03/11/2026

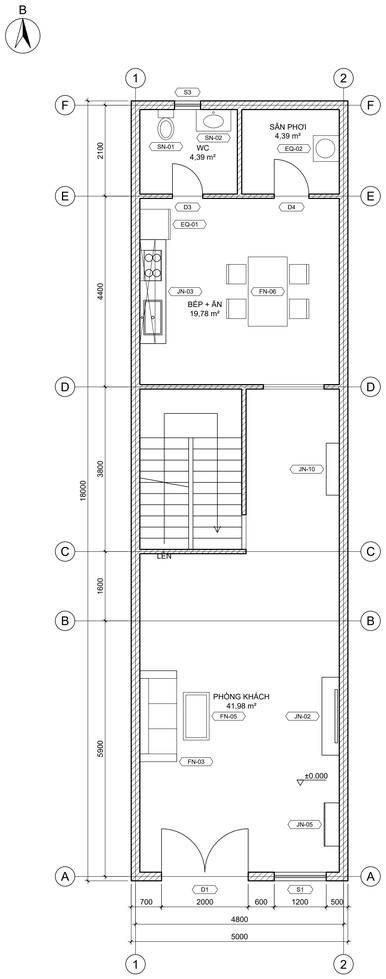


MẶT BẰNG BỐ TRÍ NỘI THẤT TẦNG 1

TỶ LỆ: 1/50

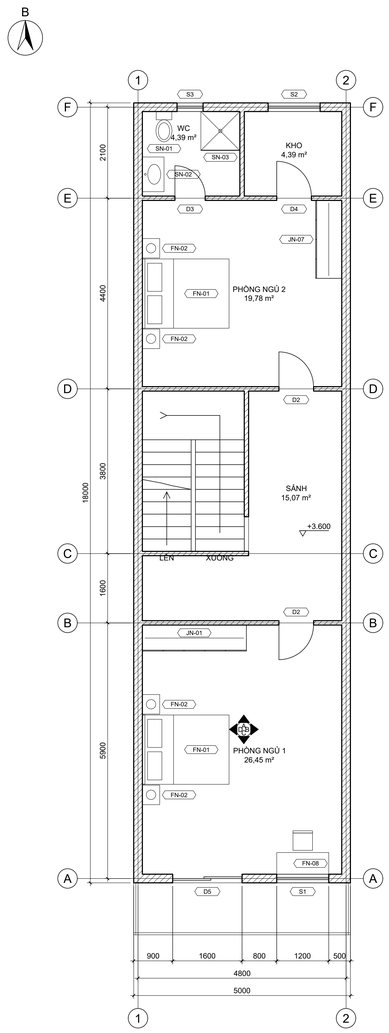

MẶT BẰNG BỐ TRÍ NỘI THẤT TẦNG 2

TỶ LỆ: 1/50

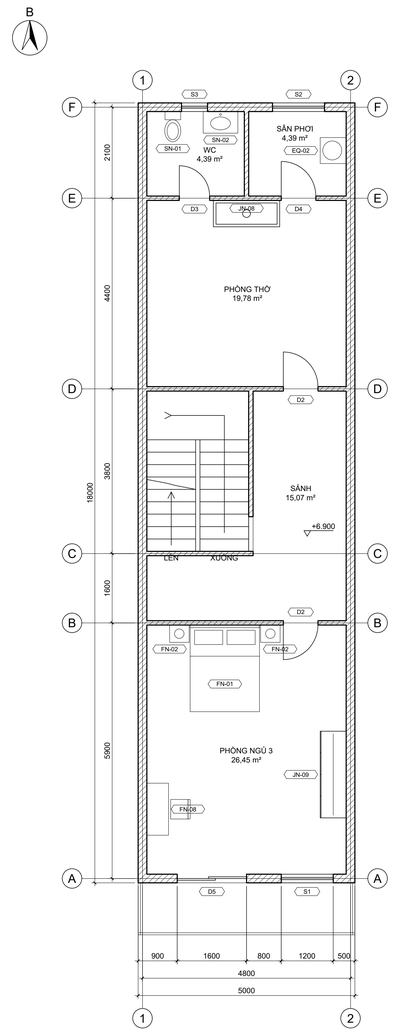

MẶT BẰNG BỐ TRÍ NỘI THẤT TẦNG 3

TỶ LỆ: 1/50

GHI CHÚ:

1. Kích thước ghi bằng mm, cao độ ghi bằng m, tính từ mặt sàn hoàn thiện của tầng.
2. Nhà thầu kiểm tra kích thước thực tế tại công trình trước khi thi công, báo lại thiết kế khi có sai khác.
3. Vật liệu theo mã trong bảng thống kê vật liệu hoàn thiện; mẫu vật liệu trình chủ đầu tư và thiết kế duyệt trước khi thi công.
4. Đồ rời (FN) thể hiện vị trí bố trí; đồ gỗ đóng tại chỗ (JN) theo bản vẽ chi tiết đồ gỗ.
5. Thiết bị vệ sinh (SN), thiết bị (EQ) lắp đặt theo hướng dẫn của nhà sản xuất; chờ sẵn cấp thoát nước, điện theo vị trí thiết bị.

LẦN NỘP	NỘI DUNG ĐIỀU CHỈNH	NGÀY NỘP
1		
2		
3		
4		

Ghi CHÚ - Note:

CHỦ ĐẦU TƯ - Client:

CHỦ ĐẦU TƯ (MẪU)

DỰ ÁN - Project:

NHÀ PHỐ 5x18m, 3 TẦNG + TUM

Mẫu minh họa

HẠNG MỤC - Item:

NỘI THẤT

TƯ VẤN THIẾT KẾ - Consultant:

AUTOCAD MCP


CHỦ NHIỆM TK - Chief of Project	
CHỦ TRÌ TK - Chief of Division	
THIẾT KẾ - Designed by: AutoCAD MCP	
KIỂM TRA - Checked by	

TÊN BẢN VẼ - Drawing name:

MẶT BẰNG BỐ TRÍ NỘI THẤT TẦNG 1, 2, 3

SỐ HĐ - Contract No	PHIÊN BẢN - Version: 01
GIAI ĐOẠN - Phase: TKTC	KÝ HIỆU BẢN VẼ - Drawing No: NT-01
TỶ LỆ - Scale: 1:50	HOÀN THÀNH - Finish: 03/11/2026

GHI CHÚ: NHÀ THẦU THI CÔNG KIỂM TRA KÍCH THƯỚC THỰC TẾ, NẾU THẤY CÓ XUNG ĐỘT CẦN BÁO LẠI CHO THIẾT KẾ VÀ QUẢN LÝ KỸ THUẬT.

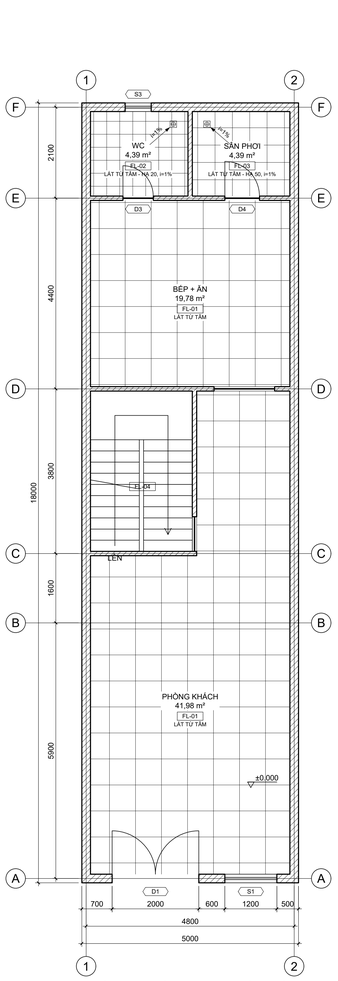


MẶT BẰNG HOÀN THIỆN SÀN TẦNG 1

TỶ LỆ: 1/50

CHÚ THÍCH VẬT LIỆU SÀN

- FL-01 Gạch porcelain 600x600 — 61,76 m² (PHÒNG KHÁCH, BẾP + ĂN)
- FL-04 Đá granite ốp bậc thang và chiếu nghỉ — 8,70 m² (CẦU THANG)
- FL-02 Gạch chống trơn 300x300 — 4,39 m² (WC)
- FL-03 Gạch chống trơn ngoài trời 400x400 — 4,39 m² (SÂN PHƠI)
- Nẹp chuyển tiếp inox
- Phễu thu sàn, dốc i=1% về phễu

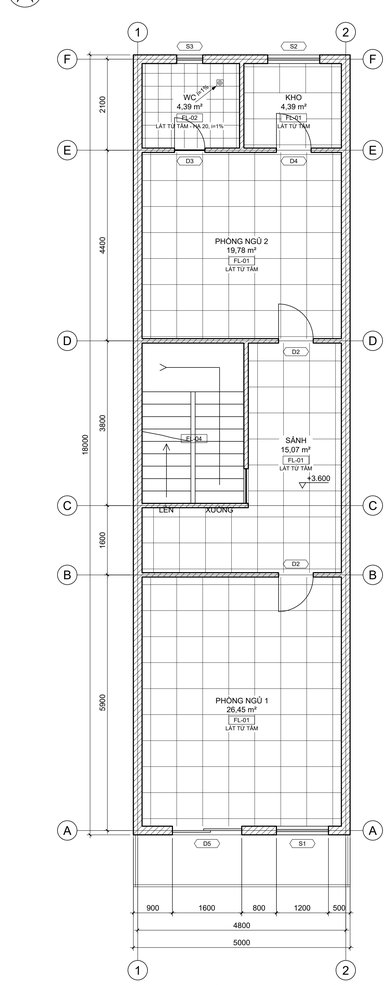


MẶT BẰNG HOÀN THIỆN SÀN TẦNG 2

TỶ LỆ: 1/50

CHÚ THÍCH VẬT LIỆU SÀN

- FL-01 Gạch porcelain 600x600 — 65,69 m² (PHÒNG NGỦ 1, SẢNH, PHÒNG NGỦ 2, KHO)
- FL-04 Đá granite ốp bậc thang và chiếu nghỉ — 8,70 m² (CẦU THANG)
- FL-02 Gạch chống trơn 300x300 — 4,39 m² (WC)
- Nẹp chuyển tiếp inox
- Phễu thu sàn, dốc i=1% về phễu

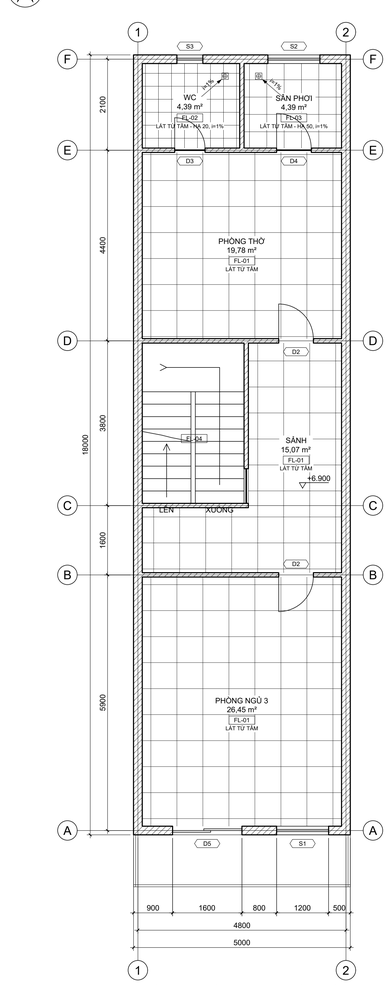

MẶT BẰNG HOÀN THIỆN SÀN TẦNG 3

TỶ LỆ: 1/50

CHÚ THÍCH VẬT LIỆU SÀN

- FL-01 Gạch porcelain 600x600 — 61,30 m² (PHÒNG NGỦ 3, SẢNH, PHÒNG THỜ)
- FL-04 Đá granite ốp bậc thang và chiếu nghỉ — 8,70 m² (CẦU THANG)
- FL-02 Gạch chống trơn 300x300 — 4,39 m² (WC)
- FL-03 Gạch chống trơn ngoài trời 400x400 — 4,39 m² (SÂN PHƠI)
- Nẹp chuyển tiếp inox
- Phễu thu sàn, dốc i=1% về phễu

GHI CHÚ:

1. Kích thước ghi bằng mm, cao độ ghi bằng m, tính từ mặt sàn hoàn thiện của tầng.
2. Nhà thầu kiểm tra kích thước thực tế tại công trình trước khi thi công, báo lại thiết kế khi có sai khác.
3. Vật liệu theo mã trong bảng thống kê vật liệu hoàn thiện; mẫu vật liệu trình chủ đầu tư và thiết kế duyệt trước khi thi công.
4. Gạch lát mạch 2 mm, keo chà ron màu theo mẫu duyệt; lát từ tâm phòng (ghi LÁT TỪ TÂM) hoặc từ điểm ghi trên bản vẽ.
5. Sàn khu vệ sinh hạ 20 mm, sân và ban công hạ 50 mm so với sàn trong nhà; chống thấm trước khi lát, dốc i=1% về phễu thu.
6. Nẹp chuyển tiếp inox dưới cánh cửa tại vị trí thay đổi vật liệu hoặc cao độ sàn.

LẦN NỘP	NỘI DUNG ĐIỀU CHỈNH	NGÀY NỘP
1		
2		
3		
4		

Ghi CHÚ - Note:

GHI CHÚ: NHÀ THẦU THI CÔNG KIỂM TRA KÍCH THƯỚC THỰC TẾ; NẾU THẤY CÓ XUNG ĐỘT CẦN BÁO LẠI CHO THIẾT KẾ VÀ QUẢN LÝ KỸ THUẬT.

CHỦ ĐẦU TƯ - Client:
CHỦ ĐẦU TƯ (MẪU)

DỰ ÁN - Project:
NHÀ PHỐ 5x18m, 3 TẦNG + TUM
Mẫu minh họa


HẠNG MỤC - Item:
NỘI THẤT

TƯ VẤN THIẾT KẾ - Consultant:
AUTOCAD MCP

CHỦ NHIỆM TK - Chief of Project:
CHỦ TRÌ TK - Chief of Division:
THIẾT KẾ - Designed by: AutoCAD MCP
KIỂM TRA - Checked by:

TÊN BẢN VẼ - Drawing name:
MẶT BẰNG HOÀN THIỆN SÀN TẦNG 1, 2, 3

SỐ HĐ - Contract No:
PHIÊN BẢN - Version: 01
GIAI ĐOẠN - Phase: TKTC
KÝ HIỆU BẢN VẼ - Drawing No: NT-02
TỶ LỆ - Scale: 1:50
HOÀN THÀNH - Finish: 03/11/2026

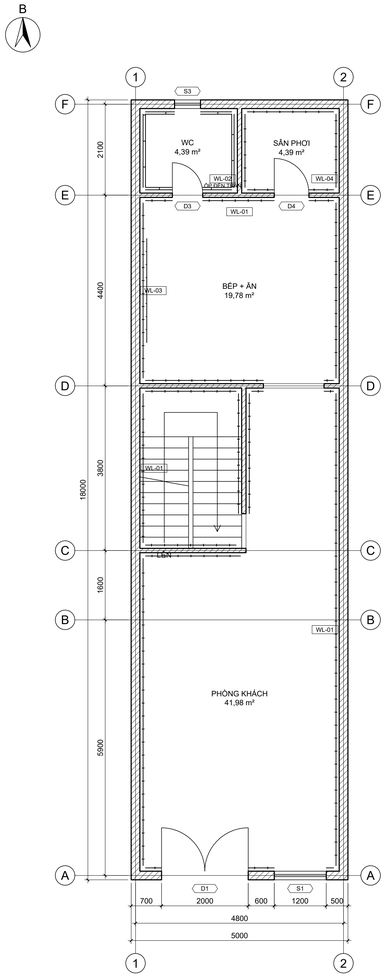


CHÚ THÍCH VẬT LIỆU TƯỜNG

- WL-01 — Sơn nước hoàn thiện màu trắng
  161,75 m² (PHÒNG KHÁCH, CẦU THANG, BẾP + ĂN)
- WL-02 — Gạch ốp tường 300x600 ốp đến trần
  23,10 m² (WC)
- WL-03 — Gạch ốp tường bếp 600x300
  1,56 m² (BẾP + ĂN)
- WL-04 — Sơn ngoại thất màu trắng
  28,32 m² (SÂN PHƠI)

MẶT BẰNG HOÀN THIỆN TƯỜNG TẦNG 1

TỶ LỆ: 1/50

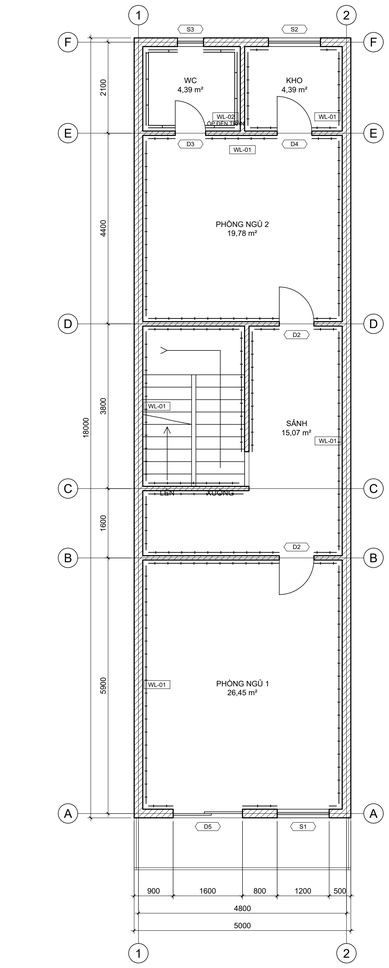


CHÚ THÍCH VẬT LIỆU TƯỜNG

- WL-01 — Sơn nước hoàn thiện màu trắng
  192,21 m² (PHÒNG NGỦ 1, SẢNH, CẦU THANG, PHÒNG NGỦ 2, KHO)
- WL-02 — Gạch ốp tường 300x600 ốp đến trần
  21,42 m² (WC)

MẶT BẰNG HOÀN THIỆN TƯỜNG TẦNG 2

TỶ LỆ: 1/50

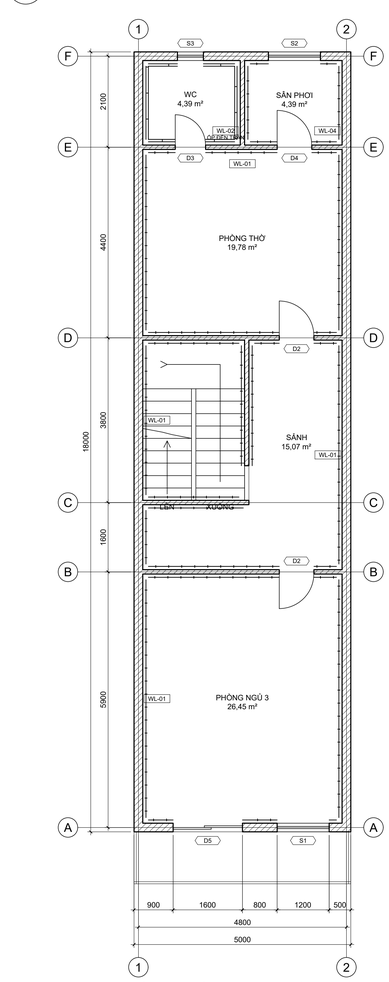

CHÚ THÍCH VẬT LIỆU TƯỜNG

- WL-01 — Sơn nước hoàn thiện màu trắng
  173,87 m² (PHÒNG NGỦ 3, SẢNH, CẦU THANG, PHÒNG THỜ)
- WL-02 — Gạch ốp tường 300x600 ốp đến trần
  21,42 m² (WC)
- WL-04 — Sơn ngoại thất màu trắng
  24,00 m² (SÂN PHƠI)

GHI CHÚ:

1. Kích thước ghi bằng mm, cao độ ghi bằng m, tính từ mặt sàn hoàn thiện của tầng.
2. Nhà thầu kiểm tra kích thước thực tế tại công trình trước khi thi công, báo lại thiết kế khi có sai khác.
3. Vật liệu theo mã trong bảng thống kê vật liệu hoàn thiện; mẫu vật liệu trình chủ đầu tư và thiết kế duyệt trước khi thi công.
4. Tường sơn: bả matit 2 lớp, sơn lót kháng kiềm 1 lớp, sơn phủ 2 lớp theo mã màu duyệt.
5. Gạch ốp tường mạch 2 mm, ốp từ mặt sàn hoàn thiện; khu vệ sinh ốp đến trần, chống thấm chân tường cao 300 trước khi ốp.
6. Khu bếp ốp gạch từ mặt đá bếp đến đáy tủ bếp trên.

MẶT BẰNG HOÀN THIỆN TƯỜNG TẦNG 3

TỶ LỆ: 1/50

LẦN NỘP	NỘI DUNG ĐIỀU CHỈNH	NGÀY NỘP
1		
2		
3		
4		

Ghi CHÚ - Note:

CHỦ ĐẦU TƯ - Client:
CHỦ ĐẦU TƯ (MẪU)

DỰ ÁN - Project:
NHÀ PHỐ 5x18m, 3 TẦNG + TUM
Mẫu minh họa

HẠNG MỤC - Item:
NỘI THẤT


TƯ VẤN THIẾT KẾ - Consultant:
AUTOCAD MCP

CHỦ NHIỆM TK - Chief of Project
CHỦ TRÌ TK - Chief of Division
THIẾT KẾ - Designed by: AutoCAD MCP
KIỂM TRA - Checked by

TÊN BẢN VẼ - Drawing name:
MẶT BẰNG HOÀN THIỆN TƯỜNG TẦNG 1, 2, 3

SỐ HĐ - Contract No.
PHIÊN BẢN - Version: 01
GIAI ĐOẠN - Phase: TKTC
KÝ HIỆU BẢN VẼ - Drawing No.: NT-03
TỶ LỆ - Scale: 1:50
HOÀN THÀNH - Finish: 03/11/2026

GHI CHÚ: NHÀ THẦU THI CÔNG KIỂM TRA KÍCH THƯỚC THỰC TẾ, NẾU THẤY CÓ XUNG ĐỘT CẦN BÁO LẠI CHO THIẾT KẾ VÀ QUẢN LÝ KỸ THUẬT.

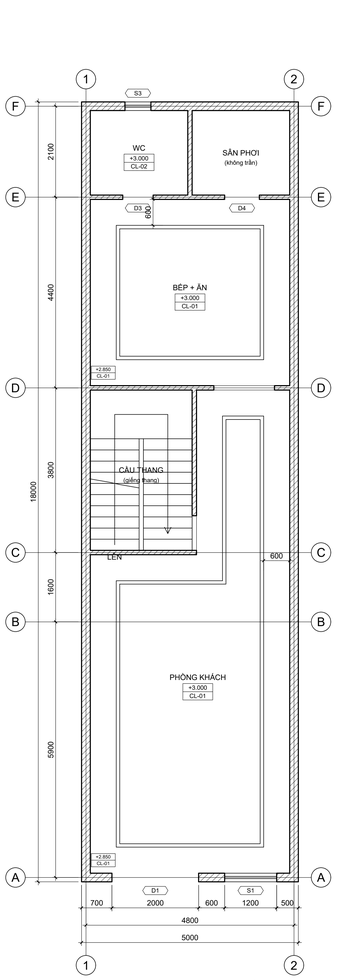


CHÚ THÍCH VẬT LIỆU TRẦN

CL-01 Trần thạch cao khung chìm, sơn trắng
cao độ +2.850, +3.000; 61,76 m² (PHÒNG KHÁCH, BẾP + ĂN)

CL-02 Trần thạch cao chống ẩm khung chìm, sơn trắng
cao độ +3.000; 4,39 m² (WC)

MẶT BẰNG HOÀN THIỆN TRẦN TẦNG 1

TỶ LỆ: 1/50

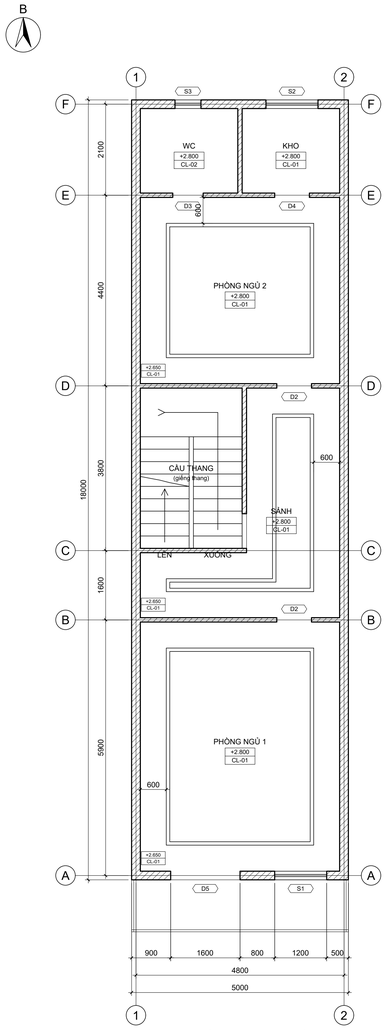


CHÚ THÍCH VẬT LIỆU TRẦN

CL-01 Trần thạch cao khung chìm, sơn trắng
cao độ +2.650, +2.800; 65,69 m² (PHÒNG NGỦ 1, SẢNH, PHÒNG NGỦ 2, KHO)

CL-02 Trần thạch cao chống ẩm khung chìm, sơn trắng
cao độ +2.800; 4,39 m² (WC)

MẶT BẰNG HOÀN THIỆN TRẦN TẦNG 2

TỶ LỆ: 1/50

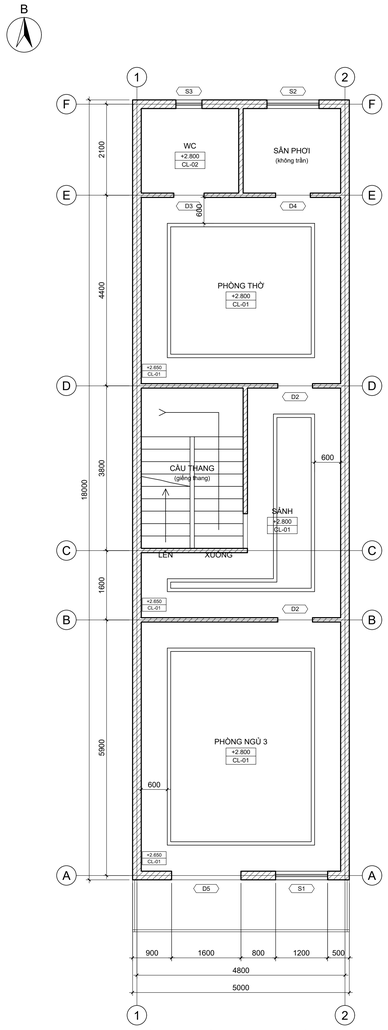

CHÚ THÍCH VẬT LIỆU TRẦN

CL-01 Trần thạch cao khung chìm, sơn trắng
cao độ +2.650, +2.800; 61,30 m² (PHÒNG NGỦ 3, SẢNH, PHÒNG THỜ)

CL-02 Trần thạch cao chống ẩm khung chìm, sơn trắng
cao độ +2.800; 4,39 m² (WC)

GHI CHÚ:

1. Kích thước ghi bằng mm, cao độ ghi bằng m, tính từ mặt sàn hoàn thiện của tầng.
2. Nhà thầu kiểm tra kích thước thực tế tại công trình trước khi thi công, báo lại thiết kế khi có sai khác.
3. Vật liệu theo mã trong bảng thống kê vật liệu hoàn thiện; mẫu vật liệu trình chủ đầu tư và thiết kế duyệt trước khi thi công.
4. Trần thạch cao khung chìm, tấm dày 9 mm; khu ẩm ướt dùng tấm chống ẩm; bả, sơn hoàn thiện như tường.
5. Cao độ trần tính từ mặt sàn hoàn thiện; giật cấp và khe hắt đèn theo kích thước trên bản vẽ.
6. Bố trí lỗ thăm trần 600x600 tại vị trí thiết bị kỹ thuật (máy lạnh, quạt hút, van).

MẶT BẰNG HOÀN THIỆN TRẦN TẦNG 3

TỶ LỆ: 1/50

GHI CHÚ: NHÀ THẦU THI CÔNG KIỂM TRA KÍCH THƯỚC THỰC TẾ, NẾU THẤY CÓ XUNG ĐỘT CẦN BÁO LẠI CHO THIẾT KẾ VÀ QUẢN LÝ KỸ THUẬT.

LẦN NỘP	NỘI DUNG ĐIỀU CHỈNH	NGÀY NỘP
1		
2		
3		
4		

Ghi CHÚ - Note:

CHỦ ĐẦU TƯ - Client:
CHỦ ĐẦU TƯ (MẪU)

DỰ ÁN - Project:
NHÀ PHỐ 5x18m, 3 TẦNG + TUM
Mẫu minh họa


HẠNG MỤC - Item:
NỘI THẤT

TƯ VẤN THIẾT KẾ - Consultant:
AUTOCAD MCP

CHỦ NHIỆM TK - Chief of Project:
CHỦ TRÌ TK - Chief of Division:
THIẾT KẾ - Designed by: AutoCAD MCP
KIỂM TRA - Checked by:

TÊN BẢN VẼ - Drawing name:
MẶT BẰNG HOÀN THIỆN TRẦN TẦNG 1, 2, 3

SỐ HĐ - Contract No:
PHIÊN BẢN - Version: 01
GIAI ĐOẠN - Phase: TKTC
KÝ HIỆU BẢN VẼ - Drawing No: NT-04
TỶ LỆ - Scale: 1:50
HOÀN THÀNH - Finish: 03/11/2026

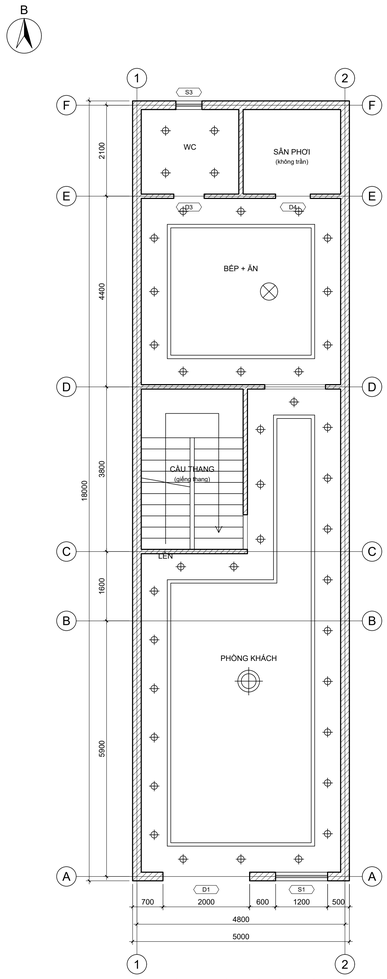


KÝ HIỆU ĐÈN

- LT-01 Đèn downlight âm trần Ø90: 40 cái
- LT-03 Đèn ốp trần: 1 cái
- LT-04 Đèn thả: 1 cái
- LT-02 Đèn LED dây hắt trần: 38,4 m

MẶT BẰNG BỐ TRÍ ĐÈN TẦNG 1

TỶ LỆ: 1/50

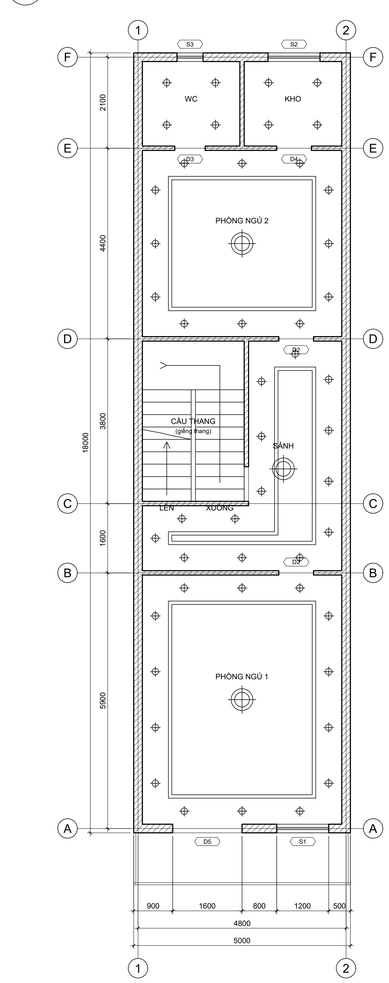


KÝ HIỆU ĐÈN

- LT-01 Đèn downlight âm trần Ø90: 48 cái
- LT-03 Đèn ốp trần: 3 cái
- LT-02 Đèn LED dây hắt trần: 42,0 m

MẶT BẰNG BỐ TRÍ ĐÈN TẦNG 2

TỶ LỆ: 1/50

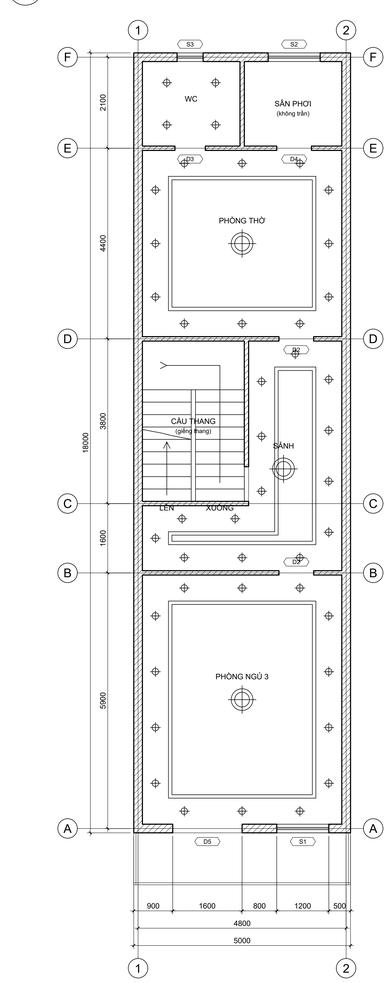

KÝ HIỆU ĐÈN

- LT-01 Đèn downlight âm trần Ø90: 44 cái
- LT-03 Đèn ốp trần: 3 cái
- LT-02 Đèn LED dây hắt trần: 42,0 m

GHI CHÚ:

1. Kích thước ghi bằng mm, cao độ ghi bằng m, tính từ mặt sàn hoàn thiện của tầng.
2. Nhà thầu kiểm tra kích thước thực tế tại công trình trước khi thi công, báo lại thiết kế khi có sai khác.
3. Vật liệu theo mã trong bảng thống kê vật liệu hoàn thiện; mẫu vật liệu trình chủ đầu tư và thiết kế duyệt trước khi thi công.
4. Vị trí đèn định vị theo tim đèn, đo từ mặt tường hoàn thiện.
5. Chủng loại, công suất, nhiệt độ màu của đèn theo bảng ký hiệu đèn và chỉ dẫn kỹ thuật.
6. Phối hợp bản vẽ điện để bố trí công tắc, ổ cắm và mạch đèn.

MẶT BẰNG BỐ TRÍ ĐÈN TẦNG 3

TỶ LỆ: 1/50

LẦN NỘP	NỘI DUNG ĐIỀU CHỈNH	NGÀY NỘP
1		
2		
3		
4		

Ghi CHÚ - Note:

CHỦ ĐẦU TƯ - Client:

CHỦ ĐẦU TƯ (MẪU)

DỰ ÁN - Project:

NHÀ PHỐ 5x18m, 3 TẦNG + TUM

Mẫu minh họa

HẠNG MỤC - Item:

NỘI THẤT

TƯ VẤN THIẾT KẾ - Consultant:

AUTOCAD MCP

CHỦ NHIỆM TK - Chief of Project	
CHỦ TRÌ TK - Chief of Division	
THIẾT KẾ - Designed by: AutoCAD MCP	
KIỂM TRA - Checked by	

TÊN BẢN VẼ - Drawing name:


MẶT BẰNG BỐ TRÍ ĐÈN TẦNG 1, 2, 3

SỐ HỒ - Contract No	PHIÊN BẢN - Version
	01
GIAI ĐOẠN - Phase: TKTC	KÝ HIỆU BẢN VẼ - Drawing No: NT-05
TỶ LỆ - Scale: 1:50	HOÀN THÀNH - Finish: 03/11/2026

GHI CHÚ: NHÀ THẦU THI CÔNG KIỂM TRA KÍCH THƯỚC THỰC TẾ, NẾU THẤY CÓ XUNG ĐỘT CẦN BÁO LẠI CHO THIẾT KẾ VÀ QUẢN LÝ KỸ THUẬT.


JN NỘI	NỘI DUNG ĐIỀU CHỈNH	NGÀY NỘP
1		
2		
3		
4		

Ghi CHÚ - Note:

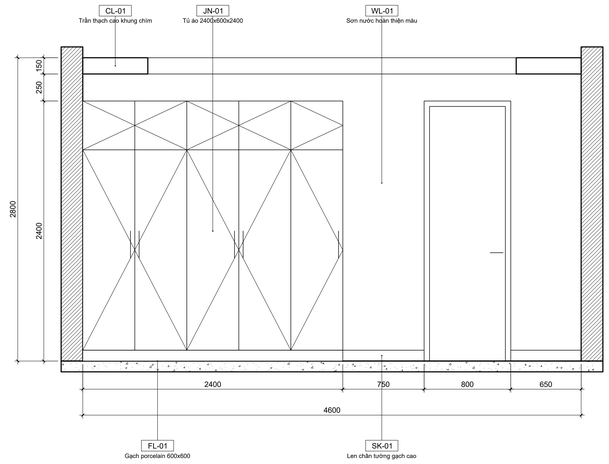


MẶT ĐỨNG A - PHÒNG NGỦ 1

TỶ LỆ: 1/20

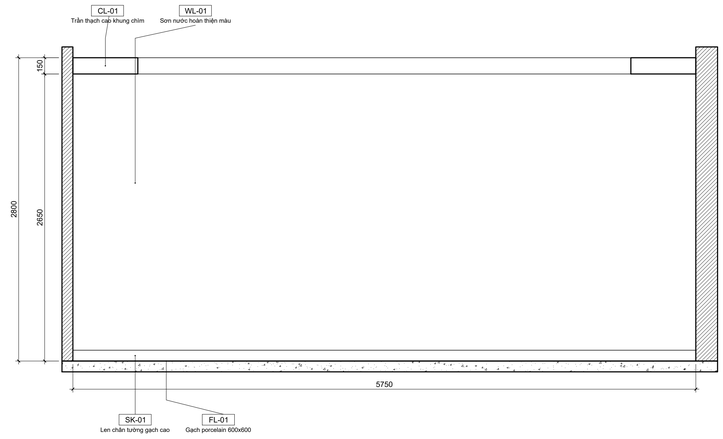


MẶT ĐỨNG B - PHÒNG NGỦ 1

TỶ LỆ: 1/20

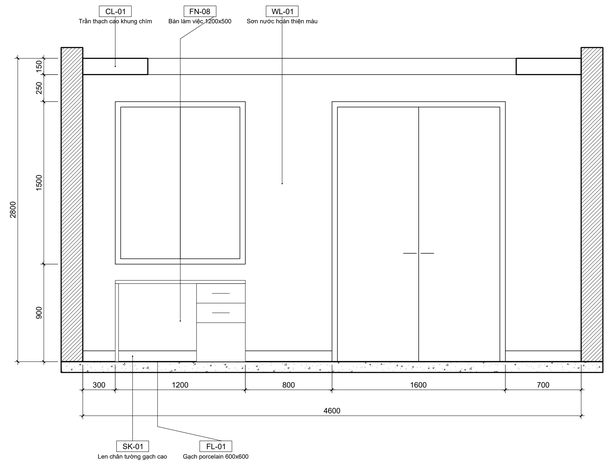

MẶT ĐỨNG C - PHÒNG NGỦ 1

TỶ LỆ: 1/20

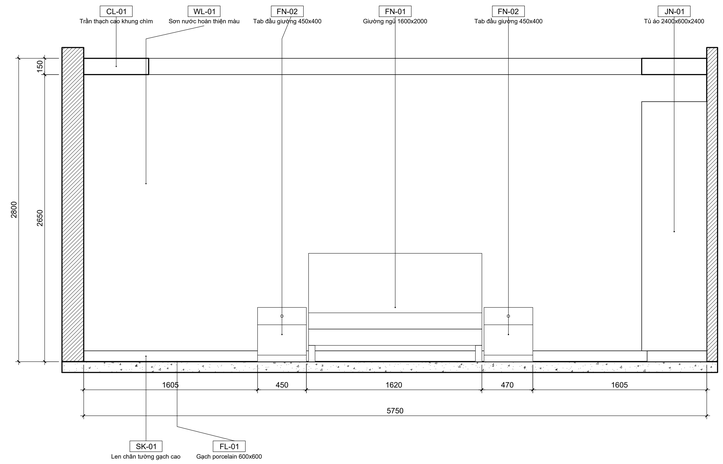

MẶT ĐỨNG D - PHÒNG NGỦ 1

TỶ LỆ: 1/20

GHI CHÚ: NHÀ THẦU THI CÔNG KIỂM TRA KÍCH THƯỚC THỰC TẾ, NẾU THẤY CÓ XUNG ĐỘT CẦN BÁO LẠI CHO THIẾT KẾ VÀ QUẢN LÝ KỸ THUẬT.

CHỦ ĐẦU TƯ - Client:

CHỦ ĐẦU TƯ (MẪU)

DỰ ÁN - Project:

NHÀ PHỐ 5x18m, 3 TẦNG + TUM

Mẫu minh họa

HẠNG MỤC - Item:

NỘI THẤT

TƯ VẤN THIẾT KẾ - Consultant:

AUTOCAD MCP

CHỦ NHIỆM TK - Chief of Project	
CHỦ TRÌ TK - Chief of Division	
THIẾT KẾ - Designed by: AutoCAD MCP	
KIỂM TRA - Checked by	

TÊN BẢN VẼ - Drawing name:

MẶT ĐỨNG NỘI THẤT PHÒNG NGỦ 1 TẦNG 2

SỐ HĐ - Contract No	PHIÊN BẢN - Version: 01
GIAI ĐOẠN - Phase: TKTC	KÝ HIỆU BẢN VẼ - Drawing No: NT-06
TỶ LỆ - Scale: 1:20	HOÀN THÀNH - Finish: 03/11/2026

BẢNG THỐNG KÊ VẬT LIỆU HOÀN THIỆN

MÃ	KÝ HIỆU	HẠNG MỤC	MÔ TẢ	VỊ TRÍ	ĐV	KHỐI LƯỢNG
CL-01		Trần	Trần thạch cao khung chìm, sơn trắng	TẦNG 1: PHÒNG KHÁCH, BẾP + ĂN; TẦNG 2: PHÒNG NGỦ 1, SẢNH, PHÒNG NGỦ 2, KHO; TẦNG 3: PHÒNG NGỦ 3, SẢNH, PHÒNG THỜ	m²	188,75
CL-02		Trần	Trần thạch cao chống ẩm khung chìm, sơn trắng	TẦNG 1: WC; TẦNG 2: WC; TẦNG 3: WC	m²	13,16
EQ-01		Thiết bị	Tủ lạnh 700x700	TẦNG 1: BẾP + ĂN	cái	1
EQ-02		Thiết bị	Máy giặt 600x600	TẦNG 1: SÂN PHƠI; TẦNG 3: SÂN PHƠI	cái	2
EQ-03		Thiết bị	Máy hút mùi 700x480x650	TẦNG 1: BẾP + ĂN	cái	1
FL-01		Sàn	Gạch porcelain 600x600	TẦNG 1: PHÒNG KHÁCH, BẾP + ĂN; TẦNG 2: PHÒNG NGỦ 1, SẢNH, PHÒNG NGỦ 2, KHO; TẦNG 3: PHÒNG NGỦ 3, SẢNH, PHÒNG THỜ	m²	188,75
FL-02		Sàn	Gạch chống trơn 300x300	TẦNG 1: WC; TẦNG 2: WC; TẦNG 3: WC	m²	13,16
FL-03		Sàn	Gạch chống trơn ngoài trời 400x400	TẦNG 1: SÂN PHƠI; TẦNG 3: SÂN PHƠI; TUM: SÂN THƯỢNG	m²	79,74
FL-04		Sàn	Đá granite ốp bậc thang và chiếu nghỉ	TẦNG 1: CẦU THANG; TẦNG 2: CẦU THANG; TẦNG 3: CẦU THANG; TUM: CẦU THANG	m²	34,37
FN-01		Nội thất rời	Giường ngủ 1600x2000	TẦNG 2: PHÒNG NGỦ 1, PHÒNG NGỦ 2; TẦNG 3: PHÒNG NGỦ 3	cái	3
FN-02		Nội thất rời	Tab đầu giường 450x400	TẦNG 2: PHÒNG NGỦ 1, PHÒNG NGỦ 2; TẦNG 3: PHÒNG NGỦ 3	cái	6
FN-03		Nội thất rời	Sofa 2100x850	TẦNG 1: PHÒNG KHÁCH	cái	1
FN-05		Nội thất rời	Bàn trà 1100x600	TẦNG 1: PHÒNG KHÁCH	cái	1
FN-06		Nội thất rời	Bộ bàn ăn 1600x900	TẦNG 1: BẾP + ĂN	cái	1
FN-08		Nội thất rời	Bàn làm việc 1200x500	TẦNG 2: PHÒNG NGỦ 1; TẦNG 3: PHÒNG NGỦ 3	cái	2
JN-01		Đồ gỗ đóng tại chỗ	Tủ áo 2400x600x2400	TẦNG 2: PHÒNG NGỦ 1	cái	1
JN-02		Đồ gỗ đóng tại chỗ	Kệ tivi 1800x400x450	TẦNG 1: PHÒNG KHÁCH	cái	1
JN-03		Đồ gỗ đóng tại chỗ	Tủ bếp dưới 2400x600x850	TẦNG 1: BẾP + ĂN	cái	1
JN-04		Đồ gỗ đóng tại chỗ	Tủ bếp trên 2400x350x700	TẦNG 1: BẾP + ĂN	cái	1
JN-05		Đồ gỗ đóng tại chỗ	Tủ giày 1000x350x1000	TẦNG 1: PHÒNG KHÁCH	cái	1
JN-07		Đồ gỗ đóng tại chỗ	Tủ áo 1800x600x2400	TẦNG 2: PHÒNG NGỦ 2	cái	1
JN-08		Đồ gỗ đóng tại chỗ	Tủ thờ 1530x610x1270	TẦNG 3: PHÒNG THỜ	cái	1
JN-09		Đồ gỗ đóng tại chỗ	Tủ áo 2000x600x2400	TẦNG 3: PHÒNG NGỦ 3	cái	1
JN-10		Đồ gỗ đóng tại chỗ	Kệ sách 1200x300x2000	TẦNG 1: PHÒNG KHÁCH	cái	1
LT-01		Đèn	Đèn downlight âm trần Ø90	TẦNG 1; TẦNG 2; TẦNG 3	cái	132
LT-02		Đèn	Đèn LED dây hắt trần	TẦNG 1; TẦNG 2; TẦNG 3	m	122,38
LT-03		Đèn	Đèn ốp trần	TẦNG 1; TẦNG 2; TẦNG 3	cái	7
LT-04		Đèn	Đèn thả	TẦNG 1	cái	1
SK-01		Len chân tường	Len chân tường gạch cao 100	TẦNG 1: PHÒNG KHÁCH, BẾP + ĂN, SÂN PHƠI; TẦNG 2: PHÒNG NGỦ 1, SẢNH, PHÒNG NGỦ 2, KHO; TẦNG 3: PHÒNG NGỦ 3, SẢNH, PHÒNG THỜ; SÂN PHƠI; TUM: SÂN THƯỢNG	m	216
SK-02		Len chân tường	Len đá granite cao 100 theo bậc	TẦNG 1: CẦU THANG; TẦNG 2: CẦU THANG; TẦNG 3: CẦU THANG; TUM: CẦU THANG	m	44,95
SN-01		Thiết bị vệ sinh	Bồn cầu 400x700	TẦNG 1: WC; TẦNG 2: WC; TẦNG 3: WC	cái	3
SN-02		Thiết bị vệ sinh	Lavabo, tủ chậu, gương 800x500	TẦNG 1: WC; TẦNG 2: WC; TẦNG 3: WC	cái	3
SN-03		Thiết bị vệ sinh	Khu tắm đứng, vách kính 900x900	TẦNG 2: WC	cái	1
WL-01		Tường hoàn thiện	Sơn nước hoàn thiện màu trắng	TẦNG 1: PHÒNG KHÁCH, CẦU THANG, BẾP + ĂN; TẦNG 2: PHÒNG NGỦ 1, SẢNH, CẦU THANG, PHÒNG NGỦ 2, KHO; TẦNG 3: PHÒNG NGỦ 3, SẢNH, CẦU THANG, PHÒNG THỜ; TUM: CẦU THANG	m²	558,86
WL-02		Tường hoàn thiện	Gạch ốp tường 300x600 ốp đến trần	TẦNG 1: WC; TẦNG 2: WC; TẦNG 3: WC	m²	65,94
WL-03		Tường hoàn thiện	Gạch ốp tường bếp 600x300	TẦNG 1: BẾP + ĂN	m²	1,56
WL-04		Tường hoàn thiện	Sơn ngoại thất màu trắng	TẦNG 1: SÂN PHƠI; TẦNG 3: SÂN PHƠI; TUM: SÂN THƯỢNG	m²	188,72

GHI CHÚ: NHÀ THẦU THI CÔNG KIỂM TRA KÍCH THƯỚC THỰC TẾ. NẾU THẤY CÓ XUNG ĐỘT CẦN BÁO LẠI CHO THIẾT KẾ VÀ QUẢN LÝ KỸ THUẬT.

LẦN NỘP	NỘI DUNG ĐIỀU CHỈNH	NGÀY NỘP
1		
2		
3		
4		

GHI CHÚ - Note:

CHỦ ĐẦU TƯ - Client:
CHỦ ĐẦU TƯ (MẪU)

DỰ ÁN - Project:
NHÀ PHỐ 5x18m, 3 TẦNG + TUM

Mẫu minh họa

HẠNG MỤC - Item:
NỘI THẤT

TƯ VẤN THIẾT KẾ - Consultant:
AUTOCAD MCP

CHỦ NHIỆM TK - Chief of Project	
CHỦ TRÌ TK - Chief of Division	
THIẾT KẾ - Designed by: AutoCAD MCP	
KIỂM TRA - Checked by	

TÊN BẢN VẼ - Drawing name:
BẢNG THỐNG KÊ VẬT LIỆU HOÀN THIỆN

SỐ HĐ - Contract No.	PHIÊN BẢN - Version: 01
GIAI ĐOẠN - Phase: TKTC	KÝ HIỆU BẢN VẼ - Drawing No.: NT-07
TỶ LỆ - Scale: 1:50	HOÀN THÀNH - Finish: 03/11/2026