
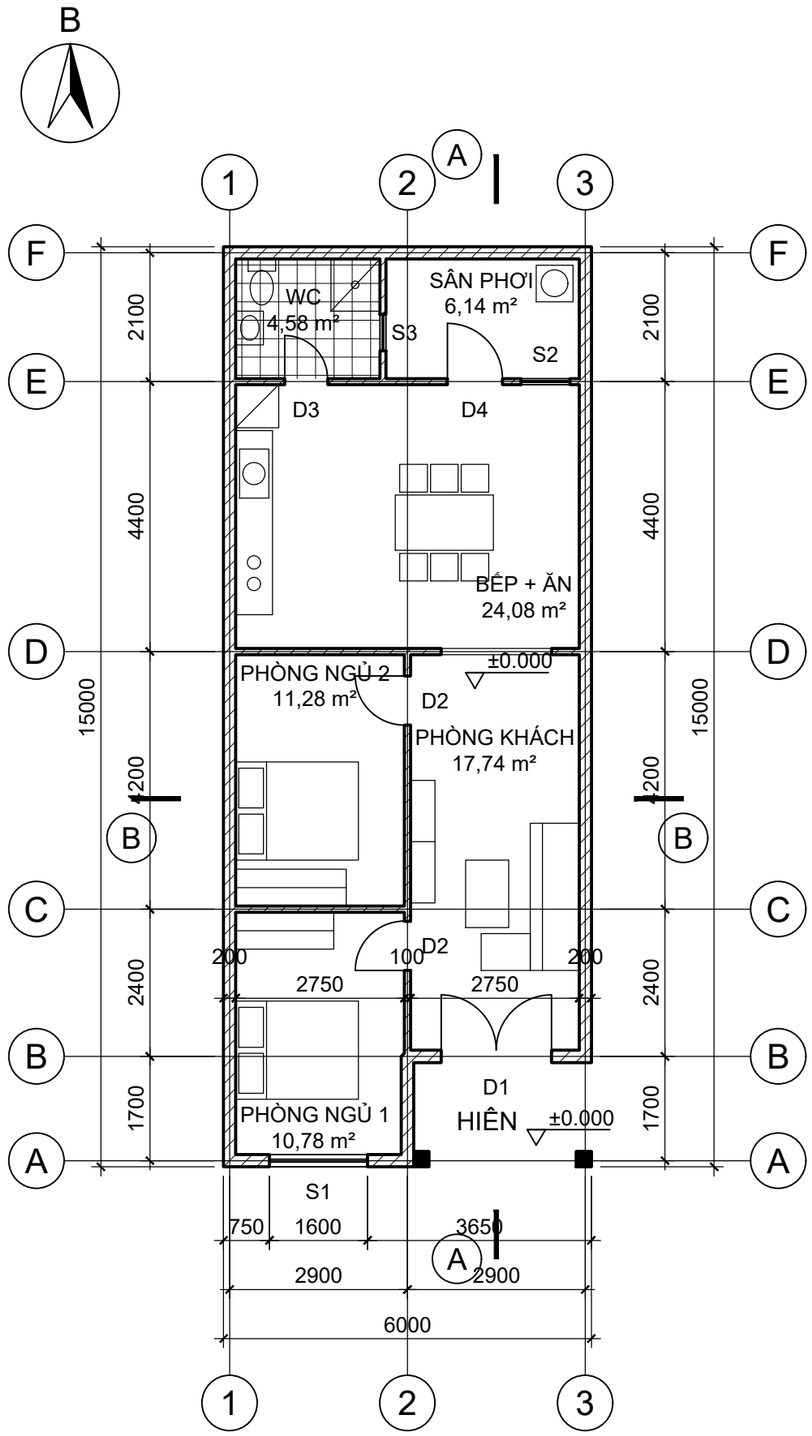


MẶT BẰNG TẦNG 1


TỶ LỆ 1:100

CÔNG TRÌNH: NHÀ Ở 1 TẦNG 6x15m			
TÊN BẢN VẼ: MẶT BẰNG TẦNG 1			
TỶ LỆ: 1:100	NGÀY: 2026-11-02	THIẾT KẾ: AutoCAD MCP	KIỂM TRA:
SỐ BẢN VẼ: KT-01	LẦN SỬA:	TỜ: 1/6	

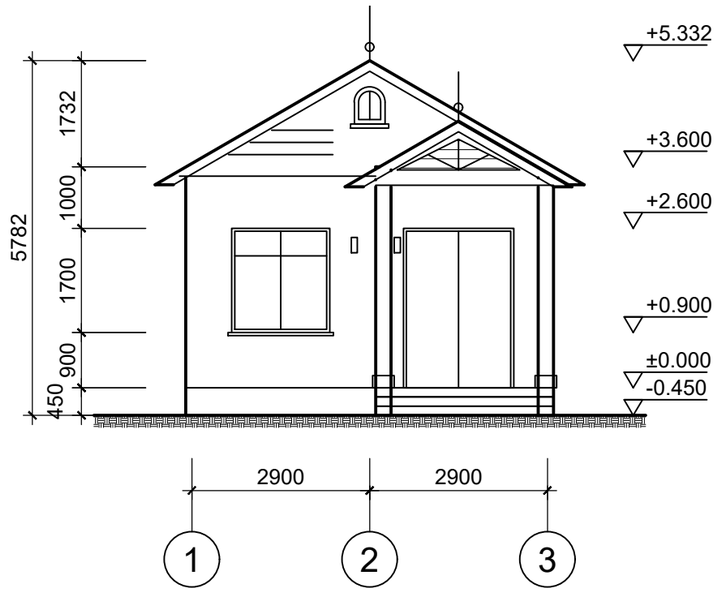

MẶT ĐỨNG CHÍNH (TRỤC 1-3)


TỶ LỆ 1:100

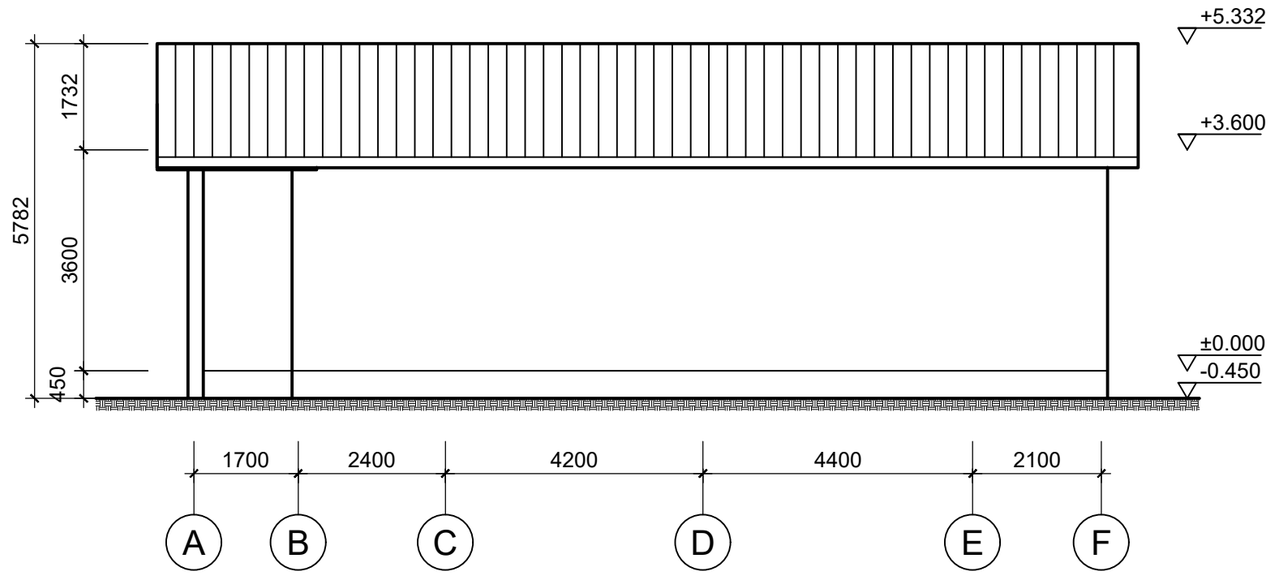

MẶT ĐỨNG TRỤC A-F


TỶ LỆ 1:100

CÔNG TRÌNH: NHÀ Ở 1 TẦNG 6x15m			
TÊN BẢN VẼ: MẶT ĐỨNG TRỤC 1-3, A-F			
TỶ LỆ: 1:100	NGÀY: 2026-11-02	THIẾT KẾ: AutoCAD MCP	KIỂM TRA:
SỐ BẢN VẼ: KT-02		LẦN SỬA:	TỜ: 2/6

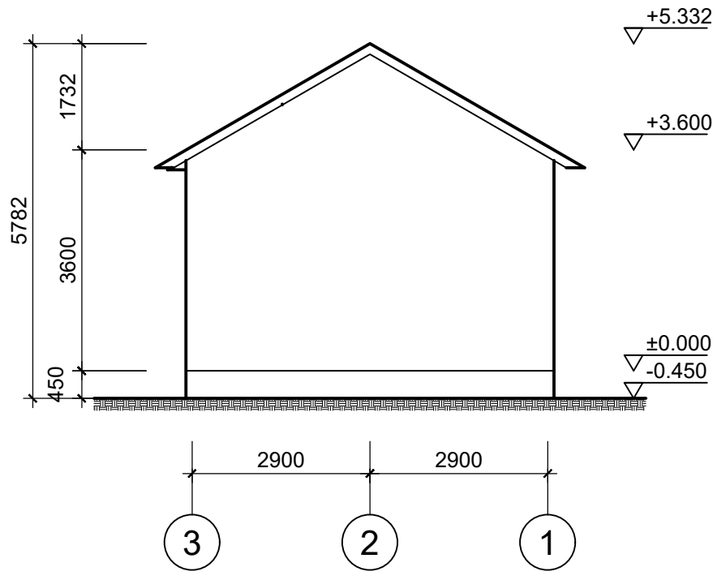

MẶT ĐỨNG TRỤC 3-1


TỶ LỆ 1:100

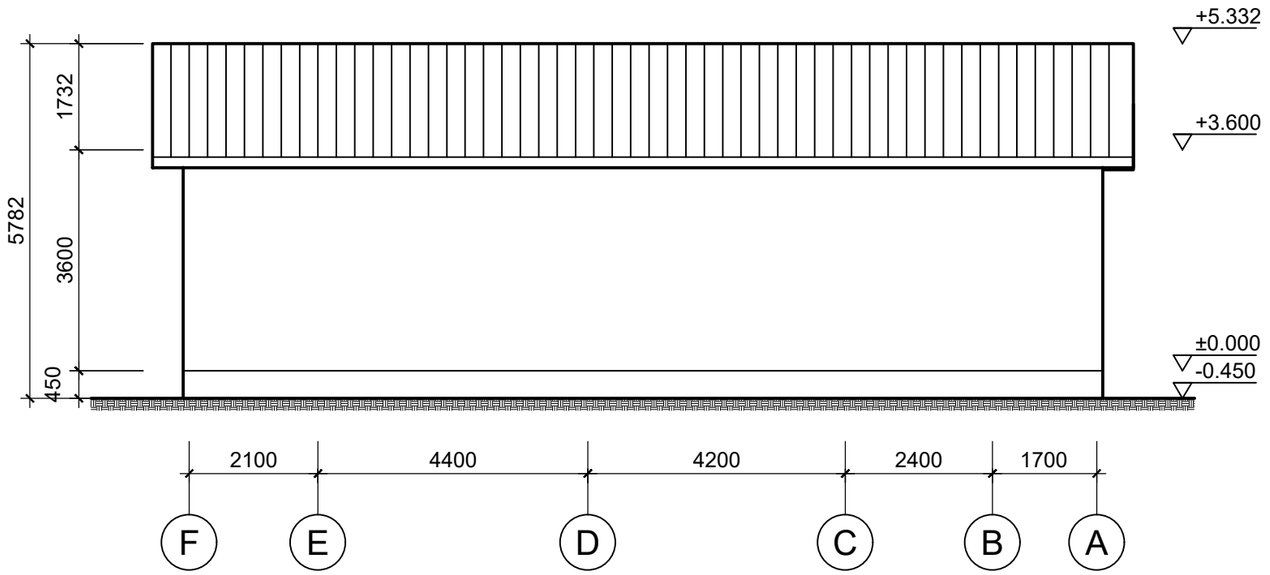

MẶT ĐỨNG TRỤC F-A


TỶ LỆ 1:100

CÔNG TRÌNH: NHÀ Ở 1 TẦNG 6x15m			
TÊN BẢN VẼ: MẶT ĐỨNG TRỤC 3-1, F-A			
TỶ LỆ: 1:100	NGÀY: 2026-11-02	THIẾT KẾ: AutoCAD MCP	KIỂM TRA:
SỐ BẢN VẼ: KT-03		LẦN SỬA:	TỜ: 3/6

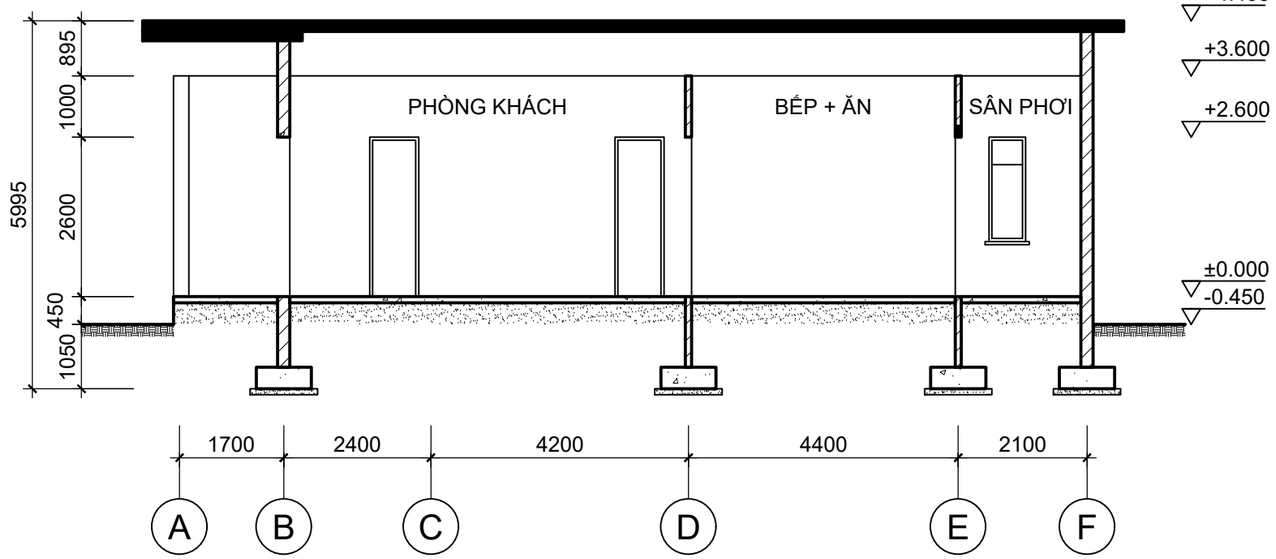

MẶT CẮT A-A


TỶ LỆ 1:100

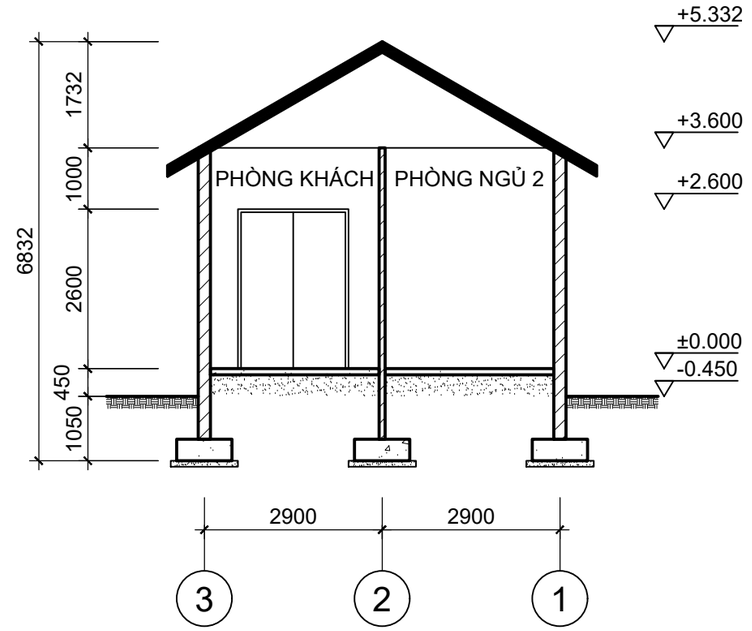


MẶT CẮT B-B

TỶ LỆ 1:100


CÔNG TRÌNH: NHÀ Ở 1 TẦNG 6x15m			
TÊN BẢN VẼ: MẶT CẮT A-A, B-B			
TỶ LỆ: 1:100	NGÀY: 2026-11-02	THIẾT KẾ: AutoCAD MCP	KIỂM TRA:
SỐ BẢN VẼ: KT-04		LẦN SỬA:	TỜ: 4/6

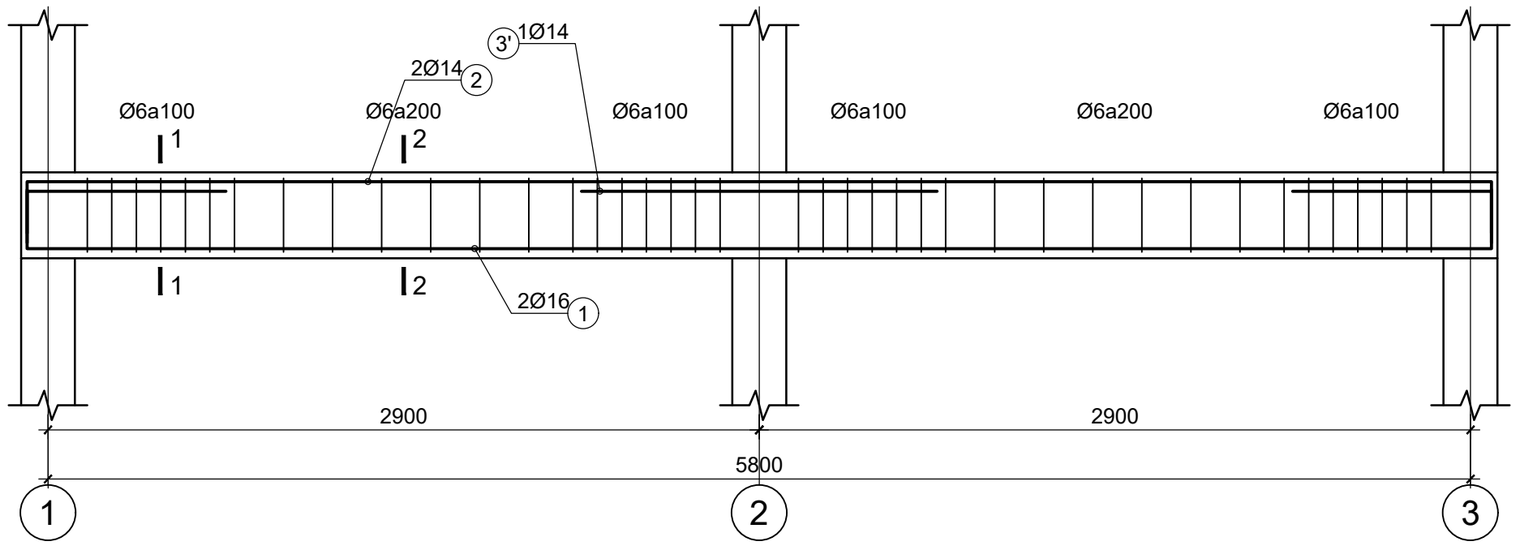

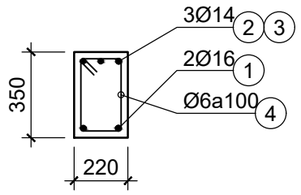


MẶT CẮT 1-1

TỶ LỆ 1:25

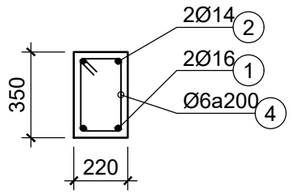

MẶT CẮT 2-2

TỶ LỆ 1:25

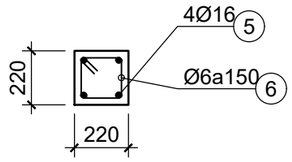


MẶT CẮT C1 (220x220)

TỶ LỆ 1:25

DẦM D1 TRỤC C (220x350)

TỶ LỆ 1:25

CÔNG TRÌNH: NHÀ Ở 1 TẦNG 6x15m			
TÊN BẢN VẼ: CHI TIẾT DẦM D1, CỘT C1			
TỶ LỆ: 1:25	NGÀY: 2026-11-02	THIẾT KẾ: AutoCAD MCP	KIỂM TRA:
SỐ BẢN VẼ: KC-01		LẦN SỬA:	TỜ: 5/6

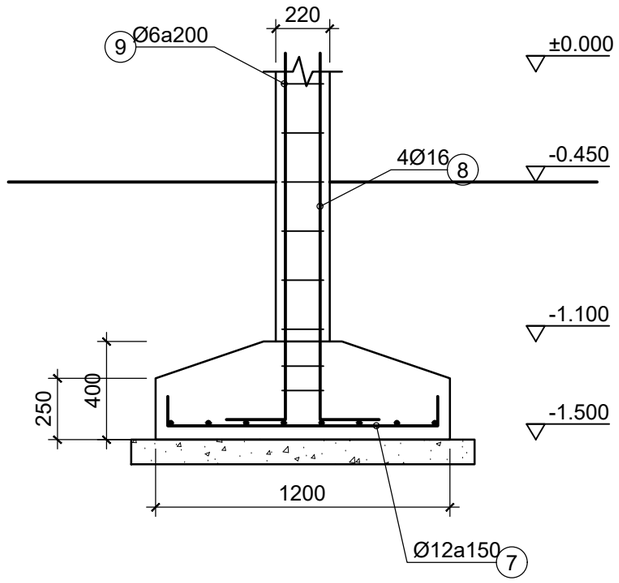

MÓNG M1 (1200x1200)

TỶ LỆ 1:25

BẢNG THỐNG KÊ CỐT THÉP								
SỐ HIỆU	HÌNH DẠNG	Ø (mm)	DÀI 1 THANH (mm)	SỐ THANH/CK	SỐ CK	TỔNG SỐ THANH	TỔNG DÀI (m)	KHỐI LƯỢNG (kg)
1	U	16	6450	2	3	6	38.7	61.16
2	U	14	6390	2	3	6	38.34	46.39
3	L	14	1020	2	3	6	6.12	7.4
3'	—	14	1450	1	3	3	4.35	5.26
4	đai	6	1090	40	3	120	130.8	29.07
7	U	12	1340	8	6	48	64.32	57.17
7'	U	12	1340	8	6	48	64.32	57.17
8	L	16	1733	4	6	24	41.59	65.73
9	đai	6	830	8	6	48	39.84	8.85
Ø6								37.92
Ø12								114.34
Ø14								59.05
Ø16								126.89
TỔNG CỘNG								338.2

CÔNG TRÌNH

NHÀ Ở 1 TẦNG 6x15m

TÊN BẢN VẼ

MÓNG M1, THỐNG KÊ THÉP

TỶ LỆ	NGÀY	THIẾT KẾ	KIỂM TRA
1:25	2026-11-02	AutoCAD MCP	

SỐ BẢN VẼ	LẦN SỬA	TỜ
KC-02		6/6