
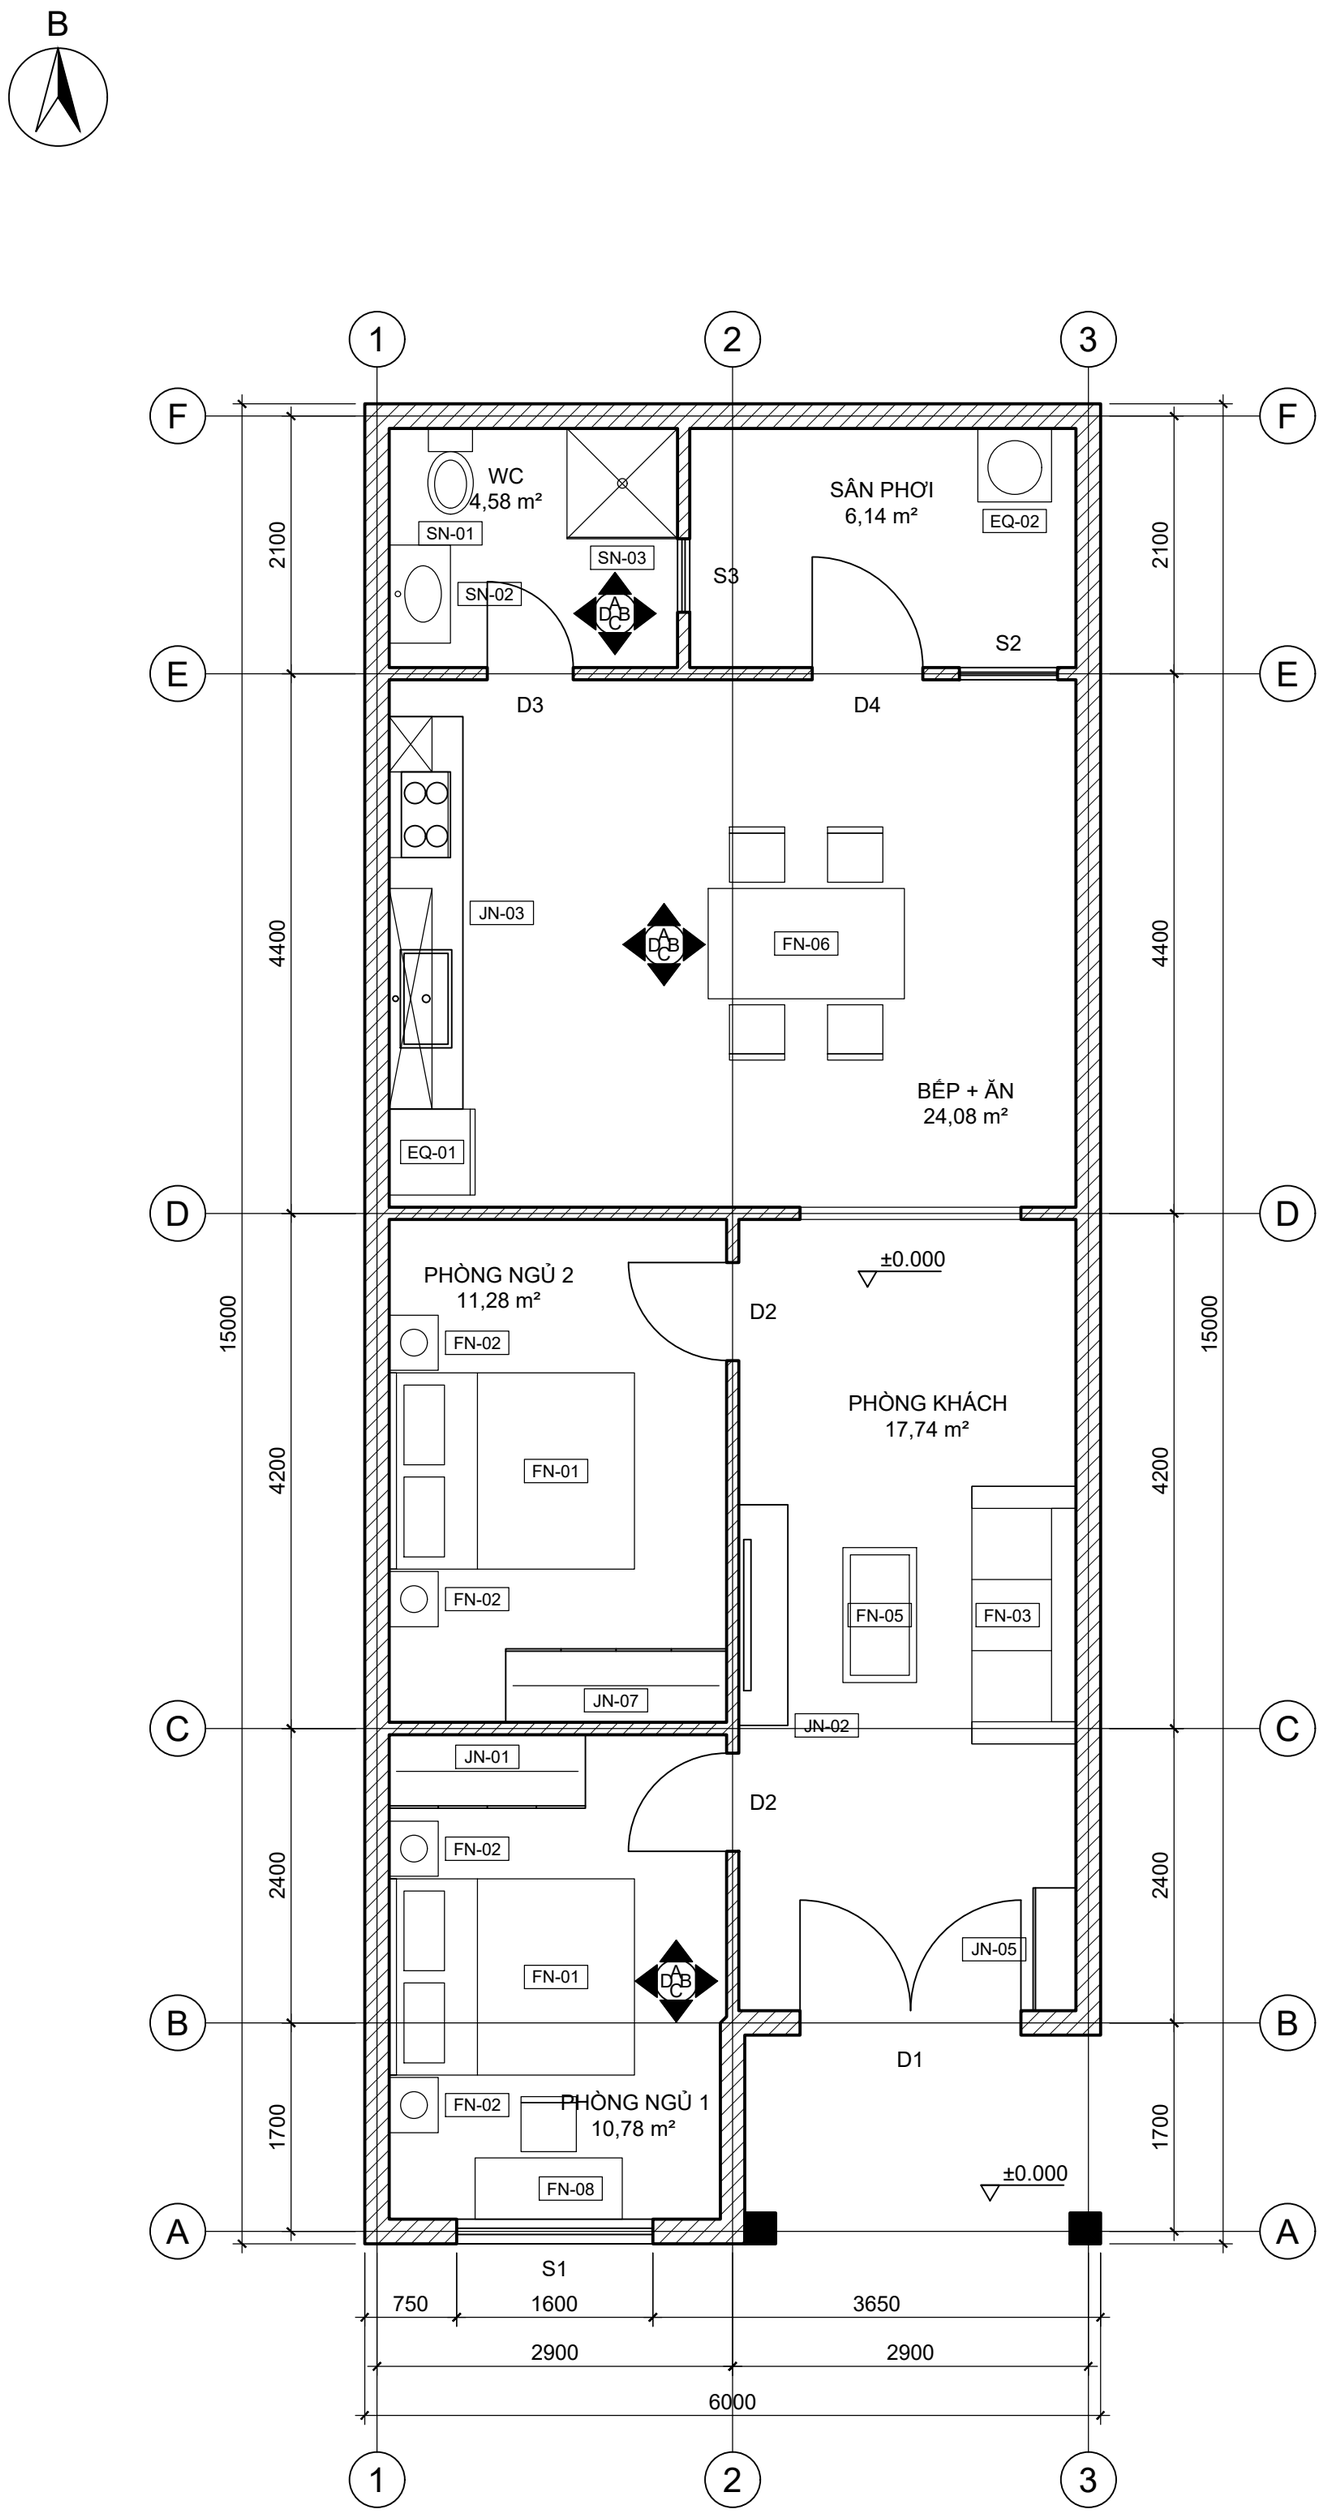


MẶT BẰNG BỐ TRÍ NỘI THẤT

TỶ LỆ 1:50

CÔNG TRÌNH: NHÀ Ở 1 TẦNG 6x15m			
TÊN BẢN VẼ: MẶT BẰNG BỐ TRÍ NỘI THẤT			
TỶ LỆ: 1:50	NGÀY: 2026-11-02	THIẾT KẾ: AutoCAD MCP	KIỂM TRA:
SỐ BẢN VẼ: NT-01		LẦN SỬA:	TỜ: 1/10

B

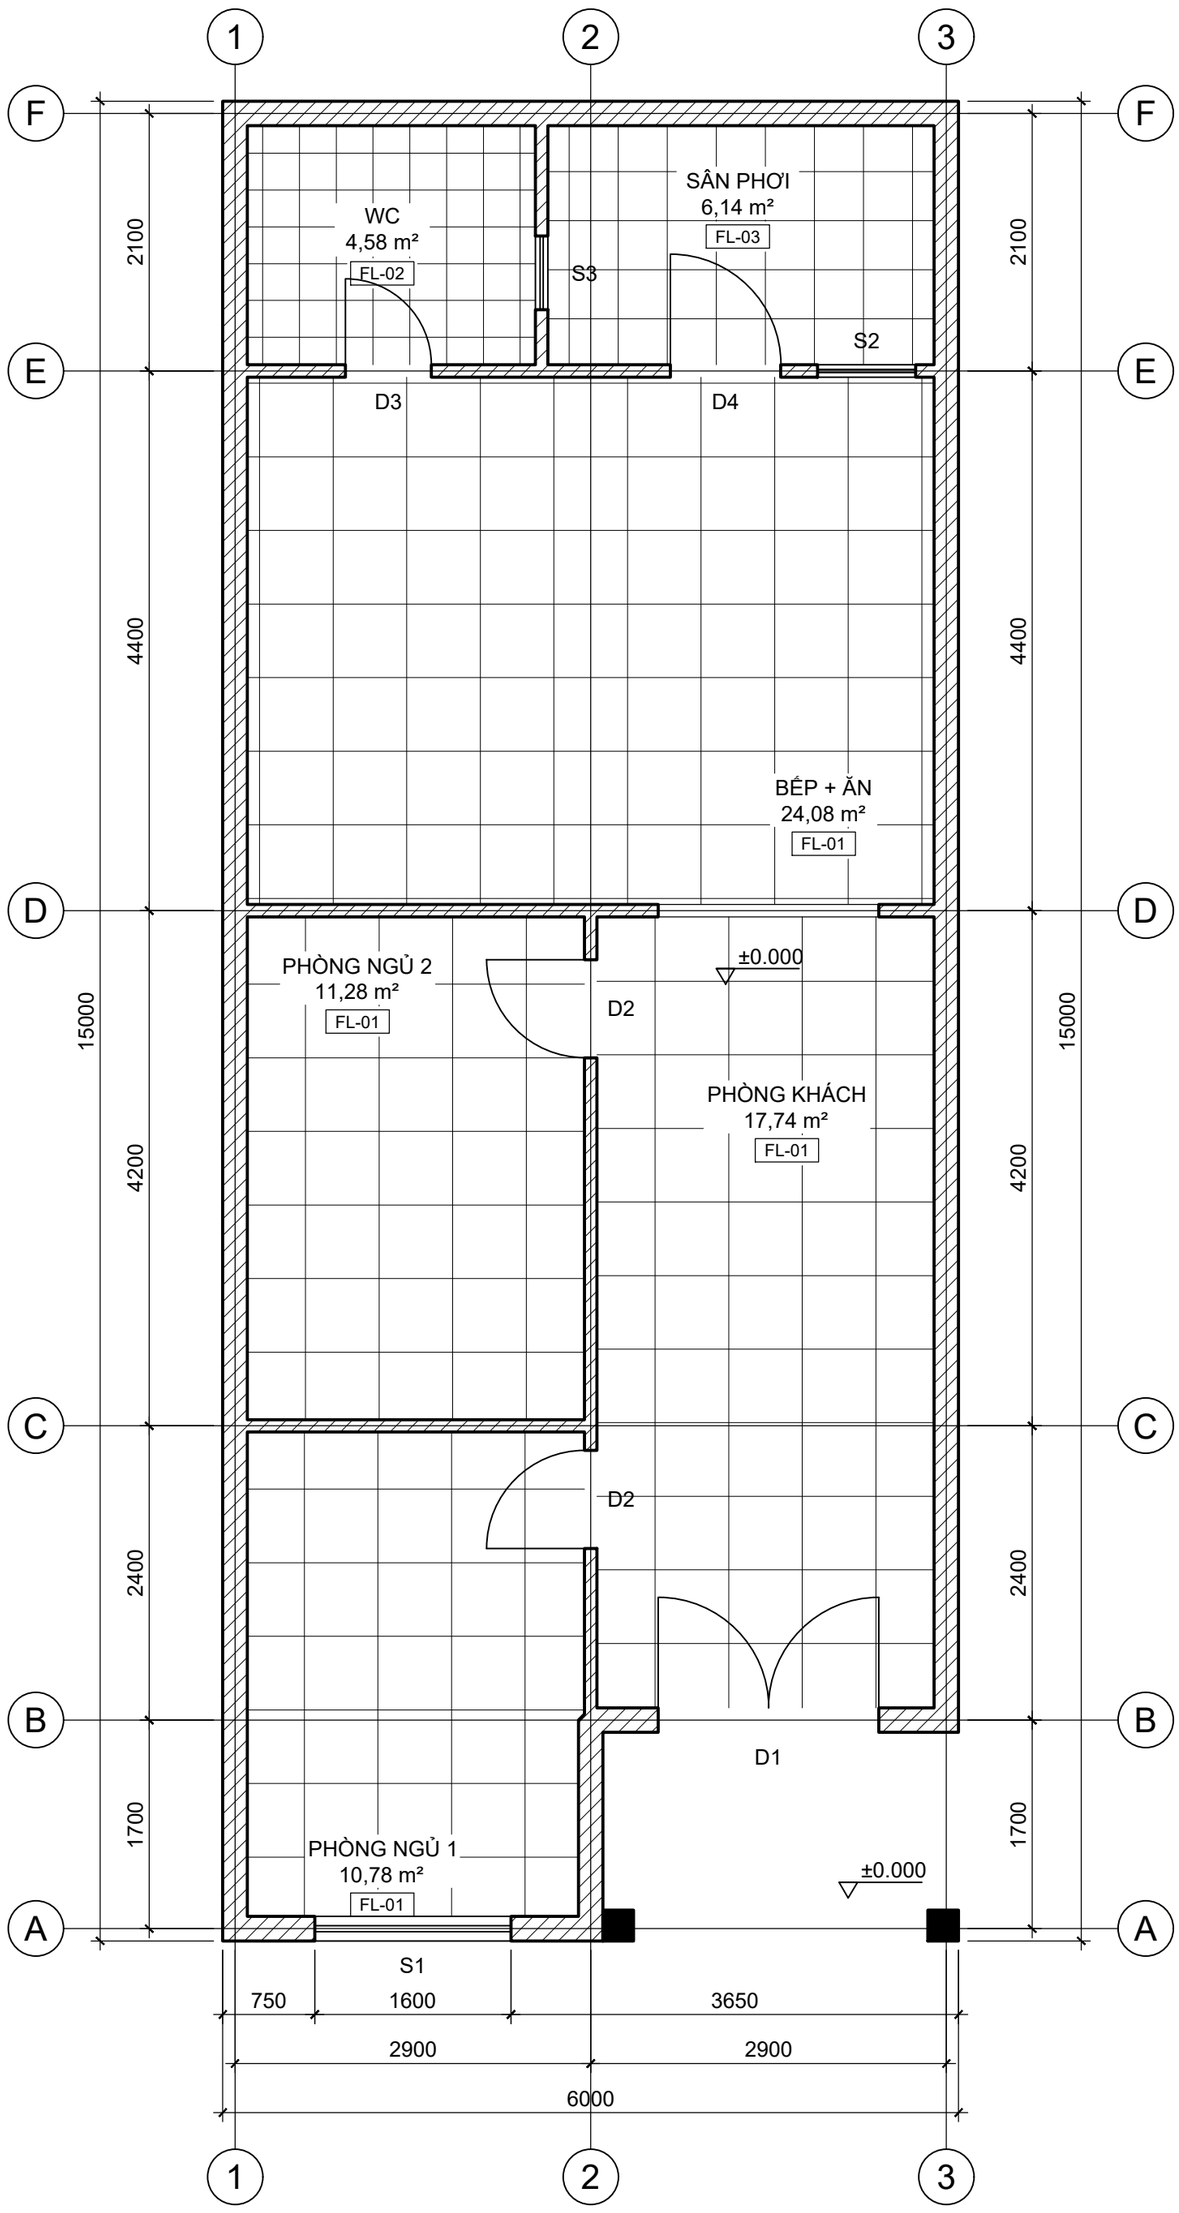

MẶT BẰNG LÁT SÀN

TỶ LỆ 1:50

CHÚ THÍCH VẬT LIỆU SÀN

FL-01 Gạch porcelain 600x600
63,87 m² (PHÒNG NGỦ 1, PHÒNG NGỦ 2, PHÒNG KHÁCH, BẾP + ĂN)

FL-02 Gạch chống trơn 300x300
4,58 m² (WC)

FL-03 Gạch chống trơn ngoài trời 400x400
6,14 m² (SÂN PHƠI)

CÔNG TRÌNH: NHÀ Ở 1 TẦNG 6x15m			
TÊN BẢN VẼ: MẶT BẰNG LÁT SÀN			
TỶ LỆ: 1:50	NGÀY: 2026-11-02	THIẾT KẾ: AutoCAD MCP	KIỂM TRA:
SỐ BẢN VẼ: NT-02	LẦN SỬA:	TỜ: 2/10	

B


KÝ HIỆU ĐÈN

LT-01 Đèn downlight âm trần Ø90: 52 cái

LT-03 Đèn ốp trần: 3 cái

LT-04 Đèn thả: 1 cái


LT-02 Đèn LED dây hắt trần: 43,5 m

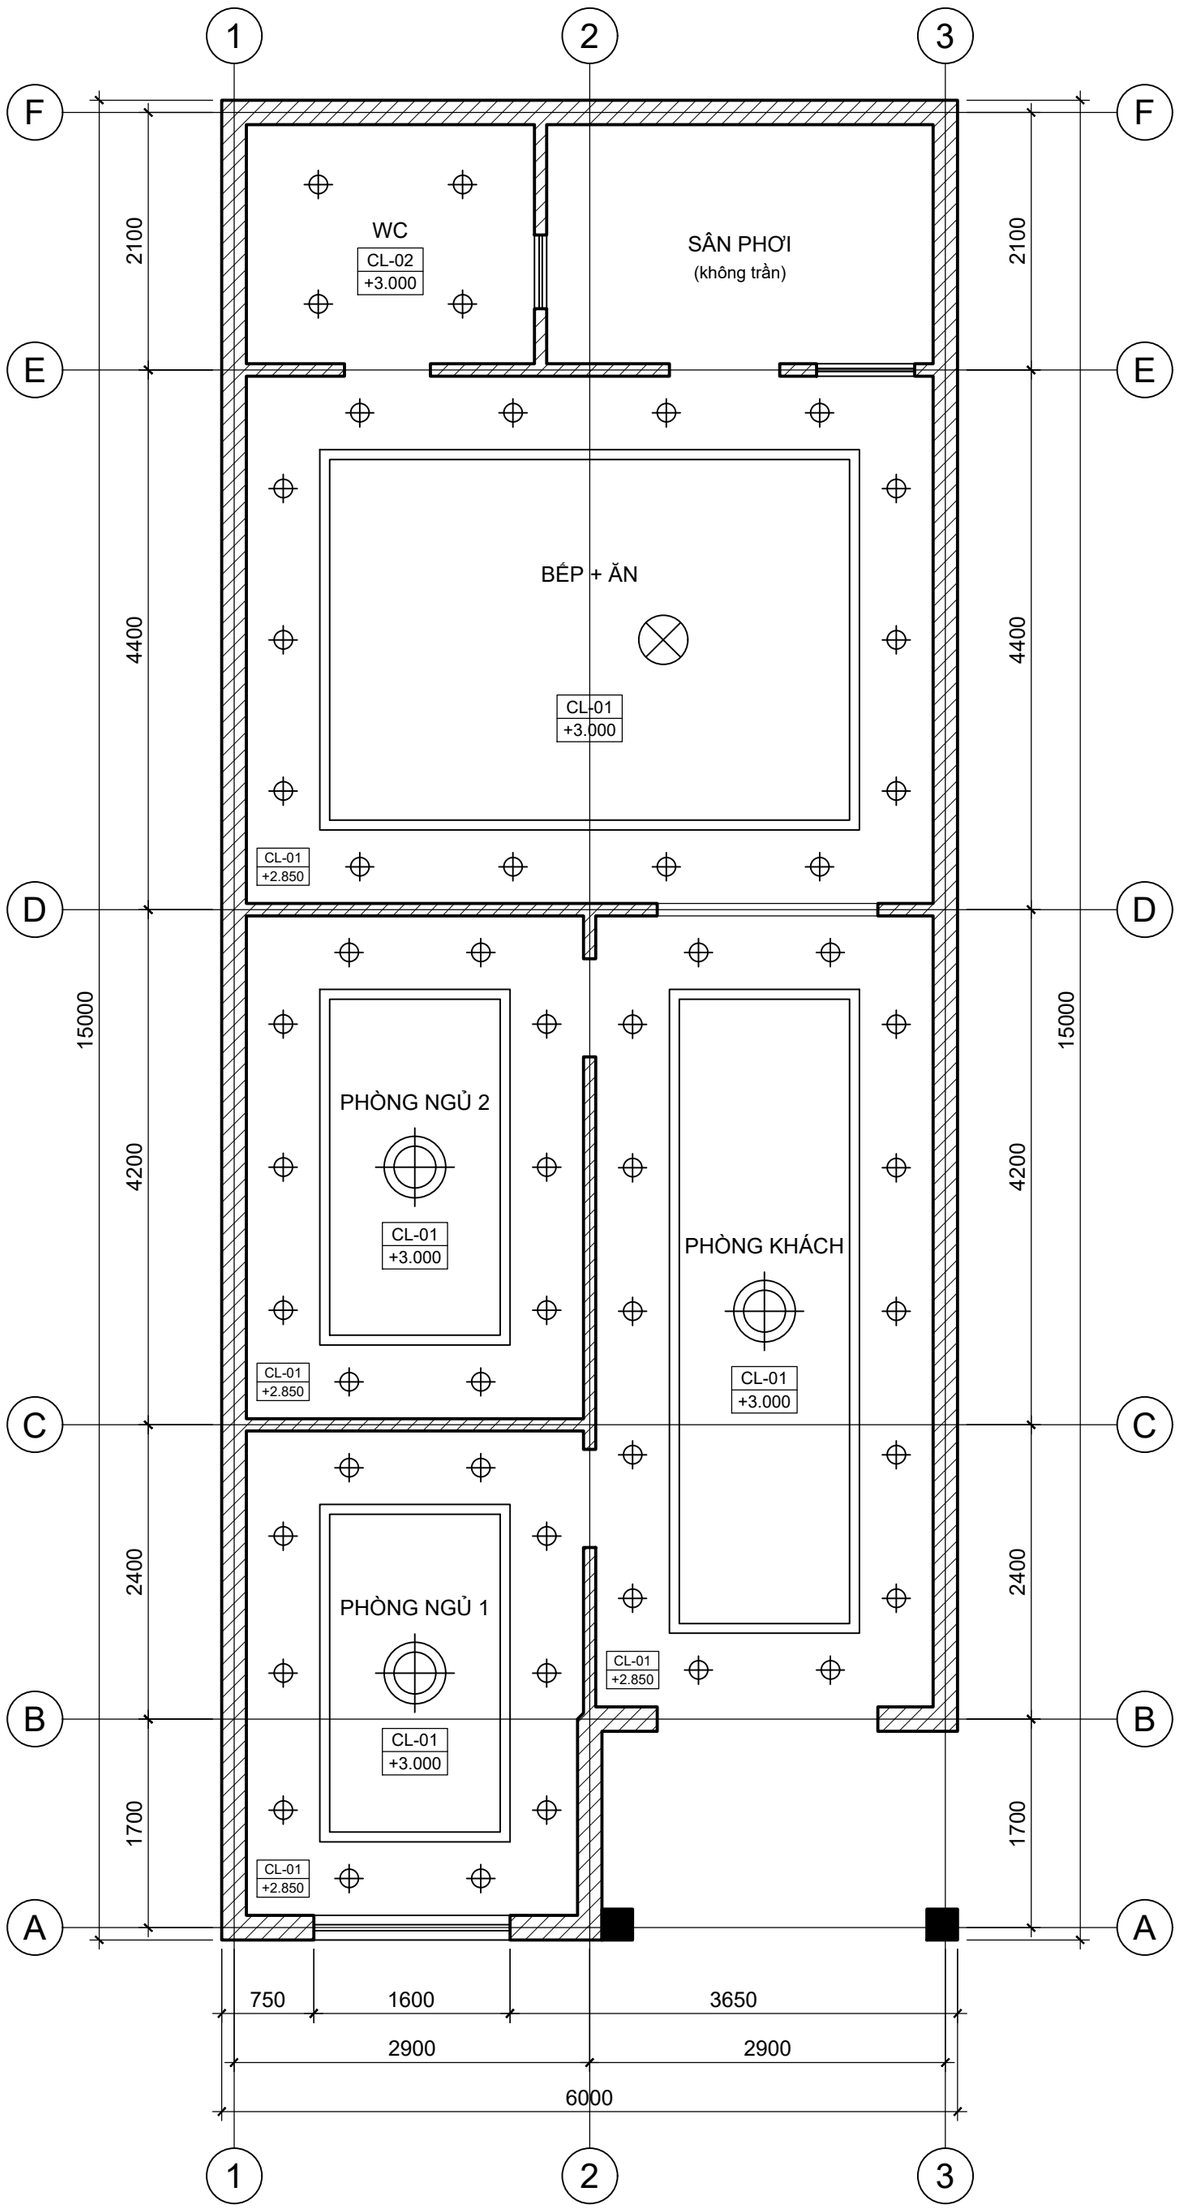

MẶT BẰNG TRẦN ĐÈN


TỶ LỆ 1:50

CÔNG TRÌNH: NHÀ Ở 1 TẦNG 6x15m			
TÊN BẢN VẼ: MẶT BẰNG TRẦN ĐÈN			
TỶ LỆ: 1:50	NGÀY: 2026-11-02	THIẾT KẾ: AutoCAD MCP	KIỂM TRA:
SỐ BẢN VẼ: NT-03	LẦN SỬA:	TỜ: 3/10	

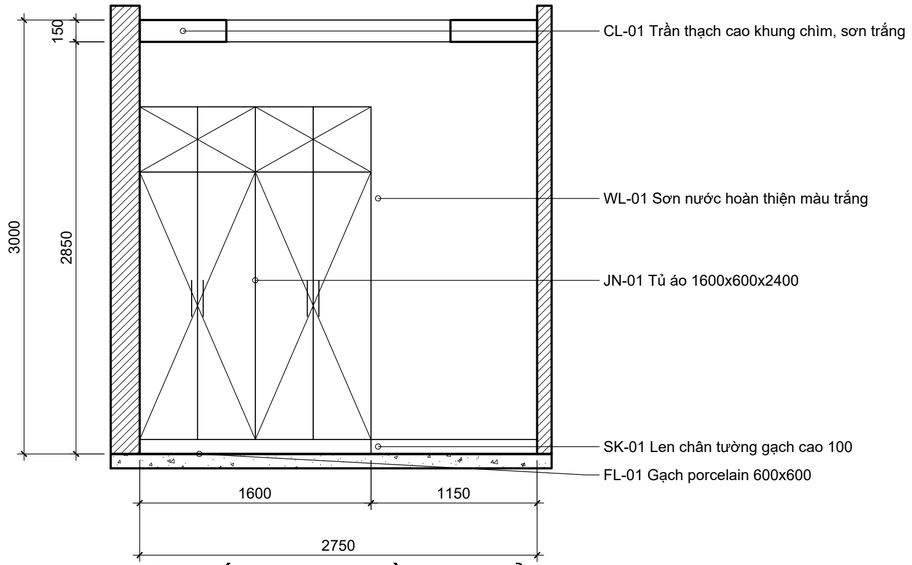

MẶT ĐỨNG A - PHÒNG NGỦ 1

TỶ LỆ 1:30

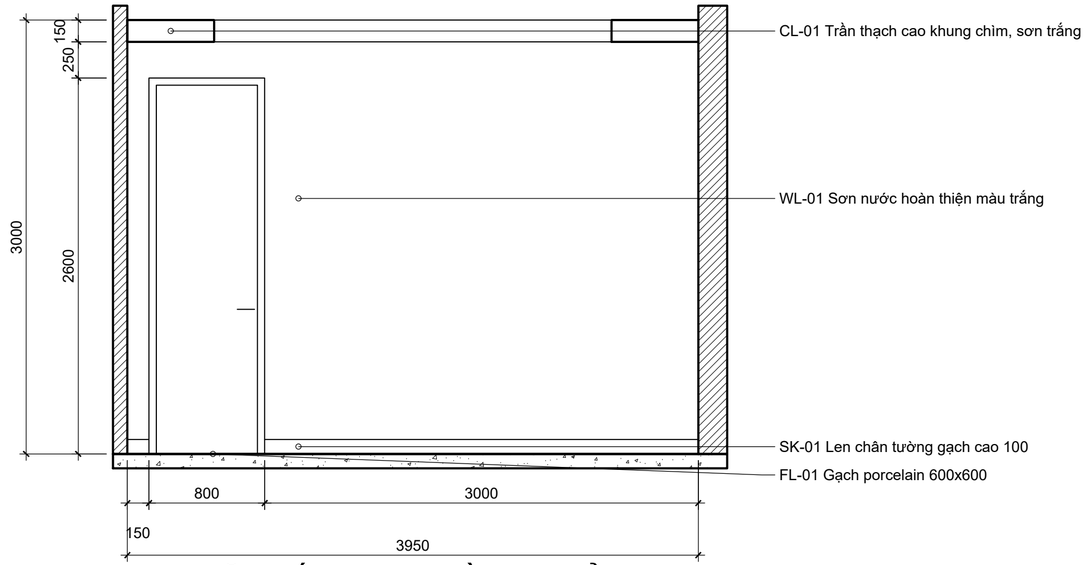

MẶT ĐỨNG B - PHÒNG NGỦ 1


TỶ LỆ 1:30

CÔNG TRÌNH
NHÀ Ở 1 TẦNG 6x15m

TÊN BẢN VẼ
MẶT ĐỨNG NỘI THẤT PHÒNG NGỦ 1 (A, B)


TỶ LỆ	NGÀY	THIẾT KẾ	KIỂM TRA
1:30	2026-11-02	AutoCAD MCP	

SỐ BẢN VẼ	LẦN SỬA	TỜ
NT-04		4/10

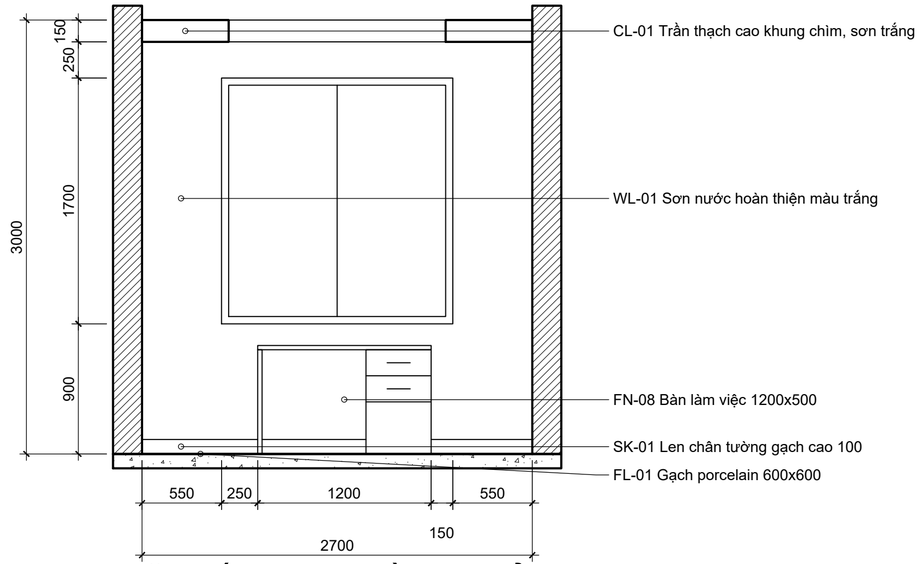

MẶT ĐỨNG C - PHÒNG NGỦ 1


TỶ LỆ 1:30

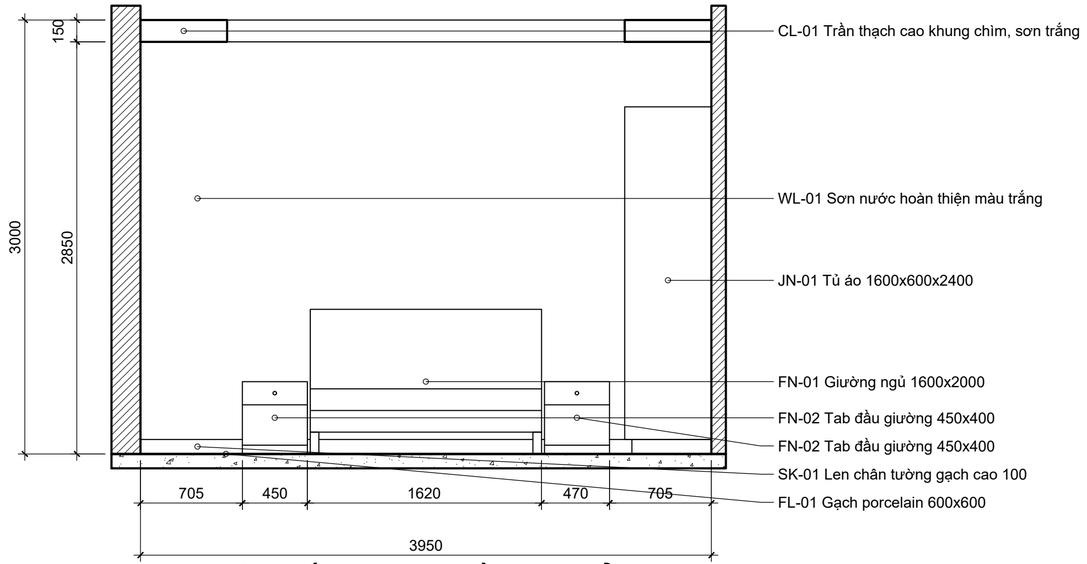

MẶT ĐỨNG D - PHÒNG NGỦ 1

TỶ LỆ 1:30


CÔNG TRÌNH: NHÀ Ở 1 TẦNG 6x15m			
TÊN BẢN VẼ: MẶT ĐỨNG NỘI THẤT PHÒNG NGỦ 1 (C, D)			
TỶ LỆ: 1:30	NGÀY: 2026-11-02	THIẾT KẾ: AutoCAD MCP	KIỂM TRA:
SỐ BẢN VẼ: NT-05	LẦN SỬA:	TỜ: 5/10	

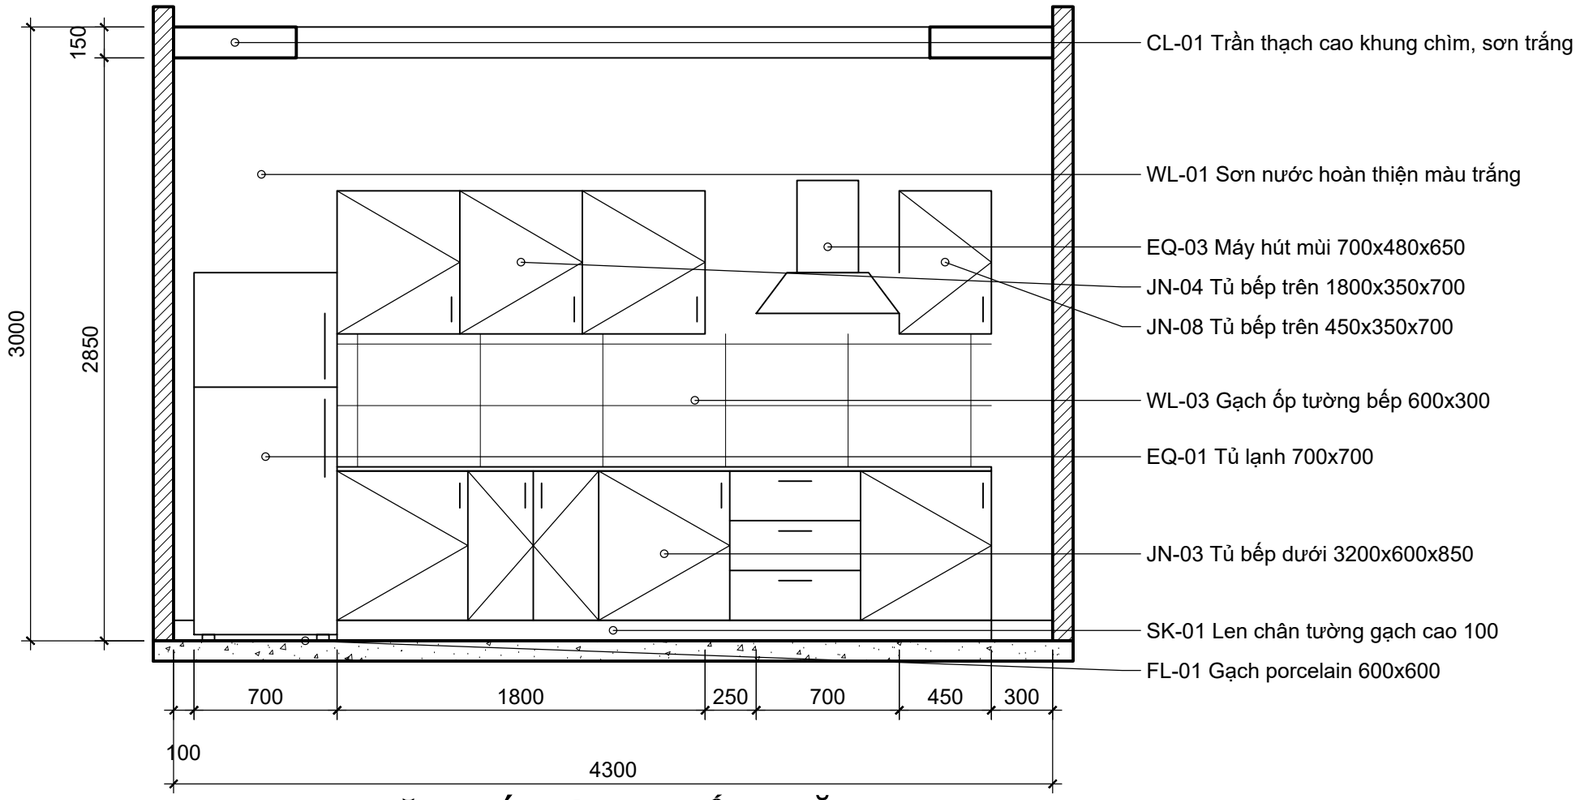

MẶT ĐỨNG D - BẾP + ĂN


TỶ LỆ 1:30

CÔNG TRÌNH: NHÀ Ở 1 TẦNG 6x15m			
TÊN BẢN VẼ: MẶT ĐỨNG NỘI THẤT BẾP (D)			
TỶ LỆ: 1:30	NGÀY: 2026-11-02	THIẾT KẾ: AutoCAD MCP	KIỂM TRA:
SỐ BẢN VẼ: NT-06	LẦN SỬA:	TỜ: 6/10	

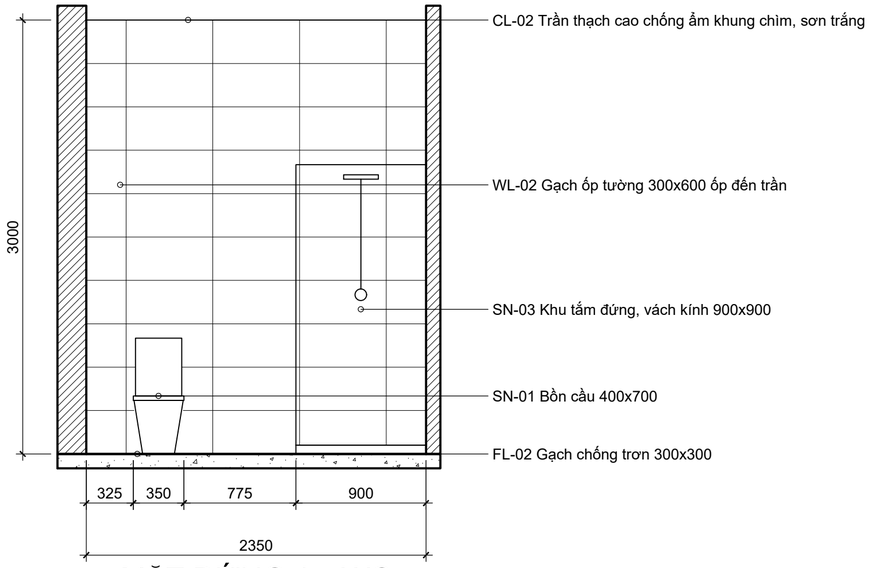

MẶT ĐỨNG A - WC

TỶ LỆ 1:30

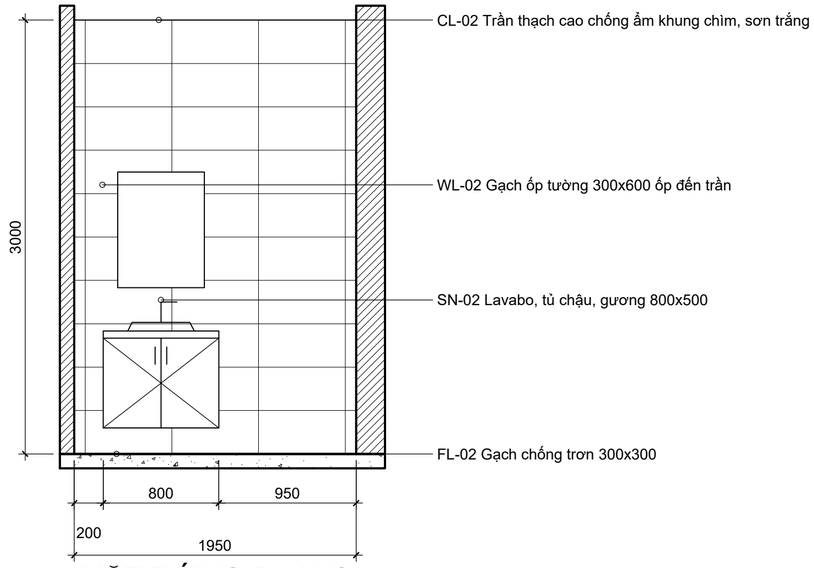

MẶT ĐỨNG D - WC

TỶ LỆ 1:30

CÔNG TRÌNH


NHÀ Ở 1 TẦNG 6x15m

TÊN BẢN VẼ

MẶT ĐỨNG NỘI THẤT WC (A, D)


TỶ LỆ	NGÀY	THIẾT KẾ	KIỂM TRA
1:30	2026-11-02	AutoCAD MCP	

SỐ BẢN VẼ	LẦN SỬA	TỜ
NT-07		7/10

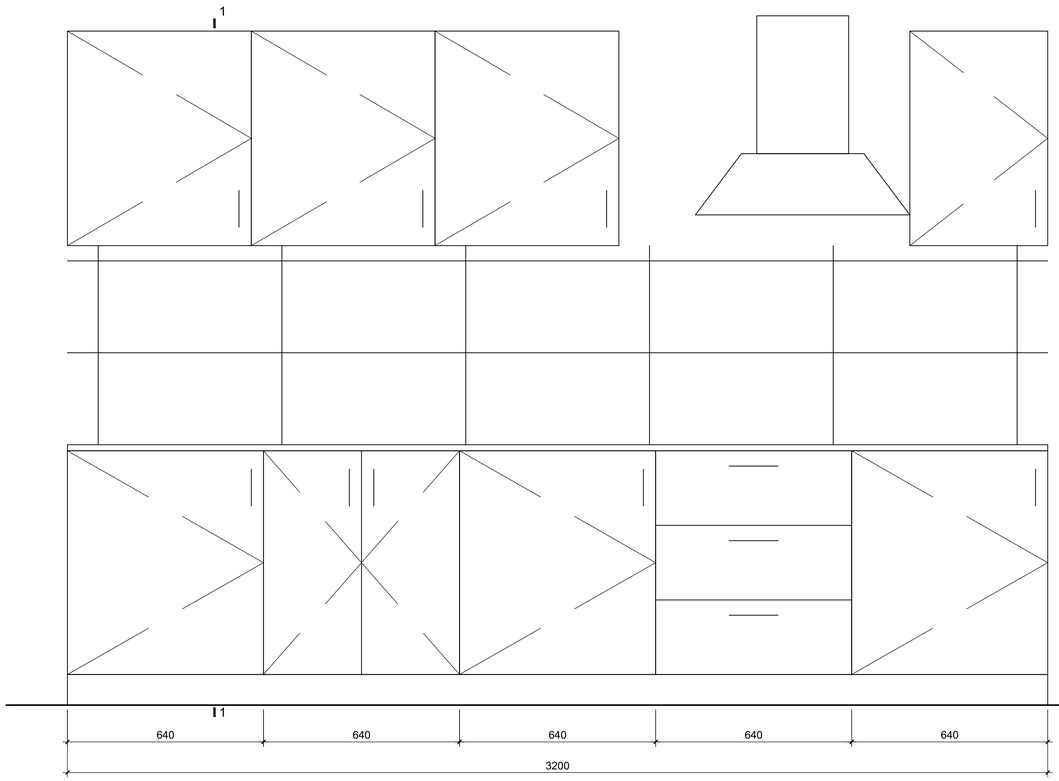

MẶT ĐỨNG TỦ BẾP JN-03


TỶ LỆ 1:10

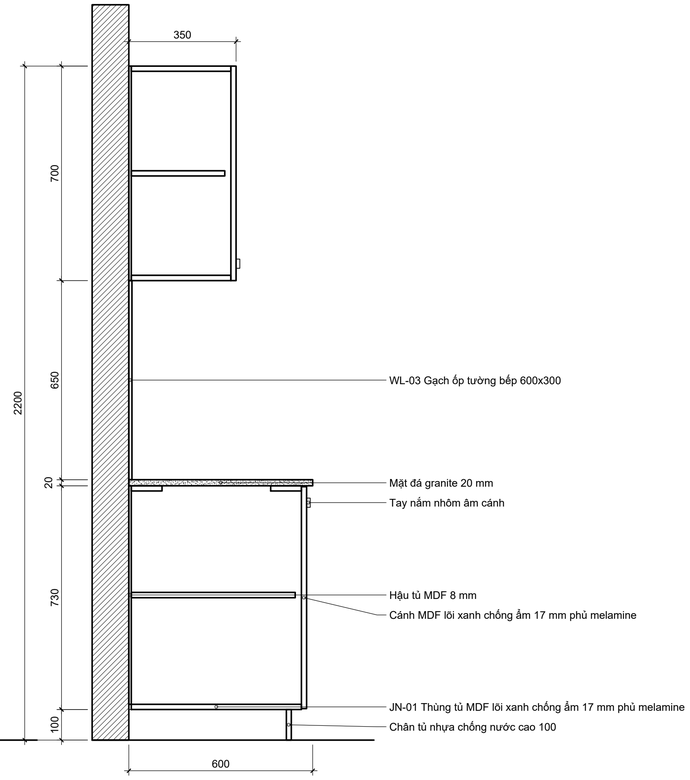

MẶT CẮT 1-1


TỶ LỆ 1:10

CÔNG TRÌNH: NHÀ Ở 1 TẦNG 6x15m			
TÊN BẢN VẼ: CHI TIẾT TỦ BẾP JN-03			
TỶ LỆ: 1:10	NGÀY: 2026-11-02	THIẾT KẾ: AutoCAD MCP	KIỂM TRA:
SỐ BẢN VẼ: NT-08	LẦN SỬA:	TỜ: 8/10	

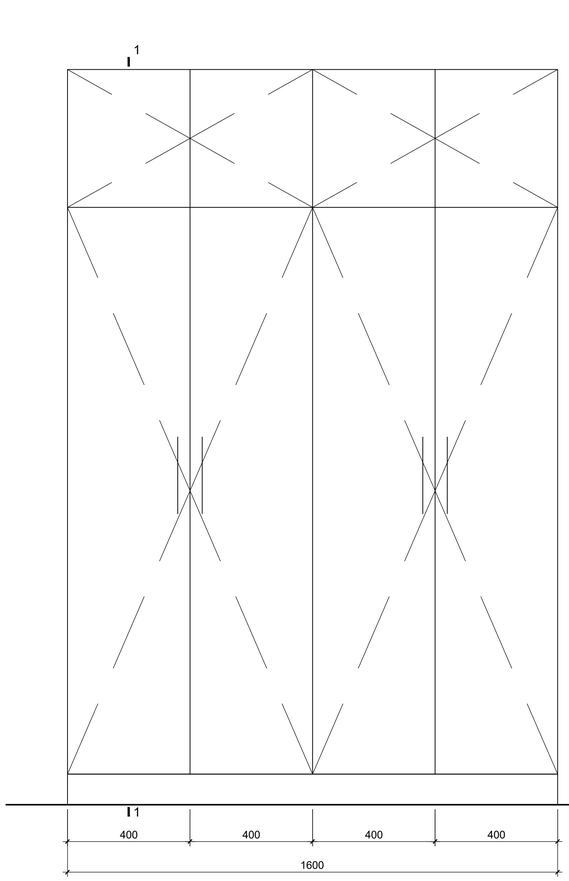

MẶT ĐỨNG TỦ ÁO JN-01

TỶ LỆ 1:10

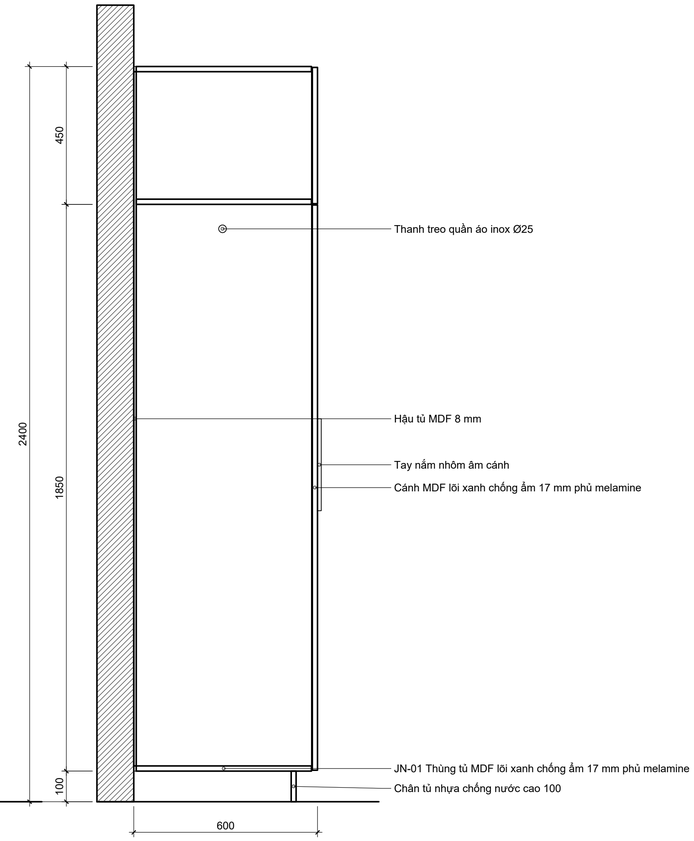

MẶT CẮT 1-1

TỶ LỆ 1:10

CÔNG TRÌNH: NHÀ Ở 1 TẦNG 6x15m			
TÊN BẢN VẼ: CHI TIẾT TỦ ÁO JN-01			
TỶ LỆ: 1:10	NGÀY: 2026-11-02	THIẾT KẾ: AutoCAD MCP	KIỂM TRA:
SỐ BẢN VẼ: NT-09	LẦN SỬA:	TỜ: 9/10	

BẢNG THỐNG KÊ VẬT LIỆU HOÀN THIỆN

MÃ	HẠNG MỤC	MÔ TẢ	VỊ TRÍ	ĐV	KHỐI LƯỢNG
CL-01	Trần	Trần thạch cao khung chìm, sơn trắng	PHÒNG NGỦ 1, PHÒNG NGỦ 2, PHÒNG KHÁCH, BẾP + ĂN	m²	63.87
CL-02	Trần	Trần thạch cao chống ẩm khung chìm, sơn trắng	WC	m²	4.58
EQ-01	Thiết bị	Tủ lạnh 700x700	BẾP + ĂN	cái	1
EQ-02	Thiết bị	Máy giặt 600x600	SÂN PHƠI	cái	1
EQ-03	Thiết bị	Máy hút mùi 700x480x650	BẾP + ĂN	cái	1
FL-01	Sàn	Gạch porcelain 600x600	PHÒNG NGỦ 1, PHÒNG NGỦ 2, PHÒNG KHÁCH, BẾP + ĂN	m²	63.87
FL-02	Sàn	Gạch chống trơn 300x300	WC	m²	4.58
FL-03	Sàn	Gạch chống trơn ngoài trời 400x400	SÂN PHƠI	m²	6.14
FN-01	Nội thất rời	Giường ngủ 1600x2000	PHÒNG NGỦ 1, PHÒNG NGỦ 2	cái	2
FN-02	Nội thất rời	Tab đầu giường 450x400	PHÒNG NGỦ 1, PHÒNG NGỦ 2	cái	4
FN-03	Nội thất rời	Sofa 2100x850	PHÒNG KHÁCH	cái	1
FN-05	Nội thất rời	Bàn trà 1100x600	PHÒNG KHÁCH	cái	1
FN-06	Nội thất rời	Bộ bàn ăn 1600x900	BẾP + ĂN	cái	1
FN-08	Nội thất rời	Bàn làm việc 1200x500	PHÒNG NGỦ 1	cái	1
JN-01	Đồ gỗ đóng tại chỗ	Tủ áo 1600x600x2400	PHÒNG NGỦ 1	cái	1
JN-02	Đồ gỗ đóng tại chỗ	Kệ tivi 1800x400x450	PHÒNG KHÁCH	cái	1
JN-03	Đồ gỗ đóng tại chỗ	Tủ bếp dưới 3200x600x850	BẾP + ĂN	cái	1
JN-04	Đồ gỗ đóng tại chỗ	Tủ bếp trên 1800x350x700	BẾP + ĂN	cái	1
JN-05	Đồ gỗ đóng tại chỗ	Tủ giày 1000x350x1000	PHÒNG KHÁCH	cái	1
JN-07	Đồ gỗ đóng tại chỗ	Tủ áo 1800x600x2400	PHÒNG NGỦ 2	cái	1
JN-08	Đồ gỗ đóng tại chỗ	Tủ bếp trên 450x350x700	BẾP + ĂN	cái	1
LT-01	Đèn	Đèn downlight âm trần Ø90		cái	52
LT-02	Đèn	Đèn LED dây hắt trần		m	43.54
LT-03	Đèn	Đèn ốp trần		cái	3
LT-04	Đèn	Đèn thả		cái	1
SK-01	Len chân tường	Len chân tường gạch cao 100	PHÒNG NGỦ 1, PHÒNG NGỦ 2, PHÒNG KHÁCH, BẾP + ĂN, SÂN PHƠI	m	64.37
SN-01	Thiết bị vệ sinh	Bồn cầu 400x700	WC	cái	1
SN-02	Thiết bị vệ sinh	Lavabo, tủ chậu, gương 800x500	WC	cái	1
SN-03	Thiết bị vệ sinh	Khu tắm đứng, vách kính 900x900	WC	cái	1
WL-01	Tường hoàn thiện	Sơn nước hoàn thiện màu trắng	PHÒNG NGỦ 1, PHÒNG NGỦ 2, PHÒNG KHÁCH, BẾP + ĂN	m²	153.34
WL-02	Tường hoàn thiện	Gạch ốp tường 300x600 ốp đến trần	WC	m²	22.96
WL-03	Tường hoàn thiện	Gạch ốp tường bếp 600x300	BẾP + ĂN	m²	2.08
WL-04	Tường hoàn thiện	Sơn ngoại thất màu trắng	SÂN PHƠI	m²	32

CÔNG TRÌNH
NHÀ Ở 1 TẦNG 6x15m

TÊN BẢN VẼ
BẢNG THỐNG KÊ VẬT LIỆU HOÀN THIỆN

TỶ LỆ	NGÀY	THIẾT KẾ	KIỂM TRA
1:50	2026-11-02	AutoCAD MCP	

SỐ BẢN VẼ	LẦN SỬA	TỜ
NT-10		10/10