DANH MỤC BẢN VẼ - KẾT CẤU

STT	KÝ HIỆU	TÊN BẢN VẼ	TỶ LỆ	KHỔ GIẤY	GHI CHÚ
1	KC-00	DANH MỤC BẢN VẼ KẾT CẤU	1:50	A3 ngang	
2	KC-01	GHI CHÚ CHUNG KẾT CẤU	1:50	A2 ngang	
3	KC-02	MẶT BẰNG KẾT CẤU SÀN TẦNG 2	1:100	A3 đứng	
4	KC-03	MẶT BẰNG KẾT CẤU SÀN TẦNG 3	1:100	A3 đứng	
5	KC-04	MẶT BẰNG KẾT CẤU SÀN TUM	1:100	A3 đứng	
6	KC-05	MẶT BẰNG KẾT CẤU SÀN MÁI	1:100	A3 ngang	
7	KC-06	BẢNG MẶT CẮT DẦM	1:25	A2 ngang	

GHI CHÚ:NHÀ THẦU THI CÔNG KIỂM TRA KÍCH THƯỚC THỰC TẾ, NẾU THẤY CÓ XUNG ĐỘT CẦN BÁO LẠI CHO THIẾT KẾ VÀ QUẢN LÝ KỸ THUẬT.

LẦN NỘP	NỘI DUNG ĐIỀU CHỈNH	NGÀY NỘP
1		
2		
3		
4		

GHI CHÚ - Note:

CHỦ ĐẦU TƯ - Client:

CHỦ ĐẦU TƯ (MẪU)

DỰ ÁN - Project:

NHÀ PHỐ 5x18m, 3 TẦNG + TUM

Mẫu minh họa

HẠNG MỤC - Item:

KẾT CẤU

TƯ VẤN THIẾT KẾ - Consultant:

AUTOCAD MCP

CHỦ NHIỆM TK - Chief of Project	
CHỦ TRÌ TK - Chief of Division	
THIẾT KẾ - Designed by AutoCAD MCP	
KIỂM TRA - Checked by ...	

TÊN BẢN VẼ - Drawing name:

DANH MỤC BẢN VẼ KẾT CẤU

SỐ HĐ - Contract No:	PHIÊN BẢN - Version 01
GIAI ĐOẠN - Phase: TKTC	KÝ HIỆU BẢN VẼ - Drawing No KC-00
TỶ LỆ - Scale: 1:50	HOÀN THÀNH - Finish: 03/11/2026

GHI CHÚ CHUNG KẾT CẤU

VẬT LIỆU		
CẤU KIỆN	VẬT LIỆU	GHI CHÚ
Móng, dầm móng, cột, dầm, sàn, cầu thang	Bê tông B20 (M250)	Đổ tại chỗ, đầm kỹ, bảo dưỡng ẩm ≥ 7 ngày
Lanh tô, bổ trụ, giằng tường	Bê tông B15 (M200)	
Bê tông lót móng	Bê tông B7,5 (M100)	Dày 100
Thép Ø < 10	CB240-T	TCVN 1651-1:2018
Thép Ø ≥ 10	CB300-V	TCVN 1651-2:2018

LỚP BÊ TÔNG BẢO VỆ (mm)	
CẤU KIỆN	a (mm)
Móng (có bê tông lót)	40
Dầm móng	30
Cột	25
Dầm	25
Sàn, cầu thang	20
Lanh tô, bổ trụ	15

CHIỀU DÀI NEO VÀ NỐI CHỒNG (mm)				
Ø	NEO KÉO 30d	NEO NÉN 20d	NỐI KÉO 40d	NỐI NÉN 30d
Ø10	300	200	400	300
Ø12	400	250	500	400
Ø14	450	300	600	450
Ø16	500	350	650	500
Ø18	550	400	750	550
Ø20	600	400	800	600
Ø22	700	450	900	700
Ø25	750	500	1000	750

LANH TÔ ĐIỂN HÌNH					
NHỊP Ô CỬA	TIẾT DIỆN	THÉP DƯỚI	THÉP TRÊN	ĐAI	GỐI (mm)
L ≤ 1200	220x150	2Ø10	2Ø10	Ø6a200	200
1200 < L ≤ 2000	220x200	2Ø12	2Ø10	Ø6a200	250
2000 < L ≤ 3000	220x300	2Ø14	2Ø12	Ø6a150	300
L > 3000	Theo thiết kế dầm				

GHI CHÚ:

1. Kích thước ghi bằng mm, cao độ ghi bằng m; cao độ ±0.000 là cao độ sàn hoàn thiện tầng 1.
2. Thiết kế theo TCVN 2737:2023 (tải trọng và tác động), TCVN 5574:2018 (kết cấu bê tông cốt thép).
3. Mối nối thép bố trí so le, không nối quá 50% số thanh tại một tiết diện; không nối thép chịu kéo tại vùng mô men lớn.
4. Cốp pha dầm, sàn chỉ tháo khi bê tông đạt ≥ 70% cường độ (nhịp ≤ 8 m) và ≥ 90% với công xôn.
5. Kích thước dầm, cột trên bản vẽ là sơ bộ theo nhịp: kỹ sư kết cấu tính toán, xác nhận trước khi thi công.
6. Nhà thầu kiểm tra kích thước thực tế, phối hợp bản vẽ kiến trúc, điện, nước trước khi thi công.

GHI CHÚ:NHÀ THẦU THI CÔNG KIỂM TRA KÍCH THƯỚC THỰC TẾ, NẾU THẤY CÓ XUNG ĐỘT CẦN BÁO LẠI CHO THIẾT KẾ VÀ QUẢN LÝ KỸ THUẬT.

LẦN NỘP	NỘI DUNG ĐIỀU CHỈNH	NGÀY NỘP
1		
2		
3		
4		

GHI CHÚ - Note:

CHỦ ĐẦU TƯ - Client:
CHỦ ĐẦU TƯ (MẪU)

DỰ ÁN - Project:
NHÀ PHỐ 5x18m, 3 TẦNG + TUM
Mẫu minh họa


HẠNG MỤC - Item:
KẾT CẤU

TƯ VẤN THIẾT KẾ - Consultant:
AUTOCAD MCP

CHỦ NHIỆM TK - Chief of Project	
CHỦ TRÌ TK - Chief of Division	
THIẾT KẾ - Designed by AutoCAD MCP	
KIỂM TRA - Checked by ...	

TÊN BẢN VẼ - Drawing name:
GHI CHÚ CHUNG KẾT CẤU


SỐ HĐ - Contract No:	PHIÊN BẢN - Version 01
GIAI ĐOẠN - Phase: TKTC	KÝ HIỆU BẢN VẼ - Drawing No: KC-01
TỶ LỆ - Scale: 1:50	HOÀN THÀNH - Finish: 03/11/2026

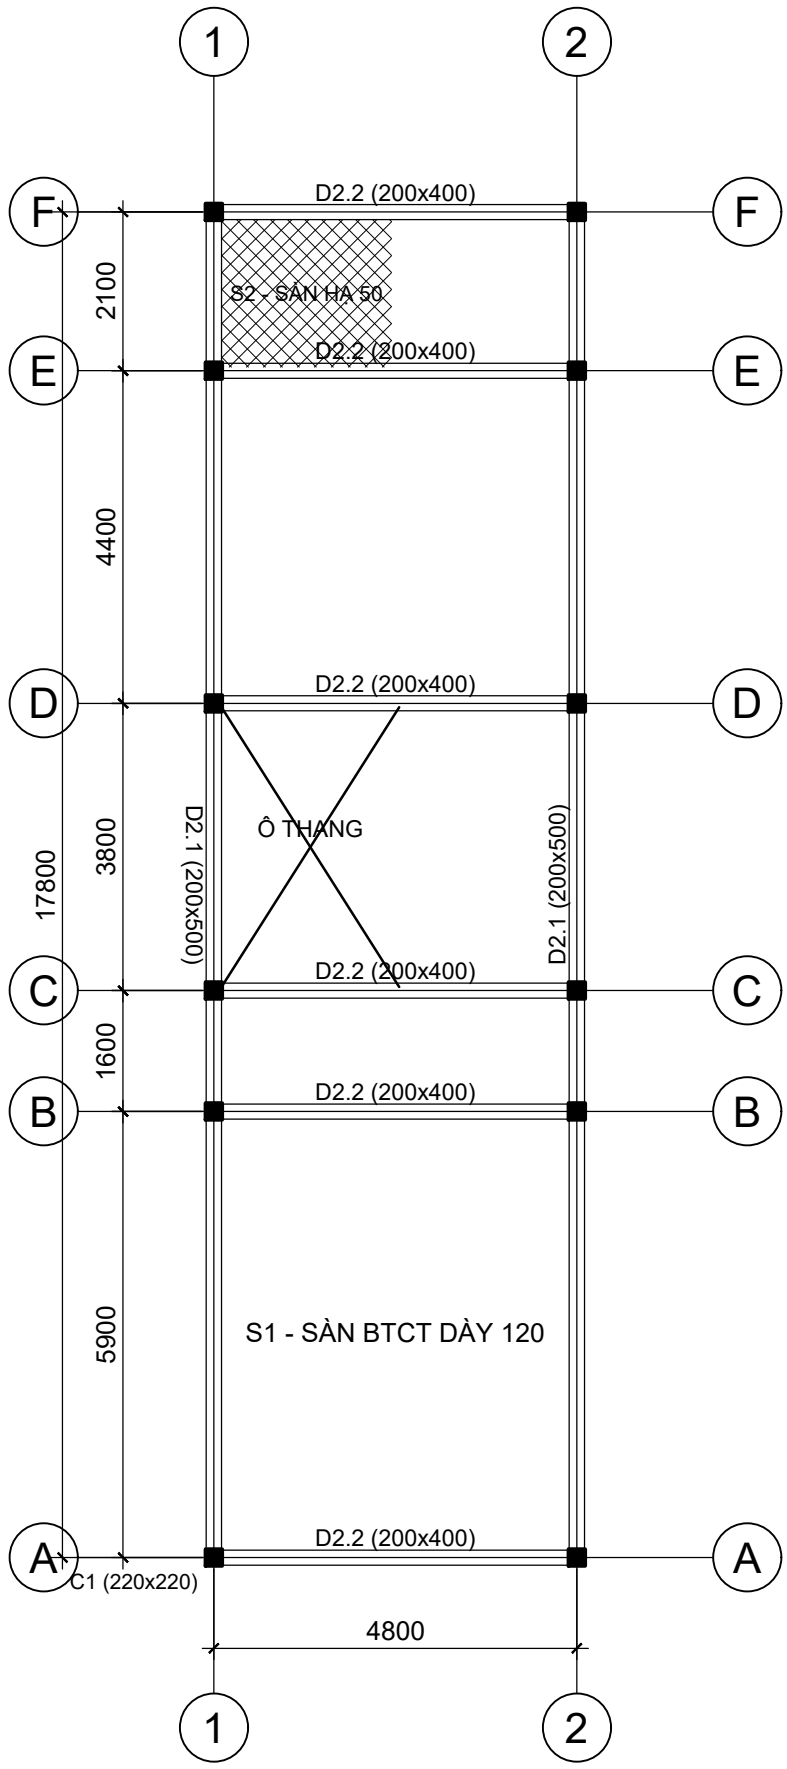

MẶT BẰNG KẾT CẤU SÀN TẦNG 2 (+3.600)

TỶ LỆ: 1/100


AUTOCAD MCP			
CÔNG TRÌNH NHÀ PHỐ 5x18m, 3 TẦNG + TUM		CHỦ ĐẦU TƯ CHỦ ĐẦU TƯ (MẪU)	
TÊN BẢN VẼ MẶT BẰNG KẾT CẤU SÀN TẦNG 2			
TỶ LỆ 1:100	NGÀY 03/11/2026	THIẾT KẾ AutoCAD MCP	KIỂM TRA ...
SỐ BẢN VẼ KC-02		LẦN SỬA 01	TỜ

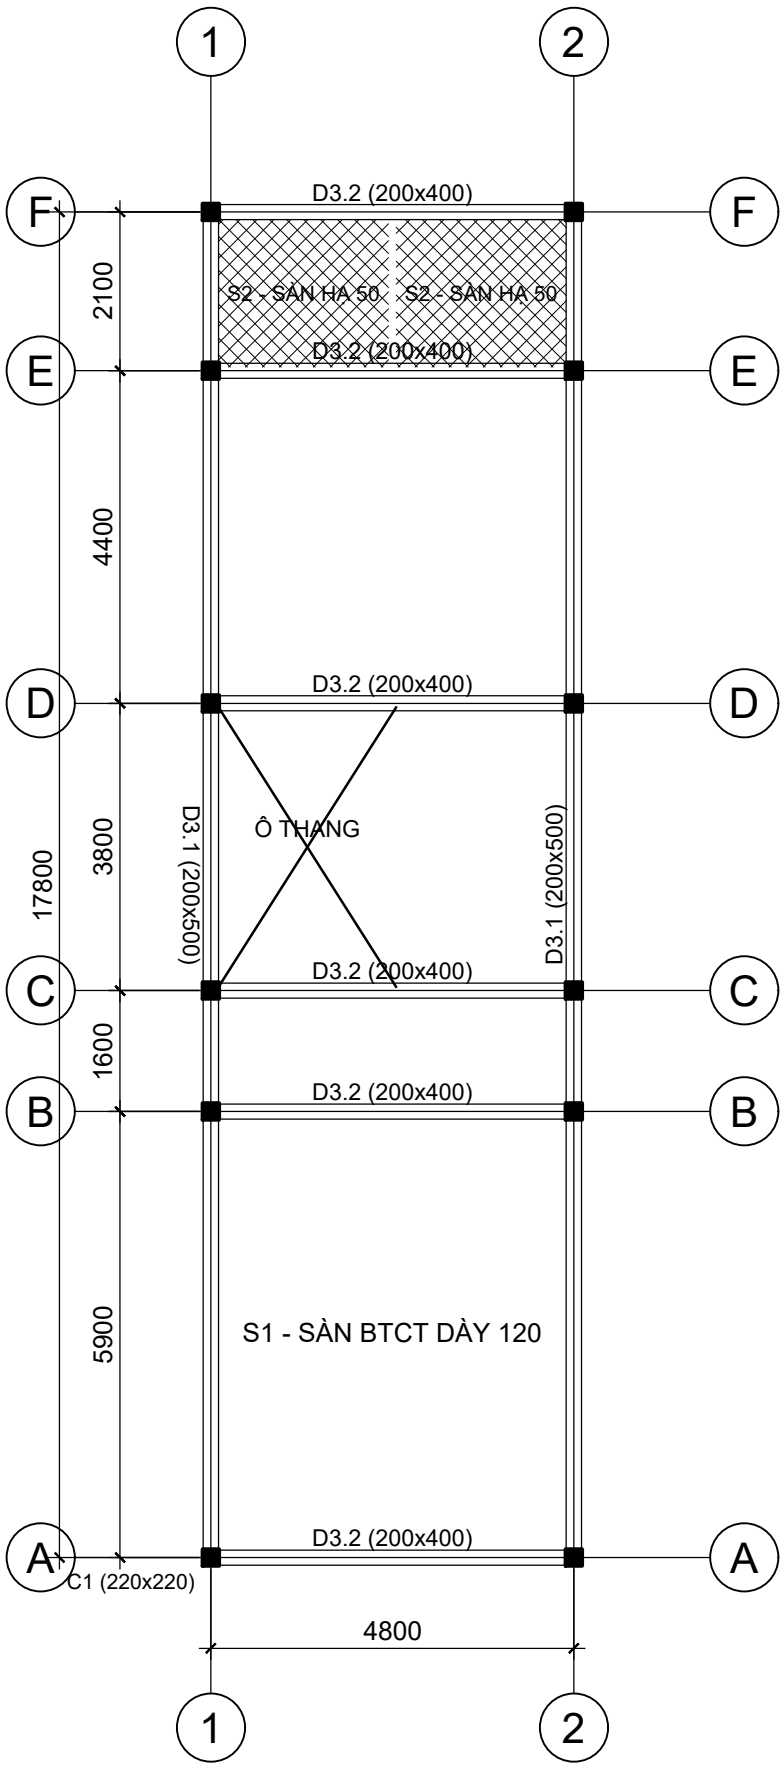

MẶT BẰNG KẾT CẤU SÀN TẦNG 3 (+6.900)

TỶ LỆ: 1/100


AUTOCAD MCP			
CÔNG TRÌNH NHÀ PHỐ 5x18m, 3 TẦNG + TUM		CHỦ ĐẦU TƯ CHỦ ĐẦU TƯ (MẪU)	
TÊN BẢN VẼ MẶT BẰNG KẾT CẤU SÀN TẦNG 3			
TỶ LỆ 1:100	NGÀY 03/11/2026	THIẾT KẾ AutoCAD MCP	KIỂM TRA ...
SỐ BẢN VẼ KC-03		LẦN SỬA 01	TỜ

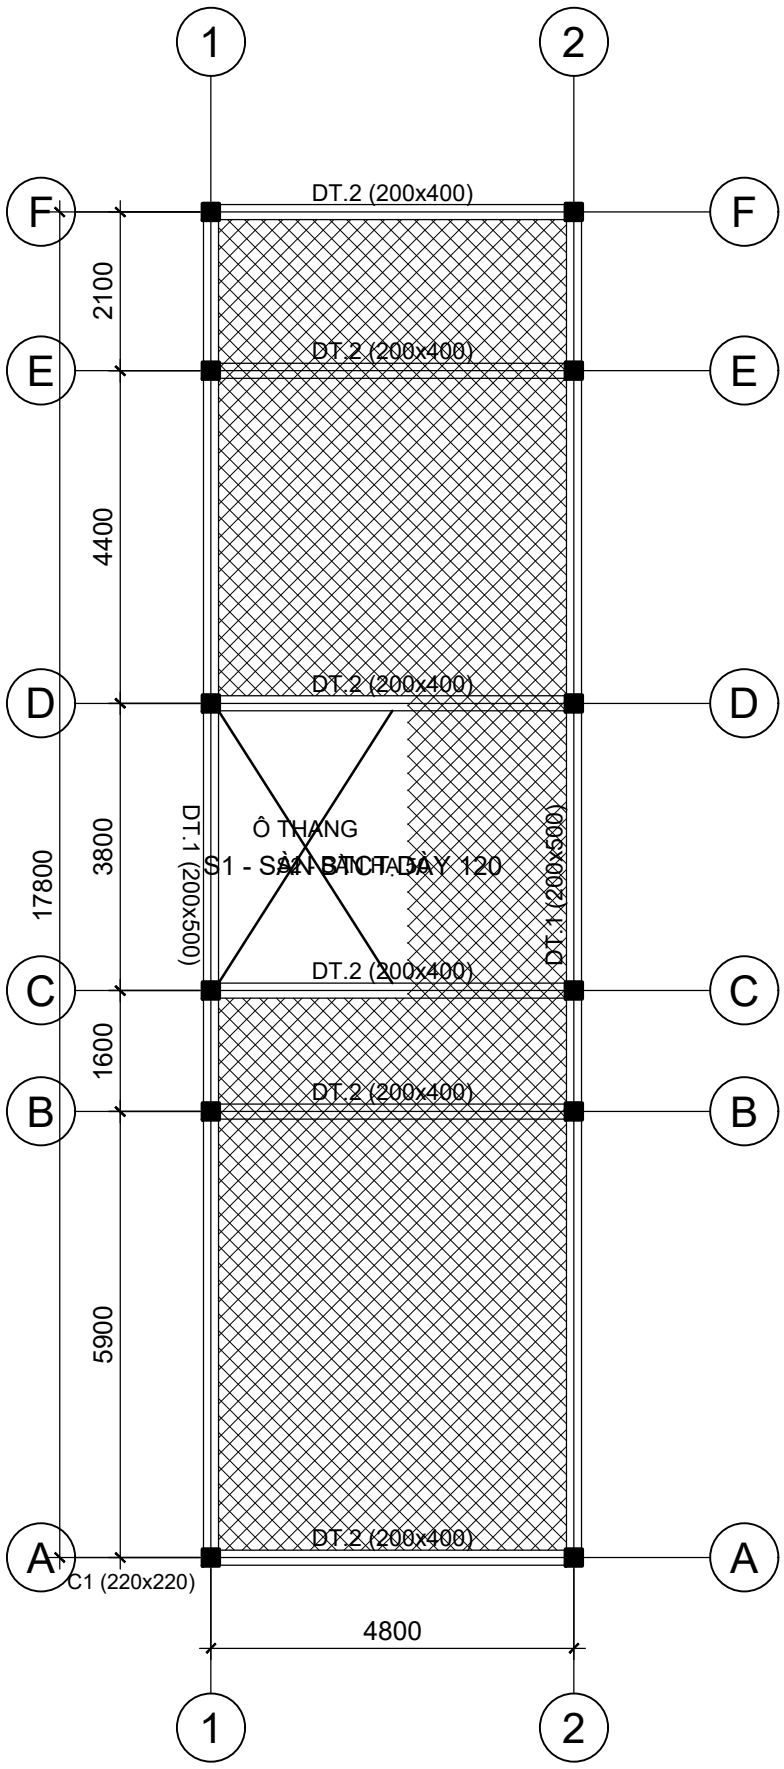

MẶT BẰNG KẾT CẤU SÀN TUM (+10.200)

TỶ LỆ: 1/100

AUTOCAD MCP			
CÔNG TRÌNH NHÀ PHỐ 5x18m, 3 TẦNG + TUM		CHỦ ĐẦU TƯ CHỦ ĐẦU TƯ (MẪU)	
TÊN BẢN VẼ MẶT BẰNG KẾT CẤU SÀN TUM			
TỶ LỆ 1:100	NGÀY 03/11/2026	THIẾT KẾ AutoCAD MCP	KIỂM TRA ...
SỐ BẢN VẼ KC-04	LẦN SỬA 01	TỜ	

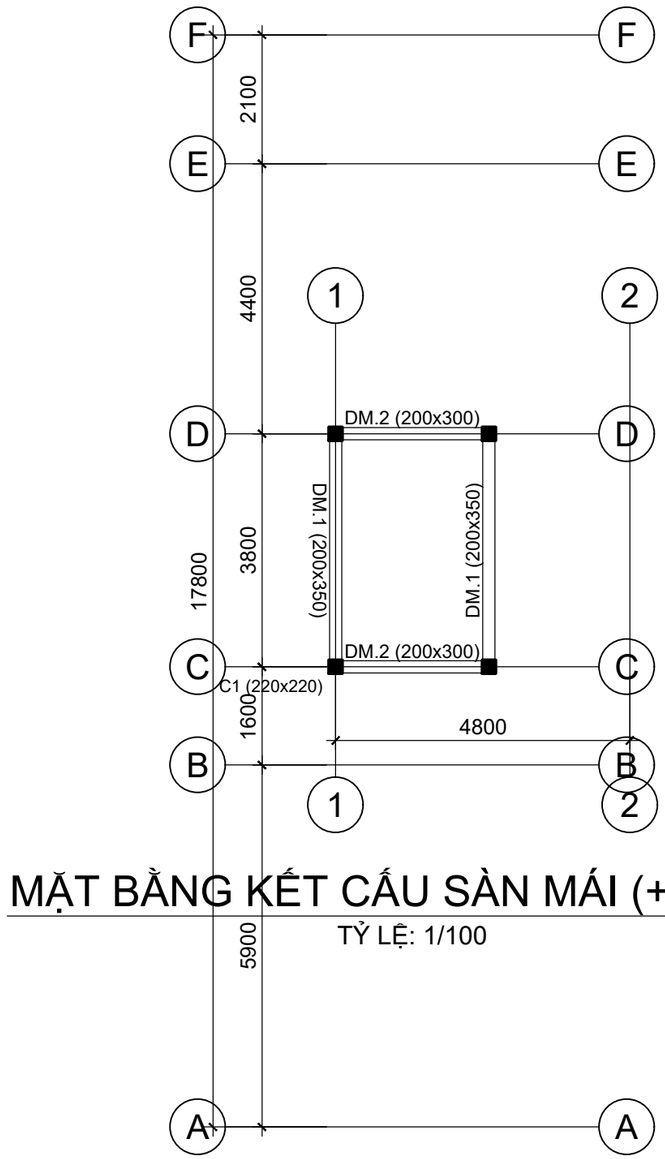

MẶT BẰNG KẾT CẤU SÀN MÁI (+13.120)

TỶ LỆ: 1/100

GHI CHÚ:NHÀ THẦU THI CÔNG KIỂM TRA KÍCH THƯỚC THỰC TẾ, NẾU THẤY CÓ XUNG ĐỘT CẦN BÁO LẠI CHO THIẾT KẾ VÀ QUẢN LÝ KỸ THUẬT.

LẦN NỘP	NỘI DUNG ĐIỀU CHỈNH	NGÀY NỘP
1		
2		
3		
4		

GHI CHÚ - Note:

CHỦ ĐẦU TƯ - Client:

CHỦ ĐẦU TƯ (MẪU)

DỰ ÁN - Project:

NHÀ PHỐ 5x18m, 3 TẦNG + TUM

Mẫu minh họa

HẠNG MỤC - Item:

KẾT CẤU

TƯ VẤN THIẾT KẾ - Consultant:


AUTOCAD MCP

CHỦ NHIỆM TK - Chief of Project	
CHỦ TRÌ TK - Chief of Division	
THIẾT KẾ - Designed by AutoCAD MCP	
KIỂM TRA - Checked by ...	


TÊN BẢN VẼ - Drawing name:

MẶT BẰNG KẾT CẤU SÀN MÁ

SỐ HĐ - Contract No:	PHIÊN BẢN - Version 01
GIAI ĐOẠN - Phase: TKTC	KÝ HIỆU BẢN VẼ - Drawing No KC-05
TỶ LỆ - Scale: 1:100	HOÀN THÀNH - Finish: 03/11/2026

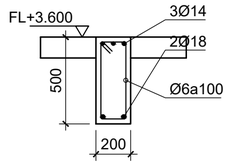


GỐI

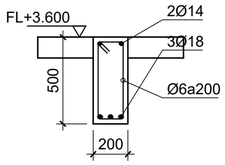


NHỊP

DẦM D2.1 (200x500) - SL: 02

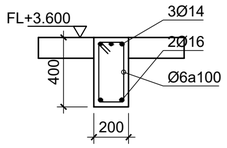


GỐI

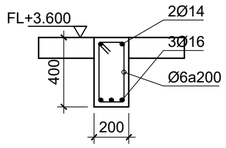


NHỊP

DẦM D2.2 (200x400) - SL: 06

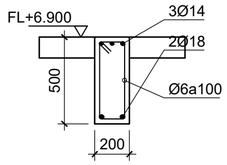


GỐI

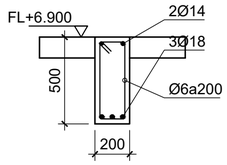


NHỊP

DẦM D3.1 (200x500) - SL: 02

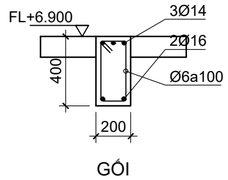


GỐI

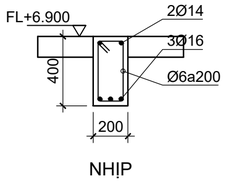


NHỊP

DẦM D3.2 (200x400) - SL: 06

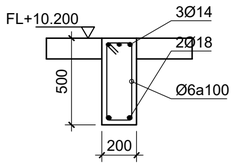


GỐI

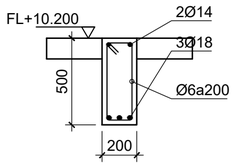


NHỊP

DẦM DT.1 (200x500) - SL: 02

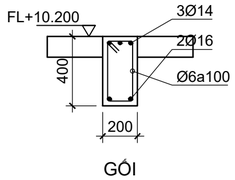


GỐI

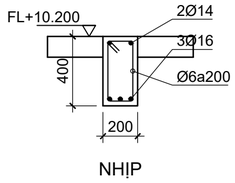


NHỊP

DẦM DT.2 (200x400) - SL: 06

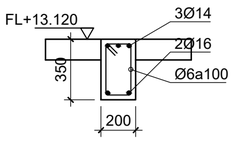


GỐI

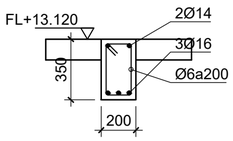


NHỊP

DẦM DM.1 (200x350) - SL: 02

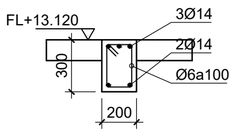

GỐI

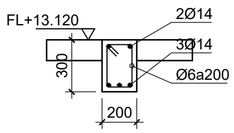

NHỊP

DẦM DM.2 (200x300) - SL: 02

BẢNG MẶT CẮT DẦM

TỶ LỆ: 1/25

GHI CHÚ:NHÀ THẦU THI CÔNG KIỂM TRA KÍCH THƯỚC THỰC TẾ, NẾU THẤY CÓ XUNG ĐỘT CẦN BÁO LẠI CHO THIẾT KẾ VÀ QUẢN LÝ KỸ THUẬT.

LẦN NỘP	NỘI DUNG ĐIỀU CHỈNH	NGÀY NỘP
1		
2		
3		
4		

GHI CHÚ - Note:

CHỦ ĐẦU TƯ - Client:

CHỦ ĐẦU TƯ (MẪU)

DỰ ÁN - Project:

NHÀ PHỐ 5x18m, 3 TẦNG + TUM

Mẫu minh họa

HẠNG MỤC - Item:

KẾT CẤU

TƯ VẤN THIẾT KẾ - Consultant:

AUTOCAD MCP

CHỦ NHIỆM TK - Chief of Project	
CHỦ TRÌ TK - Chief of Division	
THIẾT KẾ - Designed by AutoCAD MCP	
KIỂM TRA - Checked by ...	

TÊN BẢN VẼ - Drawing name:

BẢNG MẶT CẮT DẦM

SỐ HĐ - Contract No:	PHIÊN BẢN - Version 01
GIAI ĐOẠN - Phase: TKTC	KÝ HIỆU BẢN VẼ - Drawing No KC-06
TỶ LỆ - Scale: 1:25	HOÀN THÀNH - Finish: 03/11/2026