DANH MỤC BẢN VẼ - KIẾN TRÚC

STT	KÝ HIỆU	TÊN BẢN VẼ	TỶ LỆ	KHỔ GIẤY	GHI CHÚ
1	KT-00	DANH MỤC BẢN VẼ KIẾN TRÚC	1:50	A3 ngang	
2	KT-01	MẶT BẰNG TẦNG 1, TẦNG 2	1:100	A2 ngang	
3	KT-02	MẶT BẰNG TẦNG 3, TUM	1:100	A2 ngang	
4	KT-03	MẶT ĐỨNG CHÍNH, MẶT ĐỨNG SAU	1:100	A3 ngang	
5	KT-04	MẶT ĐỨNG TRỤC F-A	1:100	A3 ngang	
6	KT-05	MẶT CẮT A-A, B-B	1:100	A2 ngang	

GHI CHÚ:NHÀ THẦU THI CÔNG KIỂM TRA KÍCH THƯỚC THỰC TẾ, NẾU THẤY CÓ XUNG ĐỘT CẦN BÁO LẠI CHO THIẾT KẾ VÀ QUẢN LÝ KỸ THUẬT.

LẦN NỘP	NỘI DUNG ĐIỀU CHỈNH	NGÀY NỘP
1		
2		
3		
4		

GHI CHÚ - Note:

CHỦ ĐẦU TƯ - Client:

CHỦ ĐẦU TƯ (MẪU)

DỰ ÁN - Project:

NHÀ PHỐ 5x18m, 3 TẦNG + TUM

Mẫu minh họa

HẠNG MỤC - Item:

KIẾN TRÚC

TƯ VẤN THIẾT KẾ - Consultant:


AUTOCAD MCP

CHỦ NHIỆM TK - Chief of Project	
CHỦ TRÌ TK - Chief of Division	
THIẾT KẾ - Designed by AutoCAD MCP	
KIỂM TRA - Checked by ...	

TÊN BẢN VẼ - Drawing name:

DANH MỤC BẢN VẼ KIẾN TRÚC

SỐ HĐ - Contract No:	PHIÊN BẢN - Version 01
GIAI ĐOẠN - Phase: TKTC	KÝ HIỆU BẢN VẼ - Drawing No KT-00
TỶ LỆ - Scale: 1:50	HOÀN THÀNH - Finish: 03/11/2026

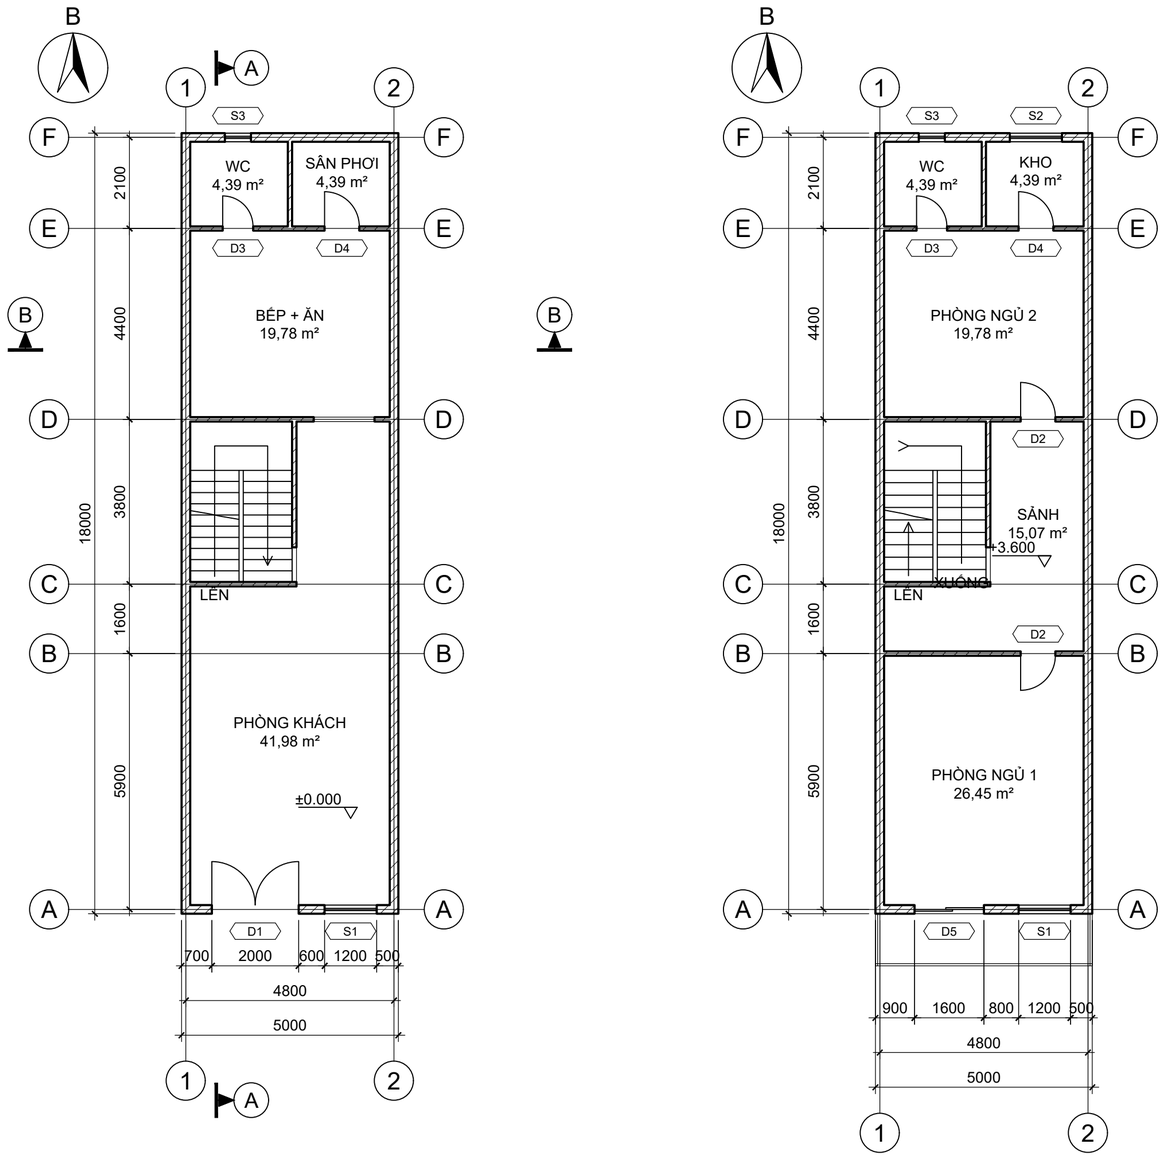

MẶT BẰNG TẦNG 1

TỶ LỆ: 1/100

MẶT BẰNG TẦNG 2

TỶ LỆ: 1/100

LẦN NỘP	NỘI DUNG ĐIỀU CHỈNH	NGÀY NỘP
1		
2		
3		
4		

GHI CHÚ - Note:

CHỦ ĐẦU TƯ - Client:

CHỦ ĐẦU TƯ (MẪU)

DỰ ÁN - Project:

NHÀ PHỐ 5x18m, 3 TẦNG + TUM

Mẫu minh họa

HẠNG MỤC - Item:

KIẾN TRÚC

TƯ VẤN THIẾT KẾ - Consultant:

AUTOCAD MCP


CHỦ NHIỆM TK - Chief of Project	
CHỦ TRÌ TK - Chief of Division	
THIẾT KẾ - Designed by AutoCAD MCP	
KIỂM TRA - Checked by ...	

TÊN BẢN VẼ - Drawing name:

MẶT BẰNG TẦNG 1, TẦNG 2


SỐ HĐ - Contract No:	PHIÊN BẢN - Version 01
GIAI ĐOẠN - Phase: TKTC	KÝ HIỆU BẢN VẼ - Drawing No KT-01
TỶ LỆ - Scale: 1:100	HOÀN THÀNH - Finish: 03/11/2026

GHI CHÚ: NHÀ THẦU THI CÔNG KIỂM TRA KÍCH THƯỚC THỰC TẾ, NẾU THẤY CÓ XUNG ĐỘT CẦN BÁO LẠI CHO THIẾT KẾ VÀ QUẢN LÝ KỸ THUẬT.

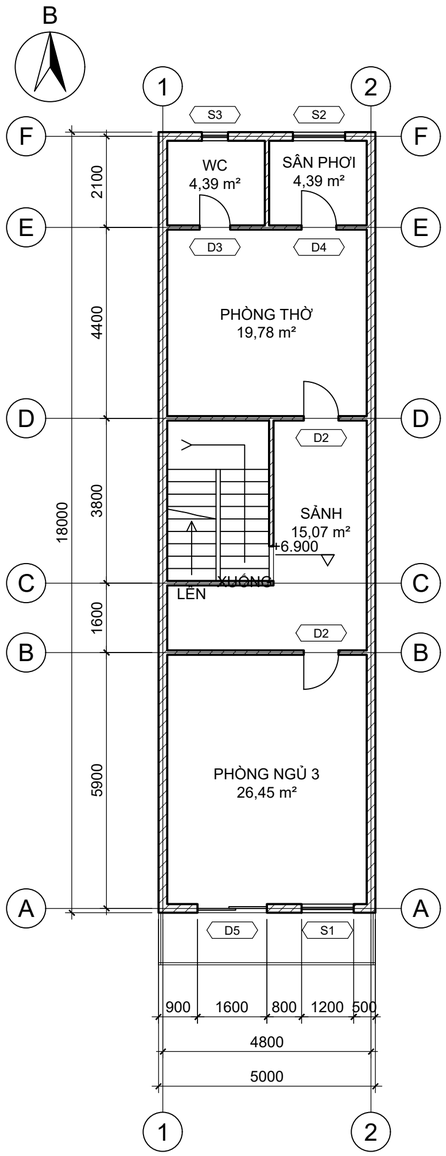

MẶT BẰNG TẦNG 3

TỶ LỆ: 1/100

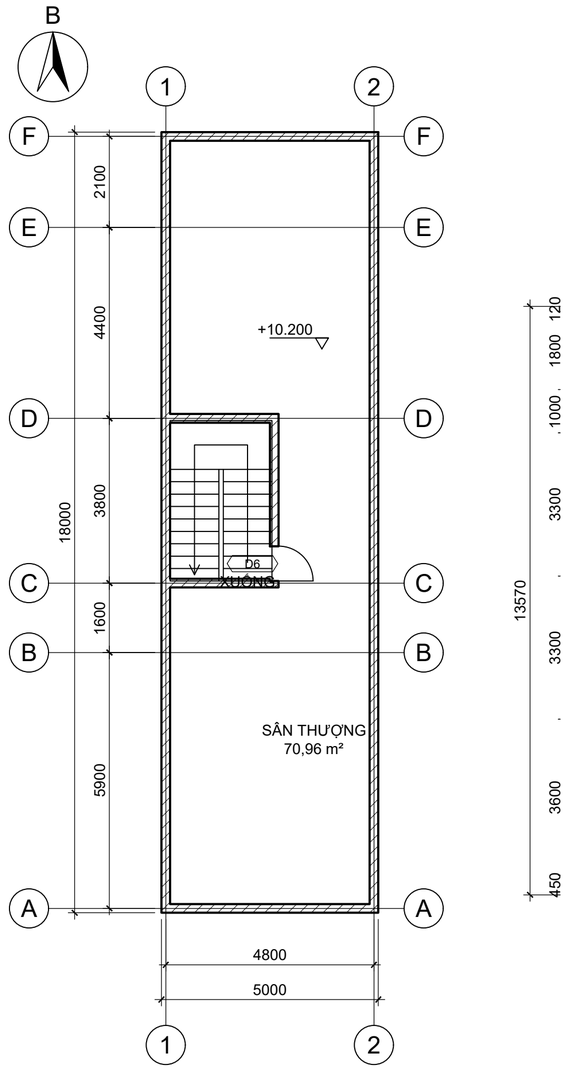

MẶT BẰNG TUM

TỶ LỆ: 1/100

MẶ

LẦN NỘP	NỘI DUNG ĐIỀU CHỈNH	NGÀY NỘP
1		
2		
3		
4		

GHI CHÚ - Note:

CHỦ ĐẦU TƯ - Client:

CHỦ ĐẦU TƯ (MẪU)

DỰ ÁN - Project:

NHÀ PHỐ 5x18m, 3 TẦNG + TUM

Mẫu minh họa

HẠNG MỤC - Item:

KIẾN TRÚC

TƯ VẤN THIẾT KẾ - Consultant:

AUTOCAD MCP


CHỦ NHIỆM TK - Chief of Project	
CHỦ TRÌ TK - Chief of Division	
THIẾT KẾ - Designed by AutoCAD MCP	
KIỂM TRA - Checked by ...	

TÊN BẢN VẼ - Drawing name:

MẶT BẰNG TẦNG 3, TUM


SỐ HĐ - Contract No:	PHIÊN BẢN - Version 01
GIAI ĐOẠN - Phase: TKTC	KÝ HIỆU BẢN VẼ - Drawing No. KT-02
TỶ LỆ - Scale: 1:100	HOÀN THÀNH - Finish: 03/11/2026

GHI CHÚ:NHÀ THẦU THI CÔNG KIỂM TRA KÍCH THƯỚC THỰC TẾ, NẾU THẤY CÓ XUNG ĐỘT CẦN BÁO LẠI CHO THIẾT KẾ VÀ QUẢN LÝ KỸ THUẬT.

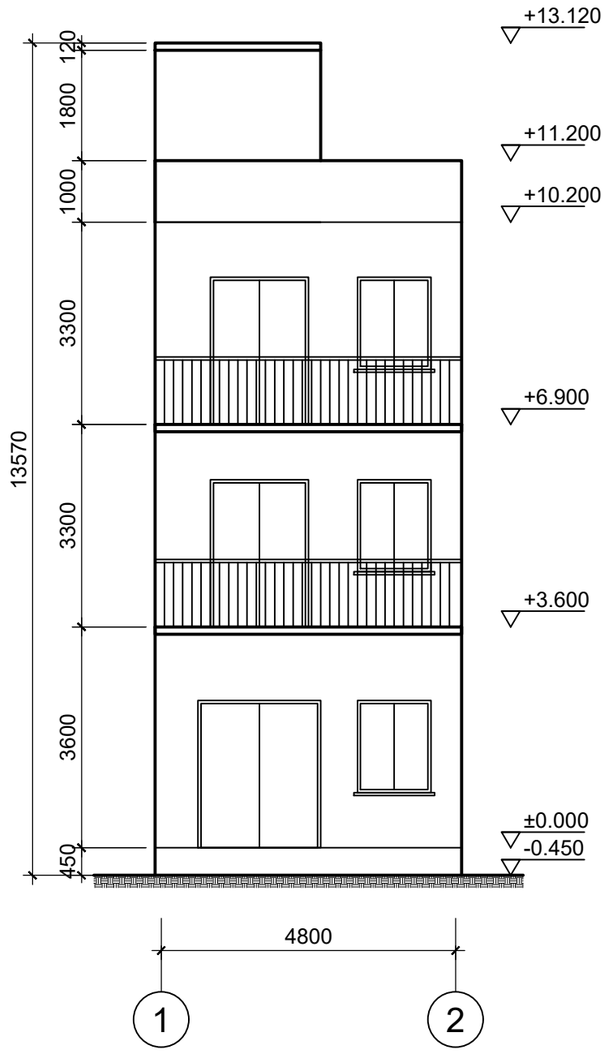

MẶT ĐỨNG CHÍNH (TRỤC A)

TỶ LỆ: 1/100

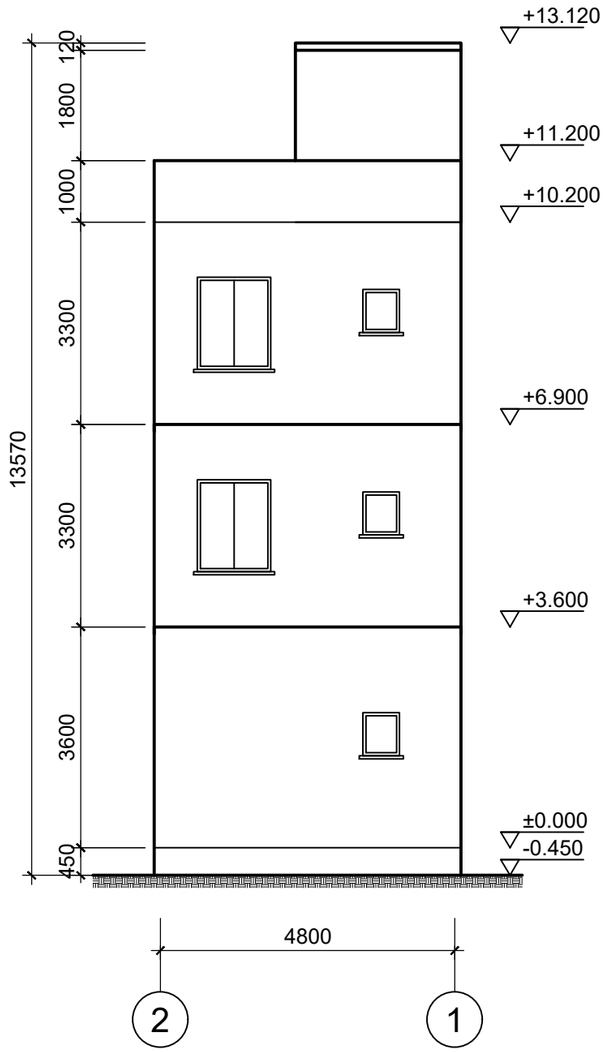

MẶT ĐỨNG SAU (TRỤC F)

TỶ LỆ: 1/100

LẦN NỘP	NỘI DUNG ĐIỀU CHỈNH	NGÀY NỘP
1		
2		
3		
4		

GHI CHÚ - Note:

CHỦ ĐẦU TƯ - Client:

CHỦ ĐẦU TƯ (MẪU)

DỰ ÁN - Project:

NHÀ PHỐ 5x18m, 3 TẦNG + TUM

Mẫu minh họa

HẠNG MỤC - Item:

KIẾN TRÚC

TƯ VẤN THIẾT KẾ - Consultant:

AUTOCAD MCP


CHỦ NHIỆM TK - Chief of Project	
CHỦ TRÌ TK - Chief of Division	
THIẾT KẾ - Designed by AutoCAD MCP	
KIỂM TRA - Checked by ...	

TÊN BẢN VẼ - Drawing name:

MẶT ĐỨNG CHÍNH, MẶT ĐỨNG SAU

SỐ HĐ - Contract No:	PHIÊN BẢN - Version 01
GIAI ĐOẠN - Phase: TKTC	KÝ HIỆU BẢN VẼ - Drawing No KT-03
TỶ LỆ - Scale: 1:100	HOÀN THÀNH - Finish: 03/11/2026

GHI CHÚ:NHÀ THẦU THI CÔNG KIỂM TRA KÍCH THƯỚC THỰC TẾ, NẾU THẤY CÓ XUNG ĐỘT CẦN BÁO LẠI CHO THIẾT KẾ VÀ QUẢN LÝ KỸ THUẬT.

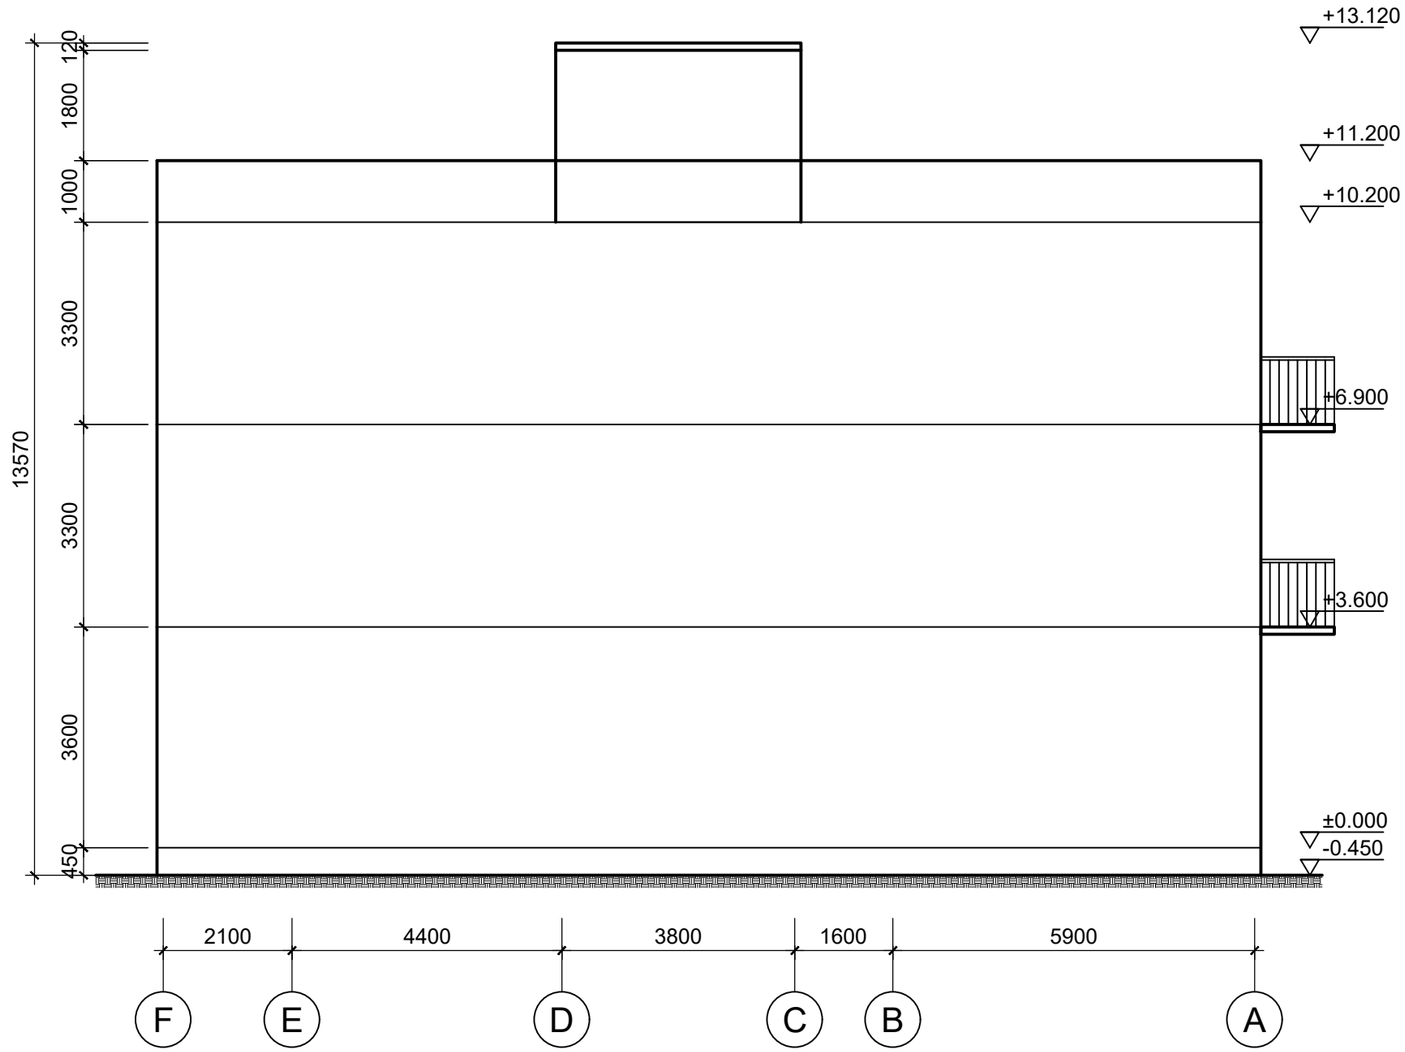

MẶT ĐỨNG TRỤC F-A

TỶ LỆ: 1/100

GHI CHÚ:NHÀ THẦU THI CÔNG KIỂM TRA KÍCH THƯỚC THỰC TẾ, NẾU THẤY CÓ XUNG ĐỘT CẦN BÁO LẠI CHO THIẾT KẾ VÀ QUẢN LÝ KỸ THUẬT.

LẦN NỘP	NỘI DUNG ĐIỀU CHỈNH	NGÀY NỘP
1		
2		
3		
4		

GHI CHÚ - Note:

CHỦ ĐẦU TƯ - Client:

CHỦ ĐẦU TƯ (MẪU)

DỰ ÁN - Project:

NHÀ PHỐ 5x18m, 3 TẦNG + TUM

Mẫu minh họa

HẠNG MỤC - Item:

KIẾN TRÚC

TƯ VẤN THIẾT KẾ - Consultant:


AUTOCAD MCP

CHỦ NHIỆM TK - Chief of Project	
CHỦ TRÌ TK - Chief of Division	
THIẾT KẾ - Designed by AutoCAD MCP	
KIỂM TRA - Checked by ...	

TÊN BẢN VẼ - Drawing name:


MẶT ĐỨNG TRỤC F-A

SỐ HĐ - Contract No:	PHIÊN BẢN - Version 01
GIAI ĐOẠN - Phase: TKTC	KÝ HIỆU BẢN VẼ - Drawing No KT-04
TỶ LỆ - Scale: 1:100	HOÀN THÀNH - Finish: 03/11/2026

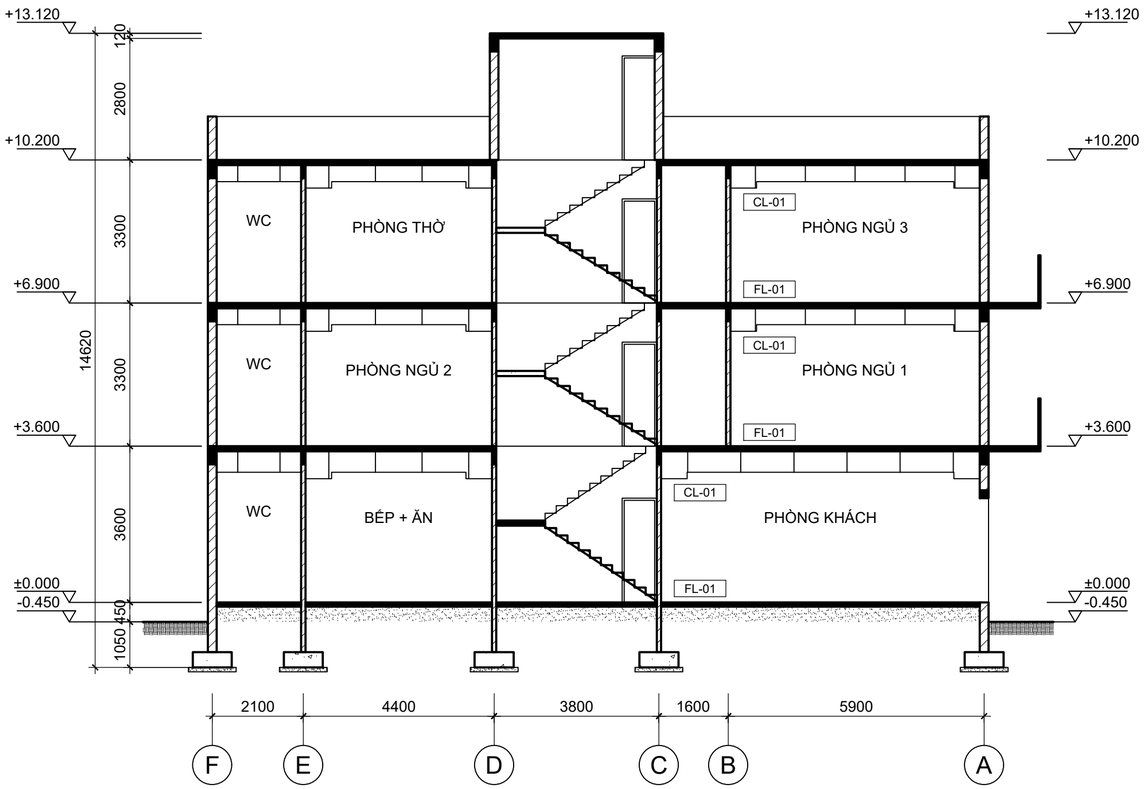

MẶT CẮT A-A

TỶ LỆ: 1/100

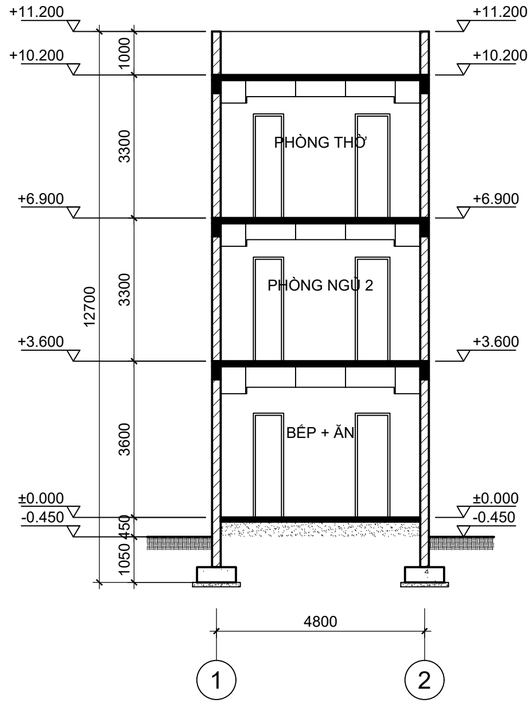

MẶT CẮT B-B

TỶ LỆ: 1/100

LẦN NỘP	NỘI DUNG ĐIỀU CHỈNH	NGÀY NỘP
1		
2		
3		
4		

GHI CHÚ - Note:

CHỦ ĐẦU TƯ - Client:

CHỦ ĐẦU TƯ (MẪU)

DỰ ÁN - Project:

NHÀ PHỐ 5x18m, 3 TẦNG + TUM

Mẫu minh họa

HẠNG MỤC - Item:

KIẾN TRÚC

TƯ VẤN THIẾT KẾ - Consultant:

AUTOCAD MCP

CHỦ NHIỆM TK - Chief of Project	
CHỦ TRÌ TK - Chief of Division	
THIẾT KẾ - Designed by AutoCAD MCP	
KIỂM TRA - Checked by ...	

TÊN BẢN VẼ - Drawing name:

MẶT CẮT A-A, B-B

SỐ HĐ - Contract No:	PHIÊN BẢN - Version 01
GIAI ĐOẠN - Phase: TKTC	KÝ HIỆU BẢN VẼ - Drawing No KT-05
TỶ LỆ - Scale: 1:100	HOÀN THÀNH - Finish: 03/11/2026

GHI CHÚ: NHÀ THẦU THI CÔNG KIỂM TRA KÍCH THƯỚC THỰC TẾ, NẾU THẤY CÓ XUNG ĐỘT CẦN BÁO LẠI CHO THIẾT KẾ VÀ QUẢN LÝ KỸ THUẬT.