HỒ SƠ BẢN VẼ KẾT CẤU

GIAI ĐOẠN: THIẾT KẾ THI CÔNG

CÔNG TRÌNH: NHÀ PHỐ 5x18m, 3 TẦNG + TUM

CHỦ ĐẦU TƯ: CHỦ ĐẦU TƯ (MẪU)

ĐƠN VỊ THIẾT KẾ: AUTOCAD MCP

ĐỊA ĐIỂM XÂY DỰNG: Mẫu minh họa

NGÀY: 11/2026

GHI CHÚ: NHÀ THẦU THI CÔNG KIỂM TRA KÍCH THƯỚC THỰC TẾ, NẾU THẤY CÓ XUNG ĐỘT CẦN BÁO LẠI CHO THIẾT KẾ VÀ QUẢN LÝ KỸ THUẬT.

LẦN NỘP	NỘI DUNG ĐIỀU CHỈNH	NGÀY NỘP
1		
2		
3		
4		

GHI CHÚ - Note:

CHỦ ĐẦU TƯ - Client:
CHỦ ĐẦU TƯ (MẪU)

DỰ ÁN - Project:
NHÀ PHỐ 5x18m, 3 TẦNG + TUM
Mẫu minh họa

HẠNG MỤC - Item:
KẾT CẤU

TƯ VẤN THIẾT KẾ - Consultant:
AUTOCAD MCP

CHỦ NHIỆM TK - Chief of Project	
CHỦ TRÌ TK - Chief of Division	
THIẾT KẾ - Designed by AutoCAD MCP	
KIỂM TRA - Checked by ...	

TÊN BẢN VẼ - Drawing name:
TỜ BÌA

SỐ HĐ - Contract No:	PHIÊN BẢN - Version 01
GIAI ĐOẠN - Phase: TKTC	KÝ HIỆU BẢN VẼ - Drawing No KC-BIA
TỶ LỆ - Scale: 1:50	HOÀN THÀNH - Finish: 03/11/2026

LẦN NỘP	NỘI DUNG ĐIỀU CHỈNH	NGÀY NỘP
1		
2		
3		
4		

GHI CHÚ - Note:

DANH MỤC BẢN VẼ - KẾT CẤU

STT	KÝ HIỆU	TÊN BẢN VẼ	TỶ LỆ	KHỔ GIẤY	GHI CHÚ
1	KC-BIA	TỜ BÌA		A2	
2	KC-00	DANH MỤC BẢN VẼ KẾT CẤU	1:50	A2	
3	KC-01	GHI CHÚ CHUNG KẾT CẤU	1:50	A2	
4	KC-02	MẶT BẰNG MÓNG, GIẰNG MÓNG, CHI TIẾT MÓNG M1	NHƯ HÌNH	A2	
5	KC-03	MẶT BẰNG KẾT CẤU SÀN TẦNG 2, TẦNG 3	1:100	A2	
6	KC-04	MẶT BẰNG KẾT CẤU SÀN TUM, SÀN MÁI	1:100	A2	
7	KC-05	BẢNG MẶT CẮT DẦM	1:25	A2	
8	KC-06	BẢNG TĨNH KẾT CẤU SƠ BỘ	1:50	A2	
9	KC-07	BẢNG THỐNG KÊ CỐT THÉP (1/2)	1:25	A2	
10	KC-08	BẢNG THỐNG KÊ CỐT THÉP (2/2)	1:25	A2	
11	KC-09	BẢNG TỔNG HỢP KHỐI LƯỢNG VẬT TƯ	1:25	A2	

GHI CHÚ:NHÀ THẦU THI CÔNG KIỂM TRA KÍCH THƯỚC THỰC TẾ, NẾU THẤY CÓ XUNG ĐỘT CẦN BÁO LẠI CHO THIẾT KẾ VÀ QUẢN LÝ KỸ THUẬT.

CHỦ ĐẦU TƯ - Client:

CHỦ ĐẦU TƯ (MẪU)

DỰ ÁN - Project:

NHÀ PHỐ 5x18m, 3 TẦNG + TUM

Mẫu minh họa

HẠNG MỤC - Item:

KẾT CẤU

TƯ VẤN THIẾT KẾ - Consultant:

AUTOCAD MCP

CHỦ NHIỆM TK - Chief of Project	
CHỦ TRÌ TK - Chief of Division	
THIẾT KẾ - Designed by AutoCAD MCP	
KIỂM TRA - Checked by ...	

TÊN BẢN VẼ - Drawing name:

DANH MỤC BẢN VẼ KẾT CẤU

SỐ HĐ - Contract No:	PHIÊN BẢN - Version 01
GIAI ĐOẠN - Phase: TKTC	KÝ HIỆU BẢN VẼ - Drawing No KC-00
TỶ LỆ - Scale: 1:50	HOÀN THÀNH - Finish: 03/11/2026

GHI CHÚ CHUNG KẾT CẤU

VẬT LIỆU		
CẤU KIỆN	VẬT LIỆU	GHI CHÚ
Móng, dầm móng, cột, dầm, sàn, cầu thang	Bê tông B20 (M250)	Đổ tại chỗ, đầm kỹ, bảo dưỡng ẩm ≥ 7 ngày
Lanh tô, bổ trụ, giằng tường	Bê tông B15 (M200)	
Bê tông lót móng	Bê tông B7,5 (M100)	Dày 100
Thép Ø < 10	CB240-T	TCVN 1651-1:2018
Thép Ø ≥ 10	CB300-V	TCVN 1651-2:2018

LỚP BÊ TÔNG BẢO VỆ (mm)	
CẤU KIỆN	a (mm)
Móng (có bê tông lót)	40
Dầm móng	30
Cột	25
Dầm	25
Sàn, cầu thang	20
Lanh tô, bổ trụ	15

CHIỀU DÀI NEO VÀ NỐI CHỒNG (mm)				
Ø	NEO KÉO 30d	NEO NÉN 20d	NỐI KÉO 40d	NỐI NÉN 30d
Ø10	300	200	400	300
Ø12	400	250	500	400
Ø14	450	300	600	450
Ø16	500	350	650	500
Ø18	550	400	750	550
Ø20	600	400	800	600
Ø22	700	450	900	700
Ø25	750	500	1000	750

LANH TÔ ĐIỂN HÌNH					
NHỊP Ô CỬA	TIẾT DIỆN	THÉP DƯỚI	THÉP TRÊN	ĐAI	GỐI (mm)
L ≤ 1200	220x150	2Ø10	2Ø10	Ø6a200	200
1200 < L ≤ 2000	220x200	2Ø12	2Ø10	Ø6a200	250
2000 < L ≤ 3000	220x300	2Ø14	2Ø12	Ø6a150	300
L > 3000	Theo thiết kế dầm				

GHI CHÚ:

1. Kích thước ghi bằng mm, cao độ ghi bằng m; cao độ ±0.000 là cao độ sàn hoàn thiện tầng 1.
2. Thiết kế theo TCVN 2737:2023 (tải trọng và tác động), TCVN 5574:2018 (kết cấu bê tông cốt thép).
3. Mối nối thép bố trí so le, không nối quá 50% số thanh tại một tiết diện; không nối thép chịu kéo tại vùng mô men lớn.
4. Cốp pha dầm, sàn chỉ tháo khi bê tông đạt ≥ 70% cường độ (nhịp ≤ 8 m) và ≥ 90% với công xôn.
5. Kích thước dầm, cột trên bản vẽ là sơ bộ theo nhịp: kỹ sư kết cấu tính toán, xác nhận trước khi thi công.
6. Nhà thầu kiểm tra kích thước thực tế, phối hợp bản vẽ kiến trúc, điện, nước trước khi thi công.

GHI CHÚ:NHÀ THẦU THI CÔNG KIỂM TRA KÍCH THƯỚC THỰC TẾ, NẾU THẤY CÓ XUNG ĐỘT CẦN BÁO LẠI CHO THIẾT KẾ VÀ QUẢN LÝ KỸ THUẬT.

LẦN NỘP	NỘI DUNG ĐIỀU CHỈNH	NGÀY NỘP
1		
2		
3		
4		

GHI CHÚ - Note:

CHỦ ĐẦU TƯ - Client:
CHỦ ĐẦU TƯ (MẪU)

DỰ ÁN - Project:
NHÀ PHỐ 5x18m, 3 TẦNG + TUM
Mẫu minh họa


HẠNG MỤC - Item:
KẾT CẤU

TƯ VẤN THIẾT KẾ - Consultant:
AUTOCAD MCP

CHỦ NHIỆM TK - Chief of Project	
CHỦ TRÌ TK - Chief of Division	
THIẾT KẾ - Designed by AutoCAD MCP	
KIỂM TRA - Checked by ...	

TÊN BẢN VẼ - Drawing name:
GHI CHÚ CHUNG KẾT CẤU


SỐ HĐ - Contract No:	PHIÊN BẢN - Version 01
GIAI ĐOẠN - Phase: TKTC	KÝ HIỆU BẢN VẼ - Drawing No: KC-01
TỶ LỆ - Scale: 1:50	HOÀN THÀNH - Finish: 03/11/2026

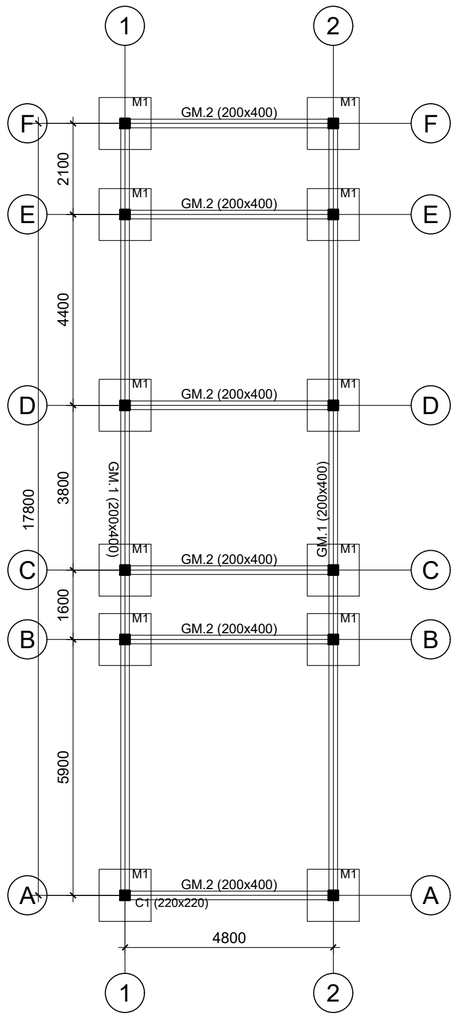

1. MÓNG ĐƠN M1 1200x1200
2. ĐÁY MÓNG -1.500
3. GIẰNG MÓNG GM DƯỚI TƯỜNG

MẶT BẰNG MÓNG, GIẰNG MÓNG

TỶ LỆ: 1/100

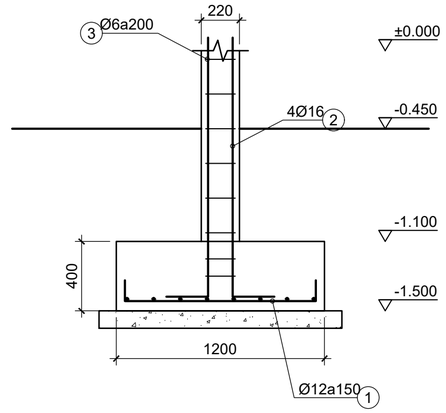

CHI TIẾT MÓNG M1 (1200x1200)

TỶ LỆ: 1/25

GHI CHÚ: NHÀ THẦU THI CÔNG KIỂM TRA KÍCH THƯỚC THỰC TẾ, NẾU THẤY CÓ XUNG ĐỘT CẦN BÁO LẠI CHO THIẾT KẾ VÀ QUẢN LÝ KỸ THUẬT.

LẦN NỘP	NỘI DUNG ĐIỀU CHỈNH	NGÀY NỘP
1		
2		
3		
4		

GHI CHÚ - Note:

CHỦ ĐẦU TƯ - Client:
CHỦ ĐẦU TƯ (MẪU)

DỰ ÁN - Project:
NHÀ PHỐ 5x18m, 3 TẦNG + TUM
Mẫu minh họa


HẠNG MỤC - Item:
KẾT CẤU

TƯ VẤN THIẾT KẾ - Consultant:
AUTOCAD MCP

CHỦ NHIỆM TK - Chief of Project	
CHỦ TRÌ TK - Chief of Division	
THIẾT KẾ - Designed by AutoCAD MCP	
KIỂM TRA - Checked by ...	


TÊN BẢN VẼ - Drawing name:
MẶT BẰNG MÓNG, GIẰNG MÓNG, CHI TIẾT MÓNG M1

SỐ HĐ - Contract No:	PHIÊN BẢN - Version 01
GIAI ĐOẠN - Phase: TKTC	KÝ HIỆU BẢN VẼ - Drawing No KC-02
TỶ LỆ - Scale: NHƯ HÌNH	HOÀN THÀNH - Finish: 03/11/2026

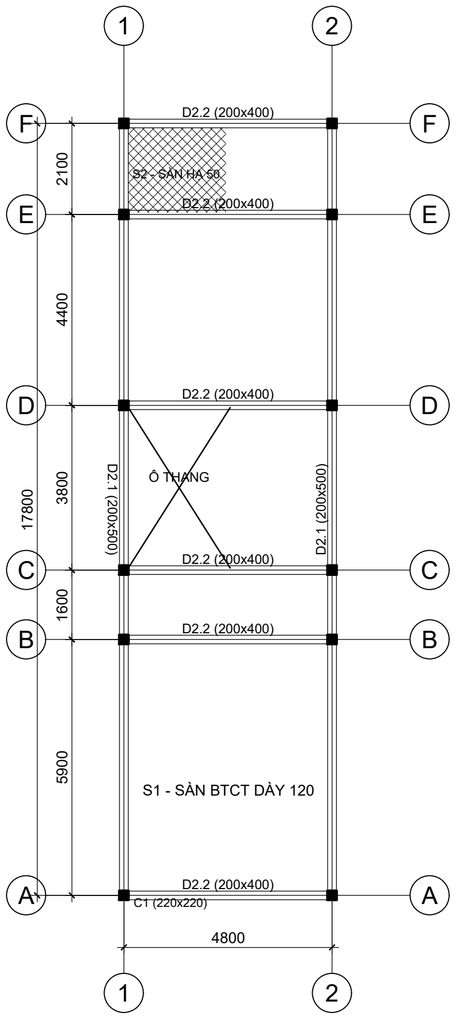

MẶT BẰNG KẾT CẤU SÀN TẦNG 2 (+3.600)

TỶ LỆ: 1/100

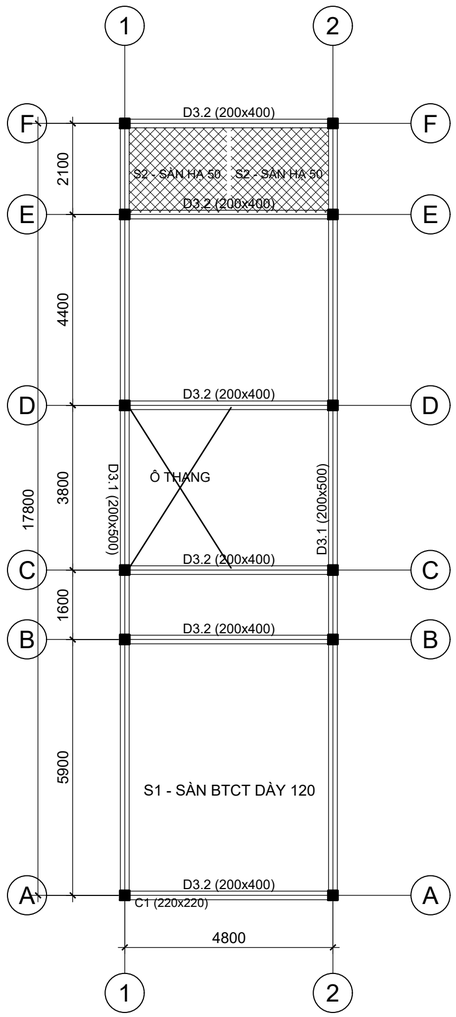

MẶT BẰNG KẾT CẤU SÀN TẦNG 3 (+6.900)

TỶ LỆ: 1/100

GHI CHÚ:NHÀ THẦU THI CÔNG KIỂM TRA KÍCH THƯỚC THỰC TẾ, NẾU THẤY CÓ XUNG ĐỘT CẦN BÁO LẠI CHO THIẾT KẾ VÀ QUẢN LÝ KỸ THUẬT.

LẦN NỘP	NỘI DUNG ĐIỀU CHỈNH	NGÀY NỘP
1		
2		
3		
4		

GHI CHÚ - Note:

CHỦ ĐẦU TƯ - Client:

CHỦ ĐẦU TƯ (MẪU)

DỰ ÁN - Project:

NHÀ PHỐ 5x18m, 3 TẦNG + TUM

Mẫu minh họa

HẠNG MỤC - Item:

KẾT CẤU

TƯ VẤN THIẾT KẾ - Consultant:


AUTOCAD MCP

CHỦ NHIỆM TK - Chief of Project	
CHỦ TRÌ TK - Chief of Division	
THIẾT KẾ - Designed by AutoCAD MCP	
KIỂM TRA - Checked by ...	

TÊN BẢN VẼ - Drawing name:


MẶT BẰNG KẾT CẤU SÀN TẦNG 2, TẦNG 3

SỐ HĐ - Contract No:	PHIÊN BẢN - Version 01
GIAI ĐOẠN - Phase: TKTC	KÝ HIỆU BẢN VẼ - Drawing No KC-03
TỶ LỆ - Scale: 1:100	HOÀN THÀNH - Finish: 03/11/2026

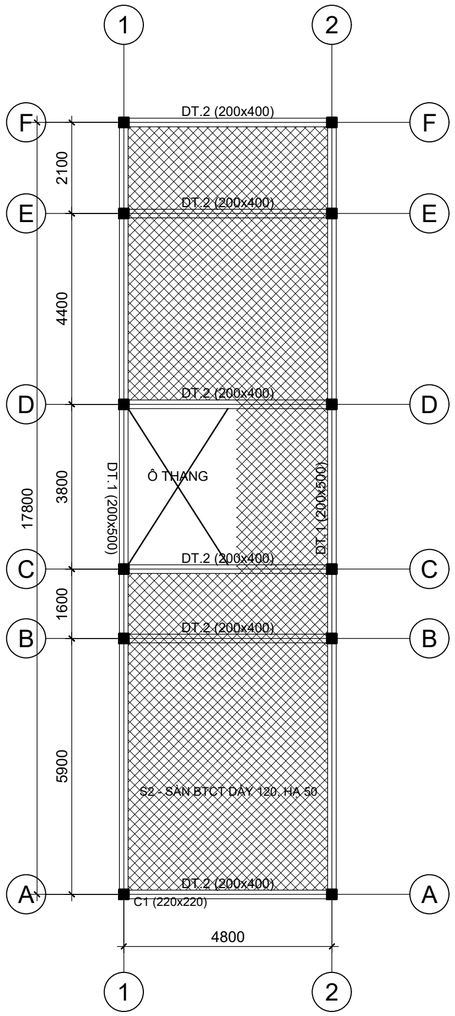

MẶT BẰNG KẾT CẤU SÀN TUM (+10.200)

TỶ LỆ: 1/100

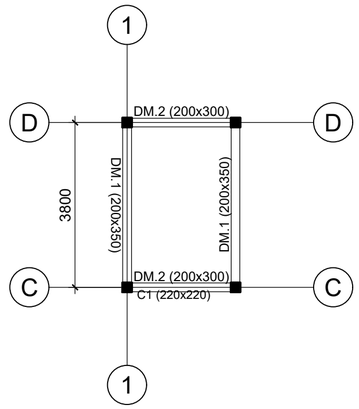

MẶT BẰNG KẾT CẤU SÀN MÁI (+13.120)

TỶ LỆ: 1/100

GHI CHÚ:NHÀ THẦU THI CÔNG KIỂM TRA KÍCH THƯỚC THỰC TẾ, NẾU THẤY CÓ XUNG ĐỘT CẦN BÁO LẠI CHO THIẾT KẾ VÀ QUẢN LÝ KỸ THUẬT.

LẦN NỘP	NỘI DUNG ĐIỀU CHỈNH	NGÀY NỘP
1		
2		
3		
4		

GHI CHÚ - Note:

CHỦ ĐẦU TƯ - Client:

CHỦ ĐẦU TƯ (MẪU)

DỰ ÁN - Project:

NHÀ PHỐ 5x18m, 3 TẦNG + TUM

Mẫu minh họa

HẠNG MỤC - Item:

KẾT CẤU

TƯ VẤN THIẾT KẾ - Consultant:


AUTOCAD MCP


CHỦ NHIỆM TK - Chief of Project	
CHỦ TRÌ TK - Chief of Division	
THIẾT KẾ - Designed by AutoCAD MCP	
KIỂM TRA - Checked by ...	

TÊN BẢN VẼ - Drawing name:


MẶT BẰNG KẾT CẤU SÀN TUM, SÀN MÁI

SỐ HĐ - Contract No:	PHIÊN BẢN - Version 01
GIAI ĐOẠN - Phase: TKTC	KÝ HIỆU BẢN VẼ - Drawing No KC-04
TỶ LỆ - Scale: 1:100	HOÀN THÀNH - Finish: 03/11/2026

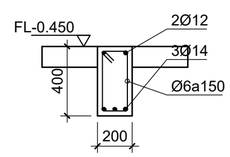


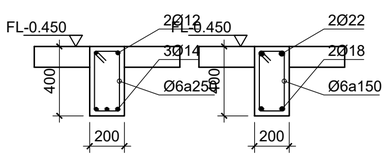


DẦM GM.2 (200x400) - SL: 06

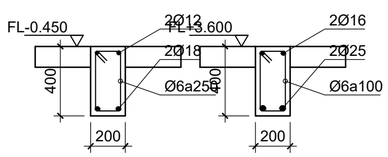


DẦM GM.1 (200x400) - SL: 02

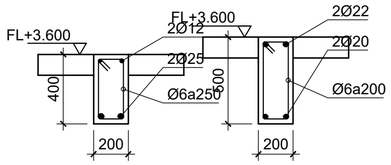


DẦM D2.2 (200x400) - SL: 06

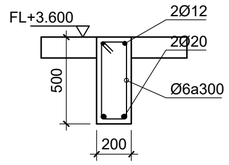


DẦM D2.1 (200x500) - SL: 02

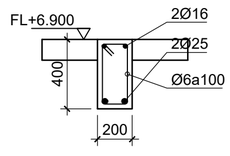


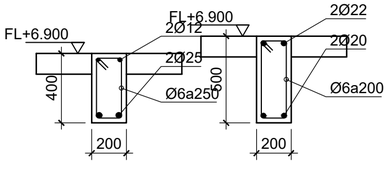


DẦM D3.2 (200x400) - SL: 06

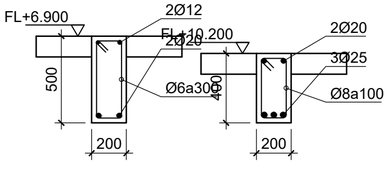


DẦM D3.1 (200x500) - SL: 02

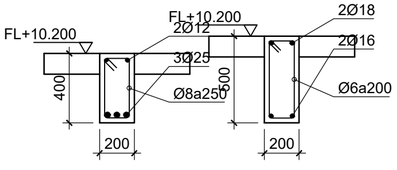


DẦM DT.2 (200x400) - SL: 06

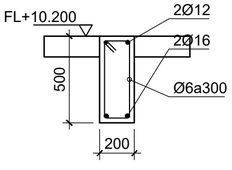


DẦM DT.1 (200x500) - SL: 02

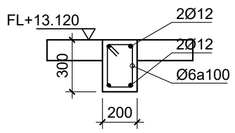

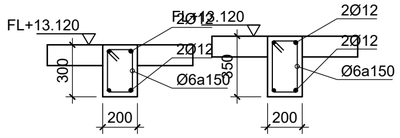

DẦM DM.2 (200x300) - SL: 02

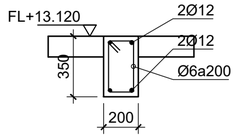

DẦM DM.1 (200x350) - SL: 02

BẢNG MẶT CẮT DẦM

TỶ LỆ: 1/25

GHI CHÚ:NHÀ THẦU THI CÔNG KIỂM TRA KÍCH THƯỚC THỰC TẾ, NẾU THẤY CÓ XUNG ĐỘT CẦN BÁO LẠI CHO THIẾT KẾ VÀ QUẢN LÝ KỸ THUẬT.

LẦN NỘP	NỘI DUNG ĐIỀU CHỈNH	NGÀY NỘP
1		
2		
3		
4		

GHI CHÚ - Note:

CHỦ ĐẦU TƯ - Client:

CHỦ ĐẦU TƯ (MẪU)

DỰ ÁN - Project:

NHÀ PHỐ 5x18m, 3 TẦNG + TUM

Mẫu minh họa

HẠNG MỤC - Item:

KẾT CẤU

TƯ VẤN THIẾT KẾ - Consultant:

AUTOCAD MCP

CHỦ NHIỆM TK - Chief of Project	
CHỦ TRÌ TK - Chief of Division	
THIẾT KẾ - Designed by AutoCAD MCP	
KIỂM TRA - Checked by ...	

TÊN BẢN VẼ - Drawing name:

BẢNG MẶT CẮT DẦM

SỐ HĐ - Contract No:	PHIÊN BẢN - Version 01
GIAI ĐOẠN - Phase: TKTC	KÝ HIỆU BẢN VẼ - Drawing No KC-05
TỶ LỆ - Scale: 1:25	HOÀN THÀNH - Finish: 03/11/2026

BẢNG TÍNH KẾT CẤU SƠ BỘ

Bảng tính do phần mềm lập để thể hiện bản vẽ: kỹ sư kết cấu có chứng chỉ hành nghề phải kiểm tra, tính toán lại và ký xác nhận trước khi dùng để thi công.

VẬT LIỆU (TCVN 5574:2018)		
VẬT LIỆU	CẤP	CƯỜNG ĐỘ TÍNH TOÁN (MPa)
Bê tông	B20	Rb = 11,5; Rbt = 0,90
Thép dọc	CB300-V	Rs = Rsc = 260; ξR = 0,583
Thép đai	CB240-T	Rsw = 170

TẢI TRỌNG SÀN (kN/m², TCVN 2737:2023)					
Ô SÀN / PHÒNG	TĨNH TẢI gk	TĨNH TẢI g	HOẠT TẢI pk	γf	HOẠT TẢI p
Phòng ở, phòng khách, bếp, phòng thờ	4,31	4,93	1,50	1,3	1,95
Sảnh, hành lang	4,31	4,93	3,00	1,2	3,60
Cầu thang	6,00	6,90	3,00	1,2	3,60
Sân thượng (mái có sử dụng)	4,65	5,41	1,50	1,3	1,95
Mái BTCT không sử dụng	4,45	5,19	0,75	1,3	0,98

CẤU TẠO SÀN ĐIỂN HÌNH (kN/m²)			
LỚP	gk	γf	g
Gạch lát dày 10	0,20	1,10	0,22
Vữa lót XM M75 dày 30	0,54	1,30	0,70
Sàn BTCT dày 120	3,00	1,10	3,30
Vữa trát trần dày 15	0,27	1,30	0,35
Trần, đường ống, thiết bị	0,30	1,20	0,36
Tổng	4,31		4,93

GHI CHÚ:

1. Tải trọng theo TCVN 2737:2023; tính toán theo TCVN 5574:2018 (tiết diện chữ nhật, cốt đơn, a = 40 mm).
2. Tải sàn truyền vào dầm: bản kê 4 cạnh (hình thang / tam giác) khi l2/l1 ≤ 2, ngược lại bản dầm.
3. Tường trên dầm đã trừ lỗ cửa; tường ngăn trên sàn quy về phân bố đều trên ô sàn.
4. Dầm liên tục, tính đàn hồi: hoạt tải đặt toàn bộ, nhịp lẻ, nhịp chẵn; mô men gối biên (liên kết cột) $qL^2/24$.
5. Cốt đai: Q ≤ Qb + Qsw với c = 2h0; s ≤ h0/2 và 300 ở vùng gối.
6. Cột: chỉ kiểm tra lực dọc; móng: diện tích theo áp lực đất giả thiết, chưa kiểm tra lún, chọc thủng.
7. Chưa xét: tải gió, động đất (TCVN 9386), độ võng, nứt, tính sàn, cầu thang, cấu tạo: kỹ sư kết cấu bổ sung.

DẦM: NỘI LỰC VÀ CỐT THÉP												
DẦM	b x h	NHỊP (m)	q (kN/m)	M+ (kNm)	As+	THÉP DƯỚI	M- (kNm)	As-	THÉP TRÊN	Q (kN)	ĐAI	KẾT LUẬN
GM.2 (SL 6)	200x400	4,80	19,1	36,7	419	3Ø14	18,3	202	2Ø12	45,8	Ø6a150/a250	ĐẠT
GM.1 (SL 2)	200x400	5,90+1,60+3,80+4,40+2,10	19,5	43,1	500	2Ø18	56,3	672	2Ø22	62,3	Ø6a150/a250	ĐẠT
D2.2 (SL 6)	200x400	4,80	36,1	69,4	857	2Ø25	34,7	395	2Ø16	86,7	Ø6a100/a250	ĐẠT
D2.1 (SL 2)	200x500	5,90+1,60+3,80+4,40+2,10	30,0	61,6	552	2Ø20	78,5	720	2Ø22	87,9	Ø6a200/a300	ĐẠT
D3.2 (SL 6)	200x400	4,80	36,1	69,4	857	2Ø25	34,7	395	2Ø16	86,7	Ø6a100/a250	ĐẠT
D3.1 (SL 2)	200x500	5,90+1,60+3,80+4,40+2,10	30,0	61,6	552	2Ø20	78,5	720	2Ø22	87,9	Ø6a200/a300	ĐẠT
DT.2 (SL 6)	200x400	4,80	48,0	92,1	1216	3Ø25	46,0	537	2Ø20	115,1	Ø8a100/a250	ĐẠT
DT.1 (SL 2)	200x500	5,90+1,60+3,80+4,40+2,10	33,3	45,4	399	2Ø16	56,6	505	2Ø18	68,8	Ø6a200/a300	ĐẠT
DM.2 (SL 2)	200x300	2,50	5,9	3,1	52	2Ø12	1,5	52	2Ø12	7,4	Ø6a100/a150	ĐẠT
DM.1 (SL 2)	200x350	3,80	7,7	9,3	118	2Ø12	4,7	62	2Ø12	14,7	Ø6a150/a200	ĐẠT

TẢI TRỌNG CỘT VÀ MÓNG (giả thiết R = 100 kPa)						
CỘT	N (kN)	KHẢ NĂNG (kN)	CỘT	MÓNG: A CẦN (m²)	A ĐÃ VẼ (m²)	MÓNG
1-D	808,6	689,1	KHÔNG ĐẠT	10,04	1,44	KHÔNG ĐẠT (≥ 3200x3200)
2-D	761,2	689,1	KHÔNG ĐẠT	9,46	1,44	KHÔNG ĐẠT (≥ 3100x3100)
2-B	681,4	689,1	ĐẠT	8,47	1,44	KHÔNG ĐẠT (≥ 3000x3000)
1-B	673,4	689,1	ĐẠT	8,36	1,44	KHÔNG ĐẠT (≥ 2900x2900)
2-E	492,1	689,1	ĐẠT	6,11	1,44	KHÔNG ĐẠT (≥ 2500x2500)
1-E	488,9	689,1	ĐẠT	6,07	1,44	KHÔNG ĐẠT (≥ 2500x2500)
1-A	441,8	689,1	ĐẠT	5,49	1,44	KHÔNG ĐẠT (≥ 2400x2400)
2-A	441,6	689,1	ĐẠT	5,49	1,44	KHÔNG ĐẠT (≥ 2400x2400)
1-C	397,4	689,1	ĐẠT	4,94	1,44	KHÔNG ĐẠT (≥ 2300x2300)
2-C	342,0	689,1	ĐẠT	4,25	1,44	KHÔNG ĐẠT (≥ 2100x2100)
1-F	222,5	689,1	ĐẠT	2,76	1,44	KHÔNG ĐẠT (≥ 1700x1700)
2-F	221,7	689,1	ĐẠT	2,75	1,44	KHÔNG ĐẠT (≥ 1700x1700)
(2600, 7600)	26,0	689,1	ĐẠT	-	-	đặt trên dầm sàn TUM
(2600, 11400)	26,0	689,1	ĐẠT	-	-	đặt trên dầm sàn TUM

XÁC NHẬN				
CHỨC DANH	HỌ VÀ TÊN	CHỨNG CHỈ HÀNH NGHỀ SỐ	CHỮ KÝ	NGÀY
Người tính				
Kiểm tra				
Chủ trì kết cấu				

LẦN NỘP	NỘI DUNG ĐIỀU CHỈNH	NGÀY NỘP
1		
2		
3		
4		

GHI CHÚ - Note:

CHỦ ĐẦU TƯ - Client:

CHỦ ĐẦU TƯ (MẪU)

DỰ ÁN - Project:

NHÀ PHỐ 5x18m, 3 TẦNG + TUM

Mẫu minh họa

HẠNG MỤC - Item: KẾT CẤU

TƯ VẤN THIẾT KẾ - Consultant:

AUTOCAD MCP

CHỦ NHIỆM TK - Chief of Project	
CHỦ TRÌ TK - Chief of Division	
THIẾT KẾ - Designed by: AutoCAD MCP	
KIỂM TRA - Checked by: ...	

TÊN BẢN VẼ - Drawing name:

BẢNG TÍNH KẾT CẤU SƠ BỘ

SỐ HĐ - Contract No:	PHIÊN BẢN - Version: 01
GIAI ĐOẠN - Phase: TKTC	KÝ HIỆU BẢN VẼ - Drawing No: KC-06
TỶ LỆ - Scale: 1:50	HOÀN THÀNH - Finish: 03/11/2026

GHI CHÚ:NHÀ THẦU THI CÔNG KIỂM TRA KÍCH THƯỚC THỰC TẾ, NẾU THẤY CÓ XUNG ĐỘT CẦN BÁO LẠI CHO THIẾT KẾ VÀ QUẢN LÝ KỸ THUẬT.

MÓNG M1 (1200x1200)								
SỐ HIỆU	HÌNH DẠNG	Ø (mm)	DÀI 1 THANH (mm)	SỐ THANH/CK	SỐ CK	TỔNG SỐ THANH	TỔNG DÀI (m)	KHỐI LƯỢNG (kg)
M1-1	Lưới đáy phương X, bẻ móc 150	12	1400	8	12	96	134,40	119,47
M1-2	Lưới đáy phương Y, bẻ móc 150	12	1400	8	12	96	134,40	119,47
Ø12								238,93
TỔNG CỘNG								238,93

CỘT 220x220								
SỐ HIỆU	HÌNH DẠNG	Ø (mm)	DÀI 1 THANH (mm)	SỐ THANH/CK	SỐ CK	TỔNG SỐ THANH	TỔNG DÀI (m)	KHỐI LƯỢNG (kg)
C1-1	Thép dọc cột, nối chồng 40d mỗi tầng	16	16920	4	2	8	135,36	213,90
C1-2	Đai cột Ø6a150	6	830	96	2	192	159,36	35,41
C2-1	Thép dọc cột, nối chồng 40d mỗi tầng	16	13360	4	10	40	534,40	844,48
C2-2	Đai cột Ø6a150	6	830	77	10	770	639,10	142,02
C3-1	Thép dọc cột, nối chồng 40d mỗi tầng	16	3880	4	2	8	31,04	49,05
C3-2	Đai cột Ø6a150	6	830	21	2	42	34,86	7,75
Ø6								185,18
Ø16								1107,44
TỔNG CỘNG								1292,62

GIẰNG MÓNG								
SỐ HIỆU	HÌNH DẠNG	Ø (mm)	DÀI 1 THANH (mm)	SỐ THANH/CK	SỐ CK	TỔNG SỐ THANH	TỔNG DÀI (m)	KHỐI LƯỢNG (kg)
GM.2-1	Thép dưới chạy suốt, neo 30d	14	5640	3	6	18	101,52	122,83
GM.2-2	Thép trên tại gối, dài L/3	12	1960	4	6	24	47,04	41,81
GM.2-3	Thép trên giữa nhịp (cấu tạo), nối 40d	12	2560	2	6	12	30,72	27,31
GM.2-4	Đai dầm Ø6a150/250	6	1150	27	6	162	186,30	41,40
GM.1-1	Thép dưới chạy suốt, neo 30d	18	19600	2	2	4	78,40	156,80
GM.1-2	Thép trên tại gối, dài L/3	22	2198	12	2	24	52,75	157,60
GM.1-3	Thép trên giữa nhịp (cấu tạo), nối 40d	12	2147	10	2	20	42,94	38,17
GM.1-4	Đai dầm Ø6a150/250	6	1150	107	2	214	246,10	54,69
Ø6								96,09
Ø12								107,29
Ø14								122,83
Ø18								156,80
Ø22								157,60
TỔNG CỘNG								640,61

DẦM SÀN TẦNG 2								
SỐ HIỆU	HÌNH DẠNG	Ø (mm)	DÀI 1 THANH (mm)	SỐ THANH/CK	SỐ CK	TỔNG SỐ THANH	TỔNG DÀI (m)	KHỐI LƯỢNG (kg)
D2.2-1	Thép dưới chạy suốt, neo 30d	25	6300	2	6	12	75,60	291,67
D2.2-2	Thép trên tại gối, dài L/3	16	2080	4	6	24	49,92	78,89
D2.2-3	Thép trên giữa nhịp (cấu tạo), nối 40d	12	2560	2	6	12	30,72	27,31
D2.2-4	Đai dầm Ø6a100/250	6	1150	35	6	210	241,50	53,67
D2.1-1	Thép dưới chạy suốt, neo 30d	20	19800	2	2	4	79,20	195,56
D2.1-2	Thép trên tại gối, dài L/3	22	2198	12	2	24	52,75	157,60
D2.1-3	Thép trên giữa nhịp (cấu tạo), nối 40d	12	2147	10	2	20	42,94	38,17
D2.1-4	Đai dầm Ø6a200/300	6	1350	85	2	170	229,50	51,00
Ø6								104,67
Ø12								65,48
Ø16								78,89
Ø20								195,56
Ø22								157,60
Ø25								291,67
TỔNG CỘNG								893,86

DẦM SÀN TẦNG 3								
SỐ HIỆU	HÌNH DẠNG	Ø (mm)	DÀI 1 THANH (mm)	SỐ THANH/CK	SỐ CK	TỔNG SỐ THANH	TỔNG DÀI (m)	KHỐI LƯỢNG (kg)
D3.2-1	Thép dưới chạy suốt, neo 30d	25	6300	2	6	12	75,60	291,67
D3.2-2	Thép trên tại gối, dài L/3	16	2080	4	6	24	49,92	78,89
D3.2-3	Thép trên giữa nhịp (cấu tạo), nối 40d	12	2560	2	6	12	30,72	27,31
D3.2-4	Đai dầm Ø6a100/250	6	1150	35	6	210	241,50	53,67
D3.1-1	Thép dưới chạy suốt, neo 30d	20	19800	2	2	4	79,20	195,56
D3.1-2	Thép trên tại gối, dài L/3	22	2198	12	2	24	52,75	157,60
D3.1-3	Thép trên giữa nhịp (cấu tạo), nối 40d	12	2147	10	2	20	42,94	38,17
D3.1-4	Đai dầm Ø6a200/300	6	1350	85	2	170	229,50	51,00
Ø6								104,67
Ø12								65,48
Ø16								78,89
Ø20								195,56
Ø22								157,60
Ø25								291,67
TỔNG CỘNG								893,86

BẢNG THỐNG KÊ CỐT THÉP (1/2)

GHI CHÚ: NHÀ THẦU THI CÔNG KIỂM TRA KÍCH THƯỚC THỰC TẾ, NẾU THẤY CÓ XUNG ĐỘT CẦN BÁO LẠI CHO THIẾT KẾ VÀ QUẢN LÝ KỸ THUẬT.

LẦN NỘP	NỘI DUNG ĐIỀU CHỈNH	NGÀY NỘP
1		
2		
3		
4		

GHI CHÚ - Note:

CHỦ ĐẦU TƯ - Client:
CHỦ ĐẦU TƯ (MẪU)

DỰ ÁN - Project:
NHÀ PHỐ 5x18m, 3 TẦNG + TUM
Mẫu minh họa

HẠNG MỤC - Item:
KẾT CẤU

TƯ VẤN THIẾT KẾ - Consultant:
AUTOCAD MCP

CHỦ NHIỆM TK - Chief of Project	
CHỦ TRÌ TK - Chief of Division	
THIẾT KẾ - Designed by: AutoCAD MCP	
KIỂM TRA - Checked by: ...	

TÊN BẢN VẼ - Drawing name:
BẢNG THỐNG KÊ CỐT THÉP (1/2)

SỐ HĐ - Contract No:	PHIÊN BẢN - Version: 01
GIAI ĐOẠN - Phase: TKTC	KÝ HIỆU BẢN VẼ - Drawing No: KC-07
TỶ LỆ - Scale: 1:25	HOÀN THÀNH - Finish: 03/11/2026

DẦM SÀN TUM								
SỐ HIỆU	HÌNH DẠNG	Ø (mm)	DÀI 1 THANH (mm)	SỐ THANH/CK	SỐ CK	TỔNG SỐ THANH	TỔNG DÀI (m)	KHỐI LƯỢNG (kg)
DT.2-1	Thép dưới chạy suốt, neo 30d	25	6300	3	6	18	113,40	437,50
DT.2-2	Thép trên tại gối, dài L/3	20	2200	4	6	24	52,80	130,37
DT.2-3	Thép trên giữa nhịp (cấu tạo), nối 40d	12	2560	2	6	12	30,72	27,31
DT.2-4	Đai dầm Ø8a100/250	8	1160	35	6	210	243,60	96,24
DT.1-1	Thép dưới chạy suốt, neo 30d	16	19400	2	2	4	77,60	122,63
DT.1-2	Thép trên tại gối, dài L/3	18	2158	12	2	24	51,79	103,58
DT.1-3	Thép trên giữa nhịp (cấu tạo), nối 40d	12	2147	10	2	20	42,94	38,17
DT.1-4	Đai dầm Ø6a200/300	6	1350	85	2	170	229,50	51,00
Ø6								51,00
Ø8								96,24
Ø12								65,48
Ø16								122,63
Ø18								103,58
Ø20								130,37
Ø25								437,50
TỔNG CỘNG								1006,79

DẦM SÀN MÁI								
SỐ HIỆU	HÌNH DẠNG	Ø (mm)	DÀI 1 THANH (mm)	SỐ THANH/CK	SỐ CK	TỔNG SỐ THANH	TỔNG DÀI (m)	KHỐI LƯỢNG (kg)
DM.2-1	Thép dưới chạy suốt, neo 30d	12	3220	2	2	4	12,88	11,45
DM.2-2	Thép trên tại gối, dài L/3	12	1193	4	2	8	9,54	8,48
DM.2-3	Thép trên giữa nhịp (cấu tạo), nối 40d	12	1793	2	2	4	7,17	6,38
DM.2-4	Đai dầm Ø6a100/150	6	950	24	2	48	45,60	10,13
DM.1-1	Thép dưới chạy suốt, neo 30d	12	4520	2	2	4	18,08	16,07
DM.1-2	Thép trên tại gối, dài L/3	12	1627	4	2	8	13,02	11,57
DM.1-3	Thép trên giữa nhịp (cấu tạo), nối 40d	12	2227	2	2	4	8,91	7,92
DM.1-4	Đai dầm Ø6a150/200	6	1050	25	2	50	52,50	11,67
Ø6								21,80
Ø12								61,87
TỔNG CỘNG								83,67

SÀN TẦNG 2 (theo cấu tạo)								
SỐ HIỆU	HÌNH DẠNG	Ø (mm)	DÀI 1 THANH (mm)	SỐ THANH/CK	SỐ CK	TỔNG SỐ THANH	TỔNG DÀI (m)	KHỐI LƯỢNG (kg)
STẦNG2-1	Thép lớp dưới phương X Ø8a200	8	5000	93	1	93	465,00	183,70
STẦNG2-2	Thép lớp dưới phương Y Ø8a200	8	3760	125	1	125	470,00	185,68
STẦNG2-3	Thép mũ trên dầm, dài L/4 Ø8a200	8	1040	436	1	436	453,44	179,14
Ø8								548,52
TỔNG CỘNG								548,52

SÀN TẦNG 3 (theo cấu tạo)								
SỐ HIỆU	HÌNH DẠNG	Ø (mm)	DÀI 1 THANH (mm)	SỐ THANH/CK	SỐ CK	TỔNG SỐ THANH	TỔNG DÀI (m)	KHỐI LƯỢNG (kg)
STẦNG3-1	Thép lớp dưới phương X Ø8a200	8	5000	93	1	93	465,00	183,70
STẦNG3-2	Thép lớp dưới phương Y Ø8a200	8	3760	125	1	125	470,00	185,68
STẦNG3-3	Thép mũ trên dầm, dài L/4 Ø8a200	8	1040	436	1	436	453,44	179,14
Ø8								548,52
TỔNG CỘNG								548,52

SÀN TUM (theo cấu tạo)								
SỐ HIỆU	HÌNH DẠNG	Ø (mm)	DÀI 1 THANH (mm)	SỐ THANH/CK	SỐ CK	TỔNG SỐ THANH	TỔNG DÀI (m)	KHỐI LƯỢNG (kg)
STUM-1	Thép lớp dưới phương X Ø8a200	8	5000	93	1	93	465,00	183,70
STUM-2	Thép lớp dưới phương Y Ø8a200	8	3760	125	1	125	470,00	185,68
STUM-3	Thép mũ trên dầm, dài L/4 Ø8a200	8	1040	436	1	436	453,44	179,14
Ø8								548,52
TỔNG CỘNG								548,52

SÀN MÁI (theo cấu tạo)								
SỐ HIỆU	HÌNH DẠNG	Ø (mm)	DÀI 1 THANH (mm)	SỐ THANH/CK	SỐ CK	TỔNG SỐ THANH	TỔNG DÀI (m)	KHỐI LƯỢNG (kg)
SMÁI-1	Thép lớp dưới phương X Ø8a200	8	2700	20	1	20	54,00	21,33
SMÁI-2	Thép lớp dưới phương Y Ø8a200	8	4000	13	1	13	52,00	20,54
SMÁI-3	Thép mũ trên dầm, dài L/4 Ø8a200	8	775	66	1	66	51,15	20,21
Ø8								62,08
TỔNG CỘNG								62,08

CẦU THANG (theo cấu tạo)								
SỐ HIỆU	HÌNH DẠNG	Ø (mm)	DÀI 1 THANH (mm)	SỐ THANH/CK	SỐ CK	TỔNG SỐ THANH	TỔNG DÀI (m)	KHỐI LƯỢNG (kg)
CT1.1	Thép chịu lực bản thang Ø10a150	10	3792	8	1	8	30,34	18,73
CT1.2	Thép phân bố bản thang Ø6a200	6	1095	16	1	16	17,52	3,89
CT1.3	Thép chịu lực bản thang Ø10a150	10	3483	8	1	8	27,86	17,20
CT1.4	Thép phân bố bản thang Ø6a200	6	1095	15	1	15	16,43	3,65
CT1.5	Thép chiếu nghỉ 2 phương Ø8a200	8	1938	18	1	18	34,88	13,78
CT2.1	Thép chịu lực bản thang Ø10a150	10	3706	8	1	8	29,65	18,30
CT2.2	Thép phân bố bản thang Ø6a200	6	1095	16	1	16	17,52	3,89
CT2.3	Thép chịu lực bản thang Ø10a150	10	3372	8	1	8	26,98	16,65
CT2.4	Thép phân bố bản thang Ø6a200	6	1095	14	1	14	15,33	3,41
CT2.5	Thép chiếu nghỉ 2 phương Ø8a200	8	1938	18	1	18	34,88	13,78
CT3.1	Thép chịu lực bản thang Ø10a150	10	3706	8	1	8	29,65	18,30
CT3.2	Thép phân bố bản thang Ø6a200	6	1095	16	1	16	17,52	3,89
CT3.3	Thép chịu lực bản thang Ø10a150	10	3372	8	1	8	26,98	16,65
CT3.4	Thép phân bố bản thang Ø6a200	6	1095	14	1	14	15,33	3,41
CT3.5	Thép chiếu nghỉ 2 phương Ø8a200	8	1938	18	1	18	34,88	13,78
Ø6								22,14
Ø8								41,34
Ø10								105,83
TỔNG CỘNG								169,32

BẢNG THỐNG KÊ CỐT THÉP (2/2)

GHI CHÚ: NHÀ THẦU THI CÔNG KIỂM TRA KÍCH THƯỚC THỰC TẾ, NẾU THẤY CÓ XUNG ĐỘT CẦN BÁO LẠI CHO THIẾT KẾ VÀ QUẢN LÝ KỸ THUẬT.

LẦN NỘP	NỘI DUNG ĐIỀU CHỈNH	NGÀY NỘP
1		
2		
3		
4		

GHI CHÚ - Note:

CHỦ ĐẦU TƯ - Client:
CHỦ ĐẦU TƯ (MẪU)

DỰ ÁN - Project:
NHÀ PHỐ 5x18m, 3 TẦNG + TUM
Mẫu minh họa

HẠNG MỤC - Item:
KẾT CẤU

TƯ VẤN THIẾT KẾ - Consultant:
AUTOCAD MCP

CHỦ NHIỆM TK - Chief of Project	
CHỦ TRÌ TK - Chief of Division	
THIẾT KẾ - Designed by: AutoCAD MCP	
KIỂM TRA - Checked by: ...	

TÊN BẢN VẼ - Drawing name:
BẢNG THỐNG KÊ CỐT THÉP (2/2)

SỐ HĐ - Contract No:	PHIÊN BẢN - Version: 01
GIAI ĐOẠN - Phase: TKTC	KÝ HIỆU BẢN VẼ - Drawing No: KC-08
TỶ LỆ - Scale: 1:25	HOÀN THÀNH - Finish: 03/11/2026

BẢNG TỔNG HỢP KHỐI LƯỢNG VẬT TƯ				
STT	HẠNG MỤC CÔNG VIỆC	ĐƠN VỊ	KHỐI LƯỢNG	DIỄN GIẢI
	I. PHẦN MÓNG			
1	Bê tông lót móng đá 4x6 B7.5, dày 100	m³	2,352	12 x 1,40 x 1,40 x 0,1
2	Bê tông lót giằng móng B7.5, dày 100	m³	2,435	60,88 x 0,40 x 0,1
3	Bê tông móng M1 B20	m³	6,912	12 x 1,20 x 1,20 x 0,40
4	Bê tông cổ cột (dưới cốt ±0.000) B20	m³	0,639	12 x 0,22 x 0,22 x 1,10
5	Bê tông giằng móng B20	m³	4,87	6 x 4,58 x 0,20 x 0,40 + 2 x 16,70 x 0,20 x 0,40
6	Ván khuôn móng	m²	23,04	12 x 2 x (1,20 + 1,20) x 0,40
7	Ván khuôn giằng móng	m²	48,704	60,88 x 2 x 0,40
8	Ván khuôn cổ cột	m²	11,616	12 x 2 x (0,22 + 0,22) x 1,10
	II. PHẦN THÂN			
9	Bê tông cột đến sàn TẦNG 2 B20	m³	2,091	12 x 0,22 x 0,22 x 3,60
10	Ván khuôn cột đến sàn TẦNG 2	m²	38,016	12 x 2 x (0,22 + 0,22) x 3,60
11	Bê tông cột đến sàn TẦNG 3 B20	m³	1,917	12 x 0,22 x 0,22 x 3,30
12	Ván khuôn cột đến sàn TẦNG 3	m²	34,848	12 x 2 x (0,22 + 0,22) x 3,30
13	Bê tông cột đến sàn TUM B20	m³	1,917	12 x 0,22 x 0,22 x 3,30
14	Ván khuôn cột đến sàn TUM	m²	34,848	12 x 2 x (0,22 + 0,22) x 3,30
15	Bê tông cột đến sàn MÁI B20	m³	0,565	4 x 0,22 x 0,22 x 2,92
16	Ván khuôn cột đến sàn MÁI	m²	10,278	4 x 2 x (0,22 + 0,22) x 2,92
17	Bê tông dầm sàn TẦNG 2 (phần dưới sàn) B20	m³	4,077	6 x 4,58 x 0,20 x 0,28 + 2 x 16,70 x 0,20 x 0,38
18	Bê tông sàn TẦNG 2 dày 120 B20	m³	9,209	76,75 x 0,12
19	Ván khuôn dầm, sàn TẦNG 2	m²	117,518	76,75 + 6 x 4,58 x 2 x 0,28 + 2 x 16,70 x 2 x 0,38
20	Bê tông dầm sàn TẦNG 3 (phần dưới sàn) B20	m³	4,077	6 x 4,58 x 0,20 x 0,28 + 2 x 16,70 x 0,20 x 0,38
21	Bê tông sàn TẦNG 3 dày 120 B20	m³	9,209	76,75 x 0,12
22	Ván khuôn dầm, sàn TẦNG 3	m²	117,518	76,75 + 6 x 4,58 x 2 x 0,28 + 2 x 16,70 x 2 x 0,38
23	Bê tông dầm sàn TUM (phần dưới sàn) B20	m³	4,077	6 x 4,58 x 0,20 x 0,28 + 2 x 16,70 x 0,20 x 0,38
24	Bê tông sàn TUM dày 120 B20	m³	9,209	76,75 x 0,12
25	Ván khuôn dầm, sàn TUM	m²	117,518	76,75 + 6 x 4,58 x 2 x 0,28 + 2 x 16,70 x 2 x 0,38
26	Bê tông dầm sàn MÁI (phần dưới sàn) B20	m³	0,494	2 x 2,28 x 0,20 x 0,18 + 2 x 3,58 x 0,20 x 0,23
27	Bê tông sàn MÁI dày 120 B20	m³	1,14	9,50 x 0,12
28	Ván khuôn dầm, sàn MÁI	m²	14,435	9,50 + 2 x 2,28 x 2 x 0,18 + 2 x 3,58 x 2 x 0,23
29	Bê tông bản thang, chiếu nghỉ dày 120 B20	m³	3,359	1,137 + 1,111 + 1,111
30	Cốt thép CB240-T, Ø ≤ 10	tấn	2,537	theo bảng thống kê cốt thép
31	Cốt thép CB300-V, Ø > 10	tấn	4,391	theo bảng thống kê cốt thép
	III. PHẦN XÂY, TRÁT			
32	Xây tường gạch dày 200 VXM M75 (đã trừ cửa)	m²	468,12	thể tích 93,62 m³
33	Xây tường gạch dày 100 VXM M75 (đã trừ cửa)	m²	175,296	thể tích 17,53 m³
34	Trát tường trong VXM M75 dày 15	m²	793,402	2 mặt tường trong, mặt trong tường bao
35	Trát tường ngoài VXM M75 dày 15	m²	493,43	mặt ngoài tường bao, 2 mặt tường mái
36	Trát trần, dầm VXM M75 dày 15	m²	366,989	đáy sàn và thành dầm

TỔNG HỢP THÉP THEO ĐƯỜNG KÍNH	
ĐƯỜNG KÍNH	KHỐI LƯỢNG (kg)
Ø6	585,55
Ø8	1845,22
Ø10	105,83
Ø12	604,54
Ø14	122,83
Ø16	1387,84
Ø18	260,38
Ø20	521,49
Ø22	472,8
Ø25	1020,84
Ø ≤ 10 (CB240-T)	2536,6
Ø > 10 (CB300-V)	4390,72
TỔNG CỘNG	6927,32

Khối lượng lấy theo bảng tính sơ bộ, dùng để lập dự toán: kỹ sư dự toán kiểm tra lại theo bản vẽ thi công (chiều dài theo trục, chưa trừ phần giao nhau, cột trong tường).

BẢNG TỔNG HỢP KHỐI LƯỢNG VẬT TƯ

GHI CHÚ:NHÀ THẦU THI CÔNG KIỂM TRA KÍCH THƯỚC THỰC TẾ, NẾU THẤY CÓ XUNG ĐỘT CẦN BÁO LẠI CHO THIẾT KẾ VÀ QUẢN LÝ KỸ THUẬT.

LẦN NỘP	NỘI DUNG ĐIỀU CHỈNH	NGÀY NỘP
1		
2		
3		
4		

GHI CHÚ - Note:

CHỦ ĐẦU TƯ - Client:
CHỦ ĐẦU TƯ (MẪU)

DỰ ÁN - Project:
NHÀ PHỐ 5x18m, 3 TẦNG + TUM
Mẫu minh họa

HẠNG MỤC - Item:
KẾT CẤU

TƯ VẤN THIẾT KẾ - Consultant:
AUTOCAD MCP

CHỦ NHIỆM TK - Chief of Project	
CHỦ TRÌ TK - Chief of Division	
THIẾT KẾ - Designed by AutoCAD MCP	
KIỂM TRA - Checked by ...	

TÊN BẢN VẼ - Drawing name:
BẢNG TỔNG HỢP KHỐI LƯỢNG VẬT TƯ

SỐ HĐ - Contract No:	PHIÊN BẢN - Version 01
GIAI ĐOẠN - Phase: TKTC	KÝ HIỆU BẢN VẼ - Drawing Na KC-09
TỶ LỆ - Scale: 1:25	HOÀN THÀNH - Finish: 03/11/2026