
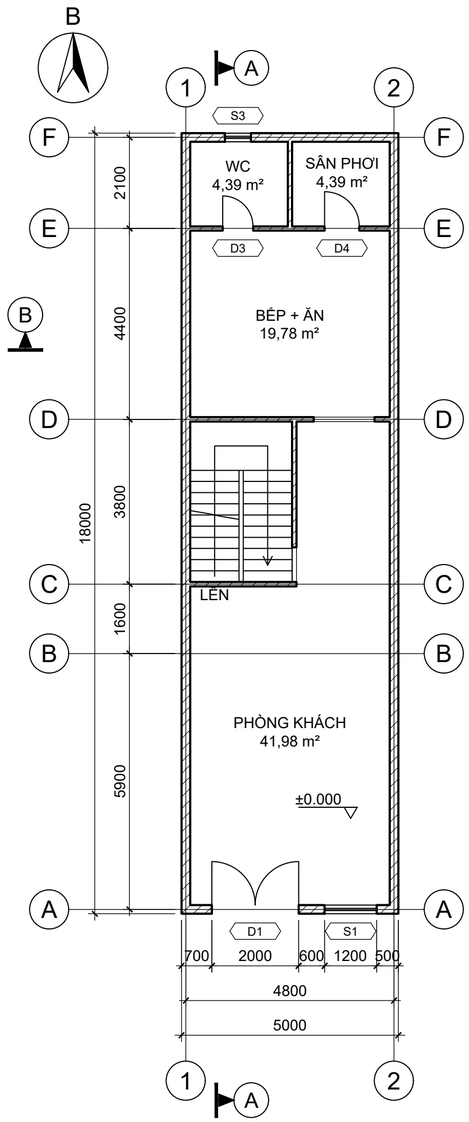


MẶT BẰNG TẦNG 1

TỶ LỆ: 1/100

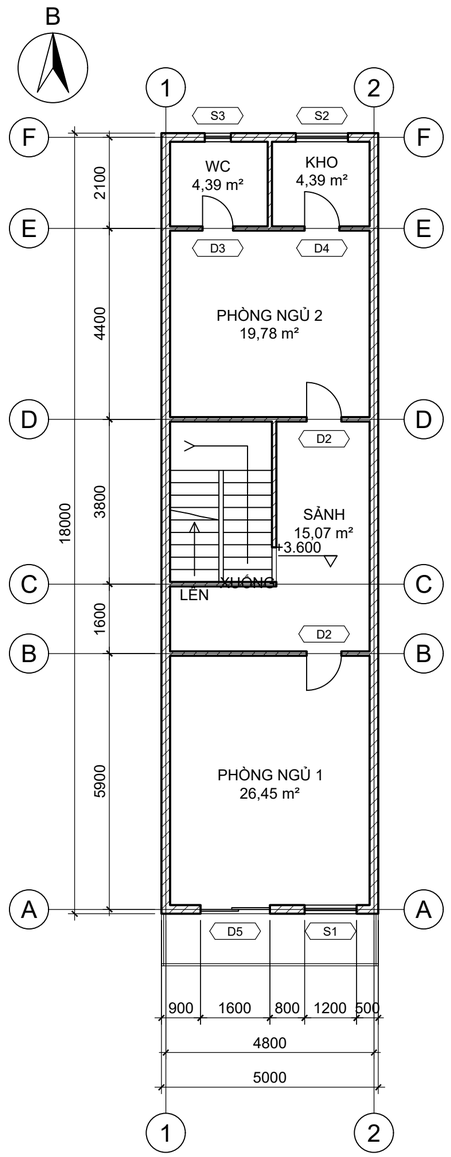

MẶT BẰNG TẦNG 2

TỶ LỆ: 1/100

LẦN NỘP	NỘI DUNG ĐIỀU CHỈNH	NGÀY NỘP
1		
2		
3		
4		

GHI CHÚ - Note:

CHỦ ĐẦU TƯ - Client:

CHỦ ĐẦU TƯ (MẪU)

DỰ ÁN - Project:

NHÀ PHỐ 5x18m, 3 TẦNG + TUM

Mẫu minh họa

HẠNG MỤC - Item:

KIẾN TRÚC, NỘI THẤT

TƯ VẤN THIẾT KẾ - Consultant:

AUTOCAD MCP


CHỦ NHIỆM TK - Chief of Project	
CHỦ TRÌ TK - Chief of Division	
THIẾT KẾ - Designed by AutoCAD MCP	
KIỂM TRA - Checked by ...	

TÊN BẢN VẼ - Drawing name:

MẶT BẰNG TẦNG 1, TẦNG 2


SỐ HĐ - Contract No:	PHIÊN BẢN - Version 01
GIAI ĐOẠN - Phase: TKTC	KÝ HIỆU BẢN VẼ - Drawing No KT-01
TỶ LỆ - Scale: 1:100	HOÀN THÀNH - Finish: 03/11/2026

GHI CHÚ: NHÀ THẦU THI CÔNG KIỂM TRA KÍCH THƯỚC THỰC TẾ, NẾU THẤY CÓ XUNG ĐỘT CẦN BÁO LẠI CHO THIẾT KẾ VÀ QUẢN LÝ KỸ THUẬT.

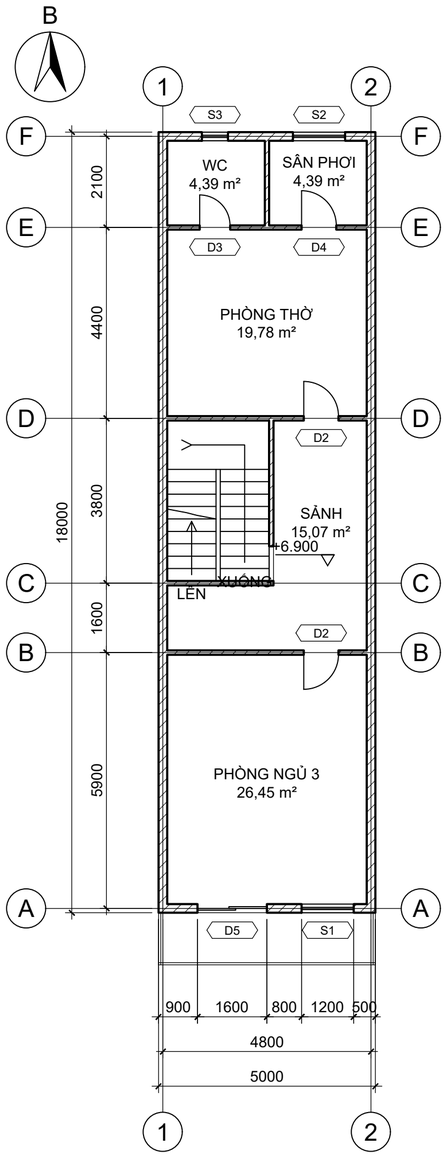

MẶT BẰNG TẦNG 3

TỶ LỆ: 1/100

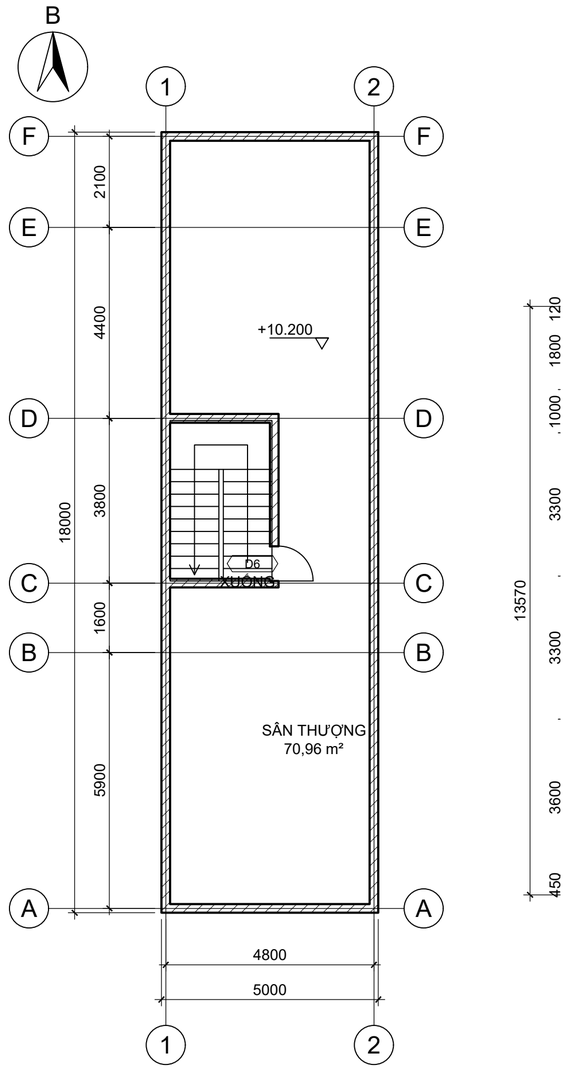

MẶT BẰNG TUM

TỶ LỆ: 1/100

MẶ

LẦN NỘP	NỘI DUNG ĐIỀU CHỈNH	NGÀY NỘP
1		
2		
3		
4		

GHI CHÚ - Note:

CHỦ ĐẦU TƯ - Client:

CHỦ ĐẦU TƯ (MẪU)

DỰ ÁN - Project:

NHÀ PHỐ 5x18m, 3 TẦNG + TUM

Mẫu minh họa

HẠNG MỤC - Item:

KIẾN TRÚC, NỘI THẤT

TƯ VẤN THIẾT KẾ - Consultant:

AUTOCAD MCP


CHỦ NHIỆM TK - Chief of Project	
CHỦ TRÌ TK - Chief of Division	
THIẾT KẾ - Designed by AutoCAD MCP	
KIỂM TRA - Checked by ...	

TÊN BẢN VẼ - Drawing name:

MẶT BẰNG TẦNG 3, TUM


SỐ HĐ - Contract No:	PHIÊN BẢN - Version 01
GIAI ĐOẠN - Phase: TKTC	KÝ HIỆU BẢN VẼ - Drawing No. KT-02
TỶ LỆ - Scale: 1:100	HOÀN THÀNH - Finish: 03/11/2026

GHI CHÚ:NHÀ THẦU THI CÔNG KIỂM TRA KÍCH THƯỚC THỰC TẾ, NẾU THẤY CÓ XUNG ĐỘT CẦN BÁO LẠI CHO THIẾT KẾ VÀ QUẢN LÝ KỸ THUẬT.

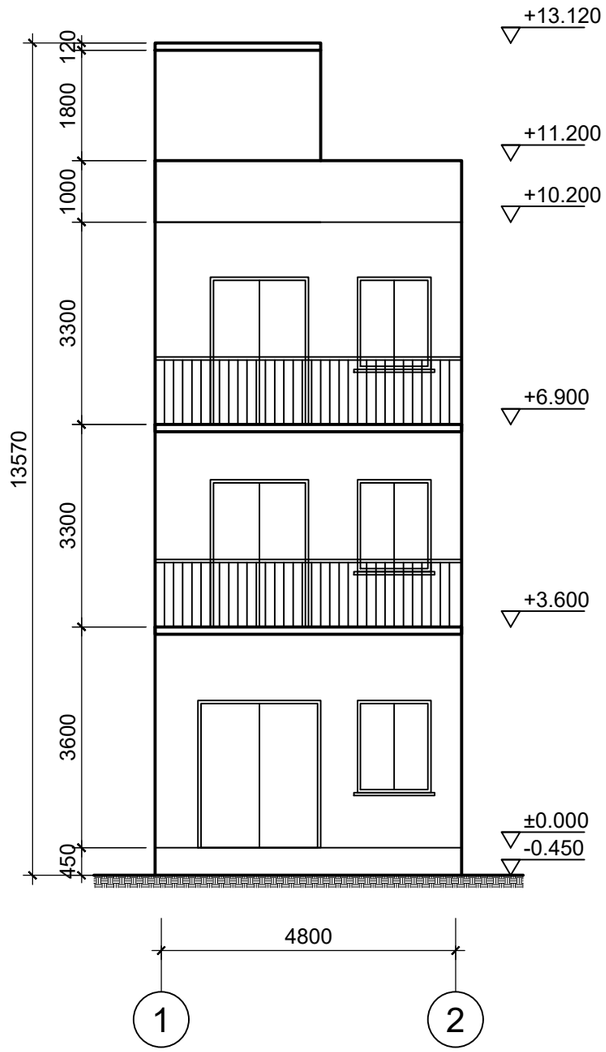

MẶT ĐỨNG CHÍNH (TRỤC A)

TỶ LỆ: 1/100

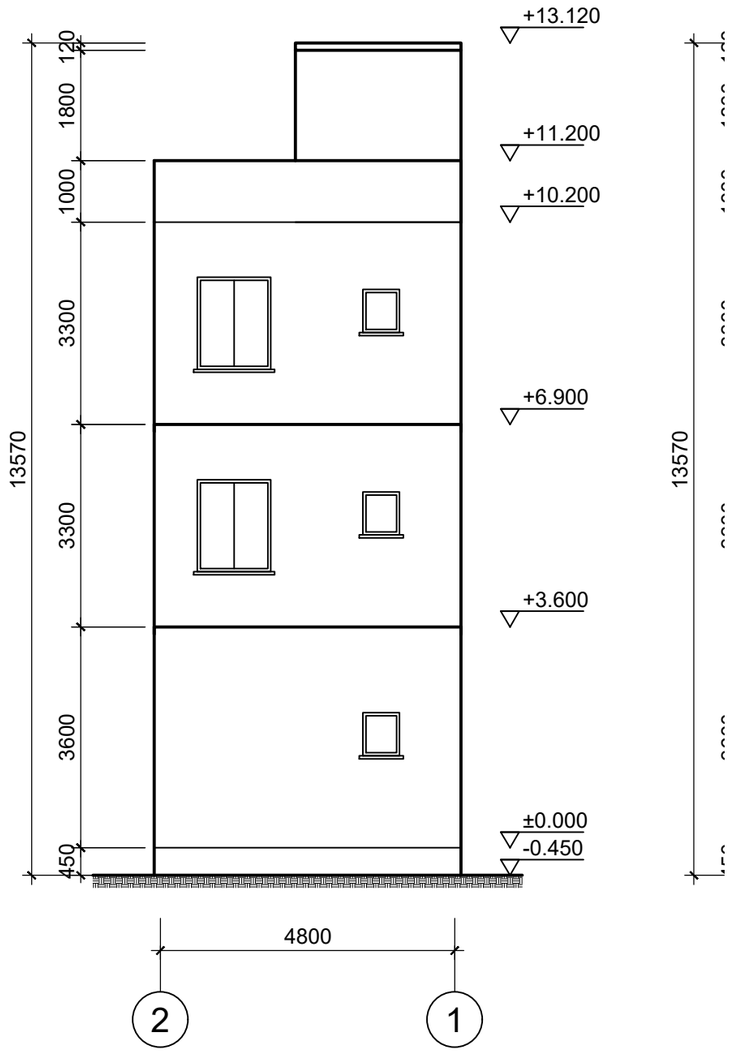

MẶT ĐỨNG SAU (TRỤC F)

TỶ LỆ: 1/100

GHI CHÚ:NHÀ THẦU THI CÔNG KIỂM TRA KÍCH THƯỚC THỰC TẾ, NẾU THẤY CÓ XUNG ĐỘT CẦN BÁO LẠI CHO THIẾT KẾ VÀ QUẢN LÝ KỸ THUẬT.

LẦN NỘP	NỘI DUNG ĐIỀU CHỈNH	NGÀY NỘP
1		
2		
3		
4		

GHI CHÚ - Note:

CHỦ ĐẦU TƯ - Client:

CHỦ ĐẦU TƯ (MẪU)

DỰ ÁN - Project:

NHÀ PHỐ 5x18m, 3 TẦNG + TUM

Mẫu minh họa

HẠNG MỤC - Item:

KIẾN TRÚC, NỘI THẤT

TƯ VẤN THIẾT KẾ - Consultant:


AUTOCAD MCP

CHỦ NHIỆM TK - Chief of Project	
CHỦ TRÌ TK - Chief of Division	
THIẾT KẾ - Designed by AutoCAD MCP	
KIỂM TRA - Checked by ...	

TÊN BẢN VẼ - Drawing name:

MẶT ĐỨNG CHÍNH, MẶT ĐỨNG SAU

SỐ HĐ - Contract No:	PHIÊN BẢN - Version 01
GIAI ĐOẠN - Phase: TKTC	KÝ HIỆU BẢN VẼ - Drawing No KT-03
TỶ LỆ - Scale: 1:100	HOÀN THÀNH - Finish: 03/11/2026

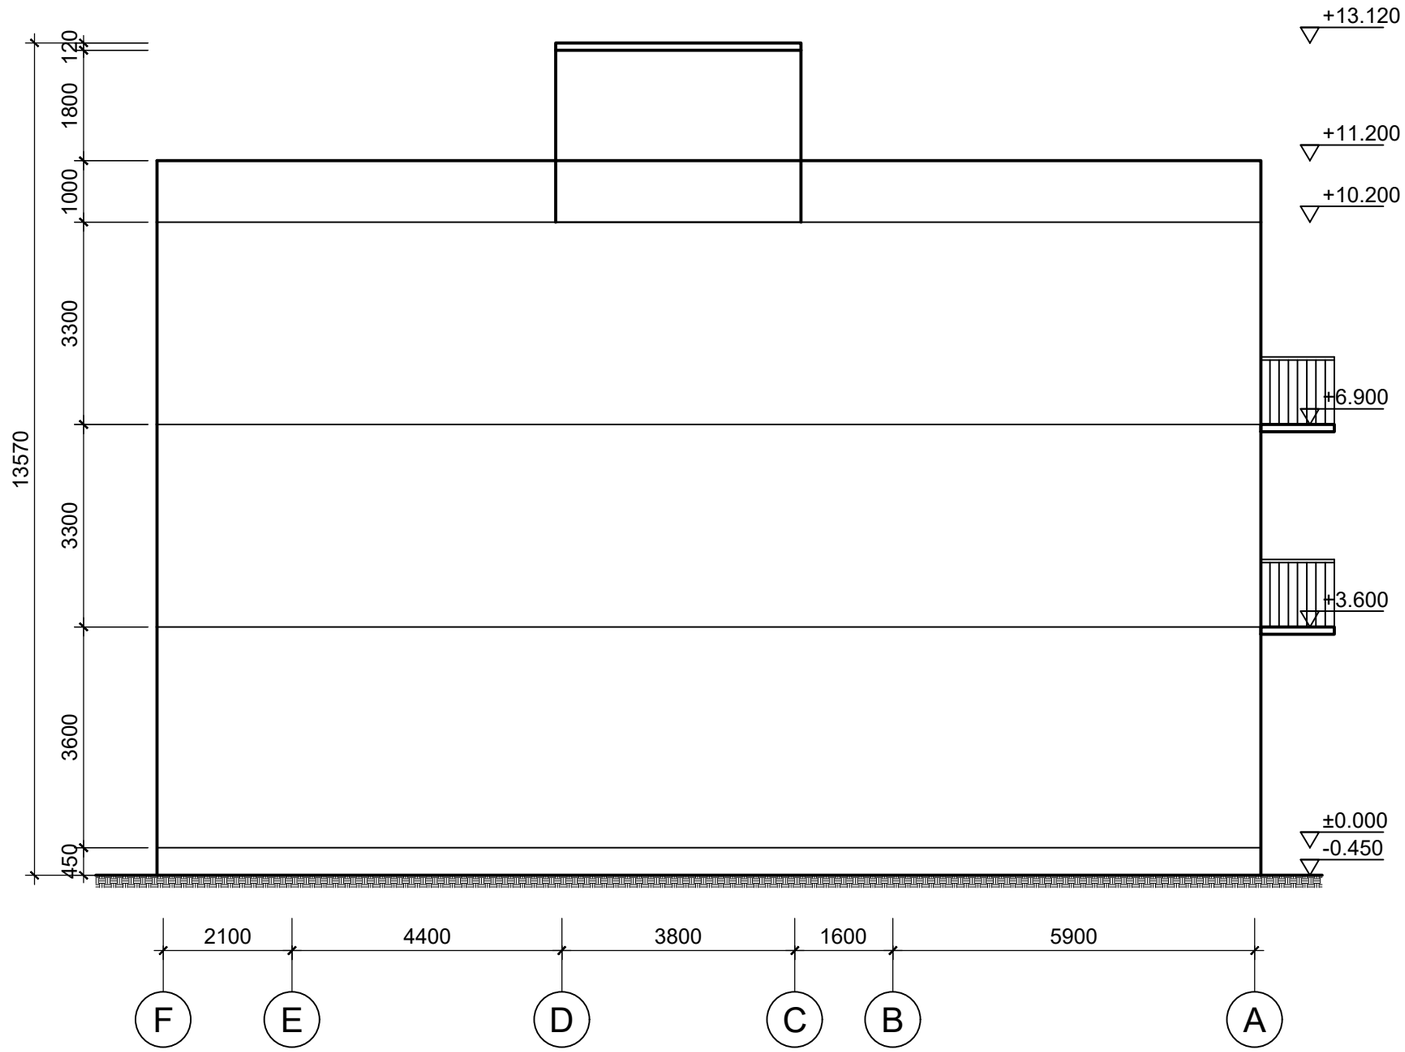

MẶT ĐỨNG TRỤC F-A

TỶ LỆ: 1/100

GHI CHÚ:NHÀ THẦU THI CÔNG KIỂM TRA KÍCH THƯỚC THỰC TẾ, NẾU THẤY CÓ XUNG ĐỘT CẦN BÁO LẠI CHO THIẾT KẾ VÀ QUẢN LÝ KỸ THUẬT.

LẦN NỘP	NỘI DUNG ĐIỀU CHỈNH	NGÀY NỘP
1		
2		
3		
4		

GHI CHÚ - Note:

CHỦ ĐẦU TƯ - Client:

CHỦ ĐẦU TƯ (MẪU)

DỰ ÁN - Project:

NHÀ PHỐ 5x18m, 3 TẦNG + TUM

Mẫu minh họa

HẠNG MỤC - Item:
KIẾN TRÚC, NỘI THẤT

TƯ VẤN THIẾT KẾ - Consultant:


AUTOCAD MCP

CHỦ NHIỆM TK - Chief of Project	
CHỦ TRÌ TK - Chief of Division	
THIẾT KẾ - Designed by AutoCAD MCP	
KIỂM TRA - Checked by ...	

TÊN BẢN VẼ - Drawing name:


MẶT ĐỨNG TRỤC F-A

SỐ HĐ - Contract No:	PHIÊN BẢN - Version 01
GIAI ĐOẠN - Phase: TKTC	KÝ HIỆU BẢN VẼ - Drawing No KT-04
TỶ LỆ - Scale: 1:100	HOÀN THÀNH - Finish: 03/11/2026

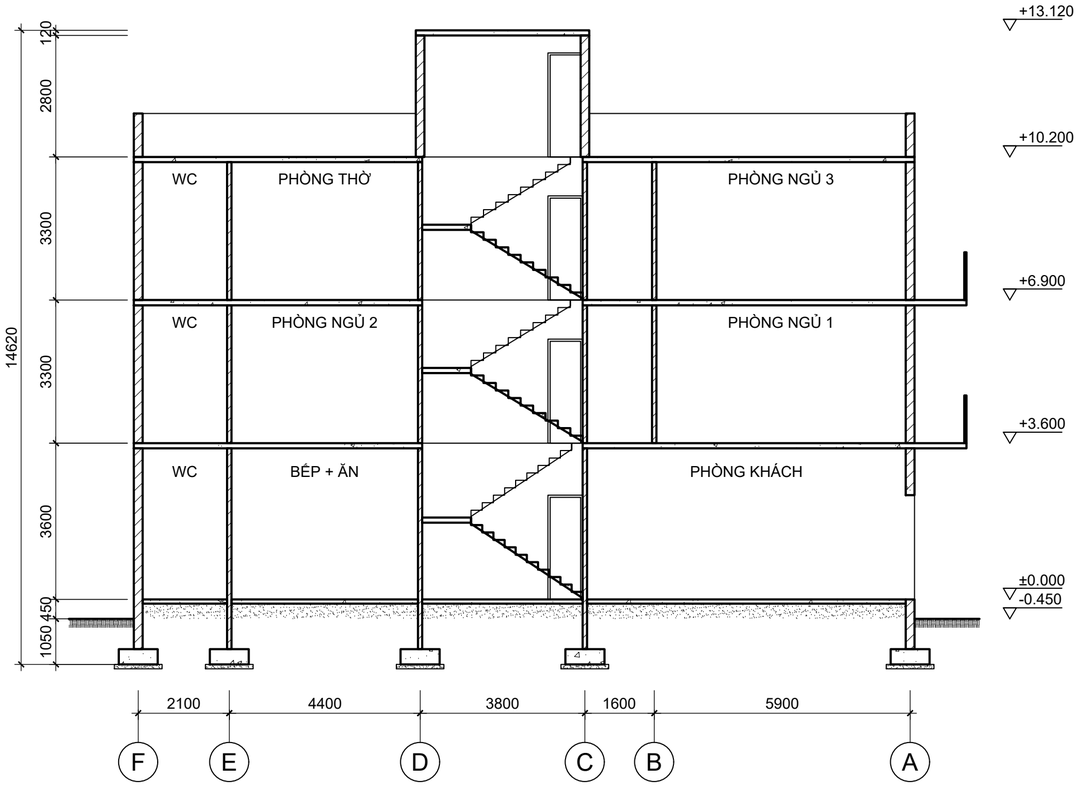

MẶT CẮT A-A

TỶ LỆ: 1/100

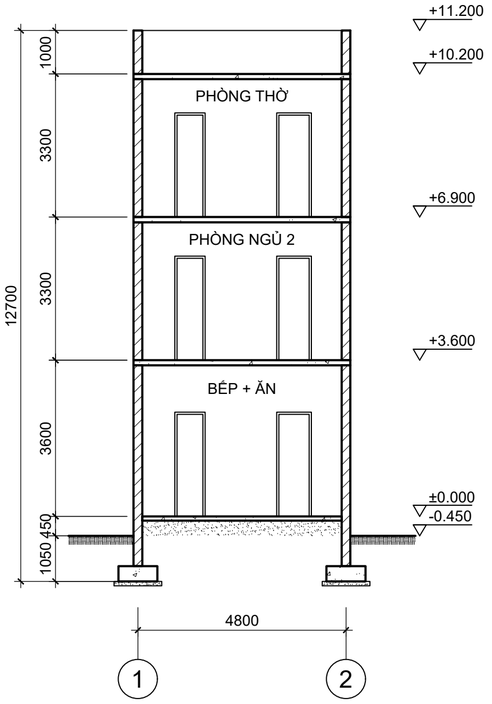

MẶT CẮT B-B

TỶ LỆ: 1/100

LẦN NỘP	NỘI DUNG ĐIỀU CHỈNH	NGÀY NỘP
1		
2		
3		
4		

GHI CHÚ - Note:

CHỦ ĐẦU TƯ - Client:

CHỦ ĐẦU TƯ (MẪU)

DỰ ÁN - Project:

NHÀ PHỐ 5x18m, 3 TẦNG + TUM

Mẫu minh họa

HẠNG MỤC - Item:

KIẾN TRÚC, NỘI THẤT

TƯ VẤN THIẾT KẾ - Consultant:

AUTOCAD MCP


CHỦ NHIỆM TK - Chief of Project	
CHỦ TRÌ TK - Chief of Division	
THIẾT KẾ - Designed by AutoCAD MCP	
KIỂM TRA - Checked by ...	

TÊN BẢN VẼ - Drawing name:

MẶT CẮT A-A, B-B

SỐ HĐ - Contract No:	PHIÊN BẢN - Version 01
GIAI ĐOẠN - Phase: TKTC	KÝ HIỆU BẢN VẼ - Drawing No KT-05
TỶ LỆ - Scale: 1:100	HOÀN THÀNH - Finish: 03/11/2026

GHI CHÚ:NHÀ THẦU THI CÔNG KIỂM TRA KÍCH THƯỚC THỰC TẾ, NẾU THẤY CÓ XUNG ĐỘT CẦN BÁO LẠI CHO THIẾT KẾ VÀ QUẢN LÝ KỸ THUẬT.

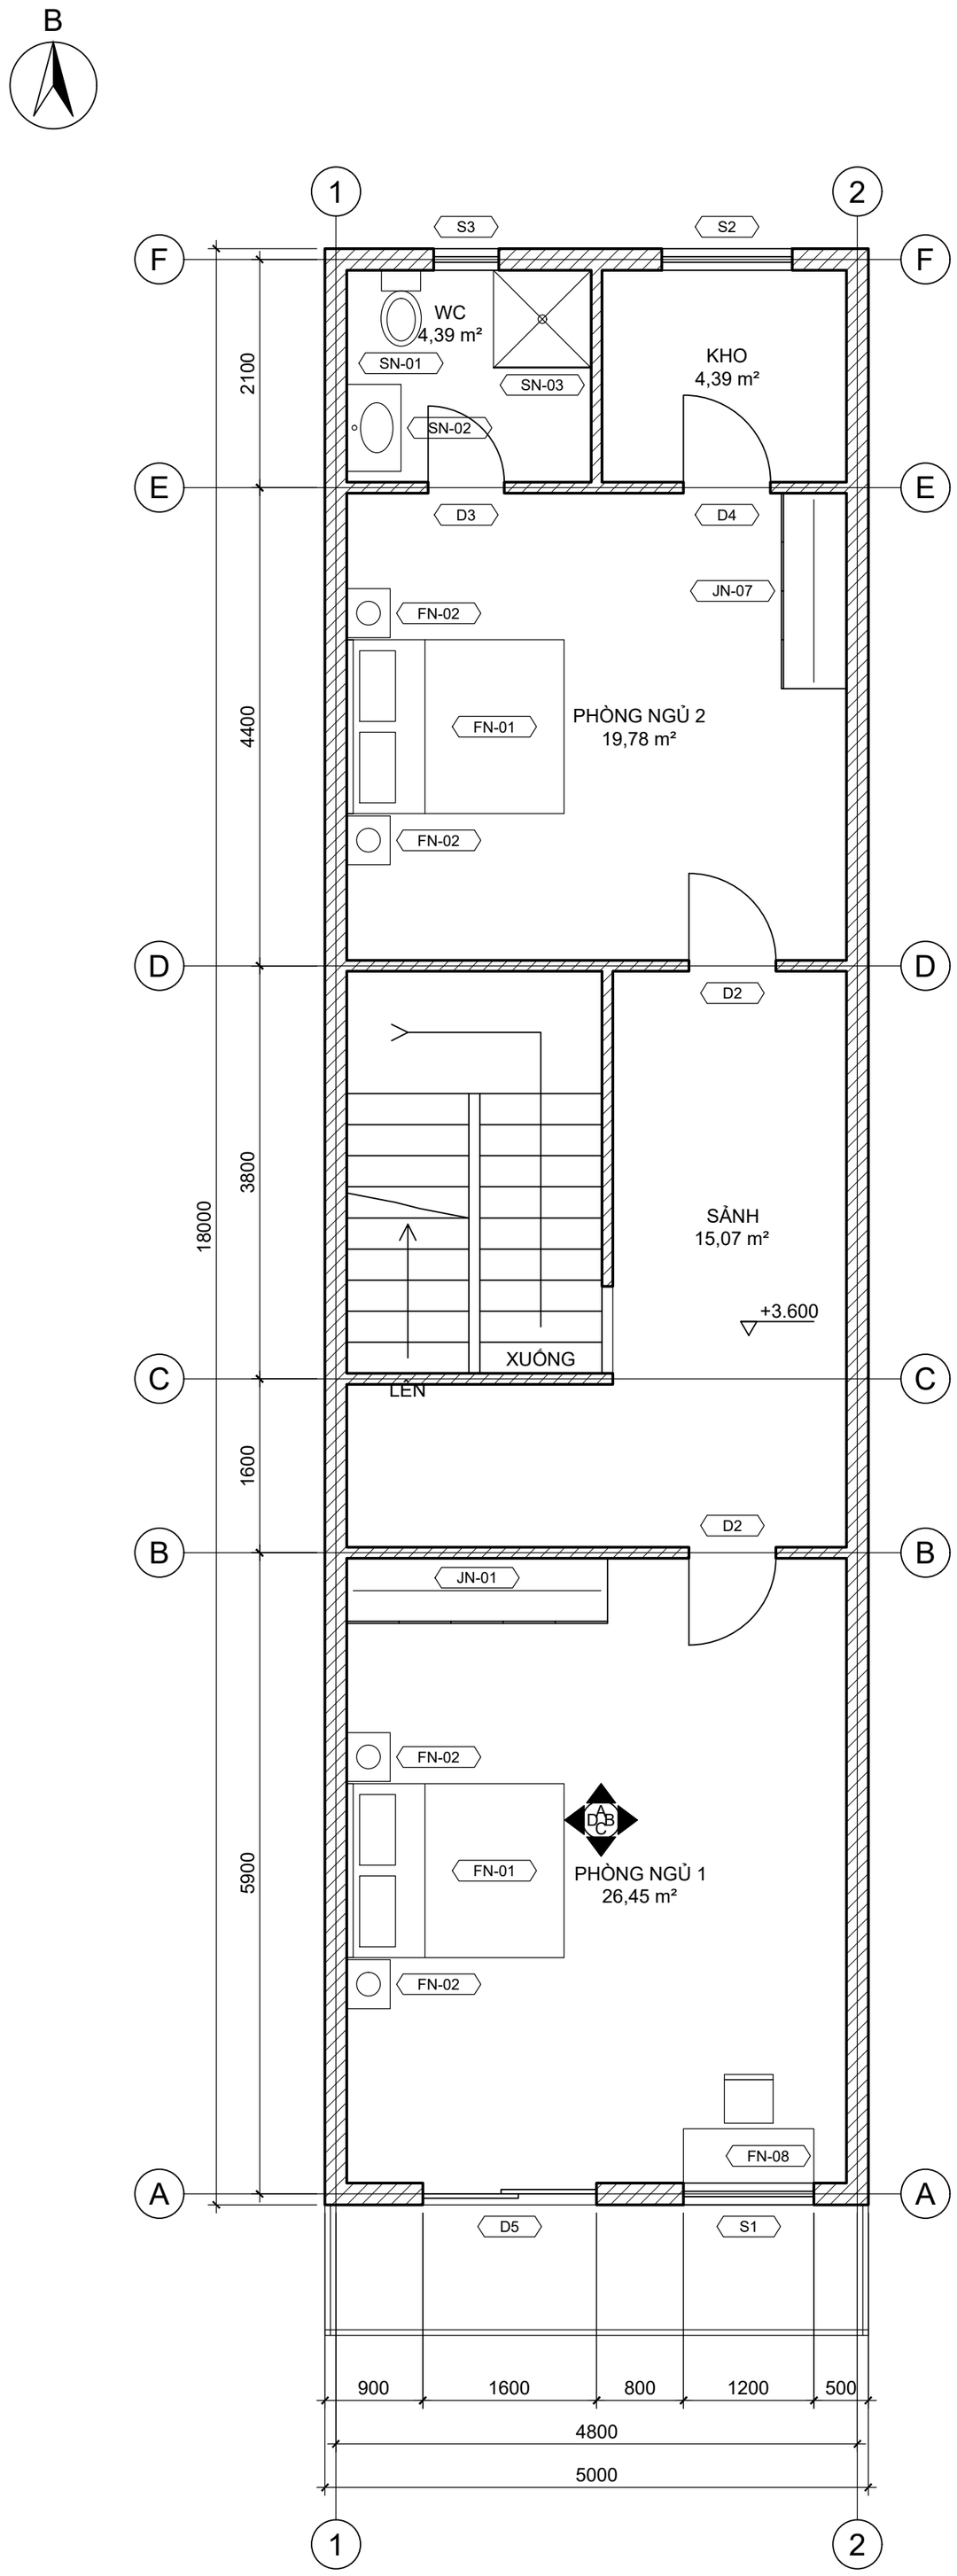


MẶT BẰNG BỐ TRÍ NỘI THẤT TẦNG 2

TỶ LỆ: 1/50

GHI CHÚ:

1. Kích thước ghi bằng mm, cao độ ghi bằng m, tính từ mặt sàn hoàn thiện của tầng.
2. Nhà thầu kiểm tra kích thước thực tế tại công trình trước khi thi công, báo lại thiết kế khi có sai khác.
3. Vật liệu theo mã trong bảng thống kê vật liệu hoàn thiện; mẫu vật liệu trình chủ đầu tư và thiết kế duyệt trước khi thi công.
4. Đồ rời (FN) thể hiện vị trí bố trí; đồ gỗ đóng tại chỗ (JN) theo bản vẽ chi tiết đồ gỗ.
5. Thiết bị vệ sinh (SN), thiết bị (EQ) lắp đặt theo hướng dẫn của nhà sản xuất; chờ sẵn cấp thoát nước, điện theo vị trí thiết bị.

AUTOCAD MCP			
CÔNG TRÌNH: NHÀ PHỐ 5x18m, 3 TẦNG + TUM		CHỦ ĐẦU TƯ: CHỦ ĐẦU TƯ (MẪU)	
TÊN BẢN VẼ: MẶT BẰNG BỐ TRÍ NỘI THẤT TẦNG 2			
TỶ LỆ: 1:50	NGÀY: 03/11/2026	THIẾT KẾ: AutoCAD MCP	KIỂM TRA: ...
SỐ BẢN VẼ: NT-01	LẦN SỬA: 01	TỜ:	

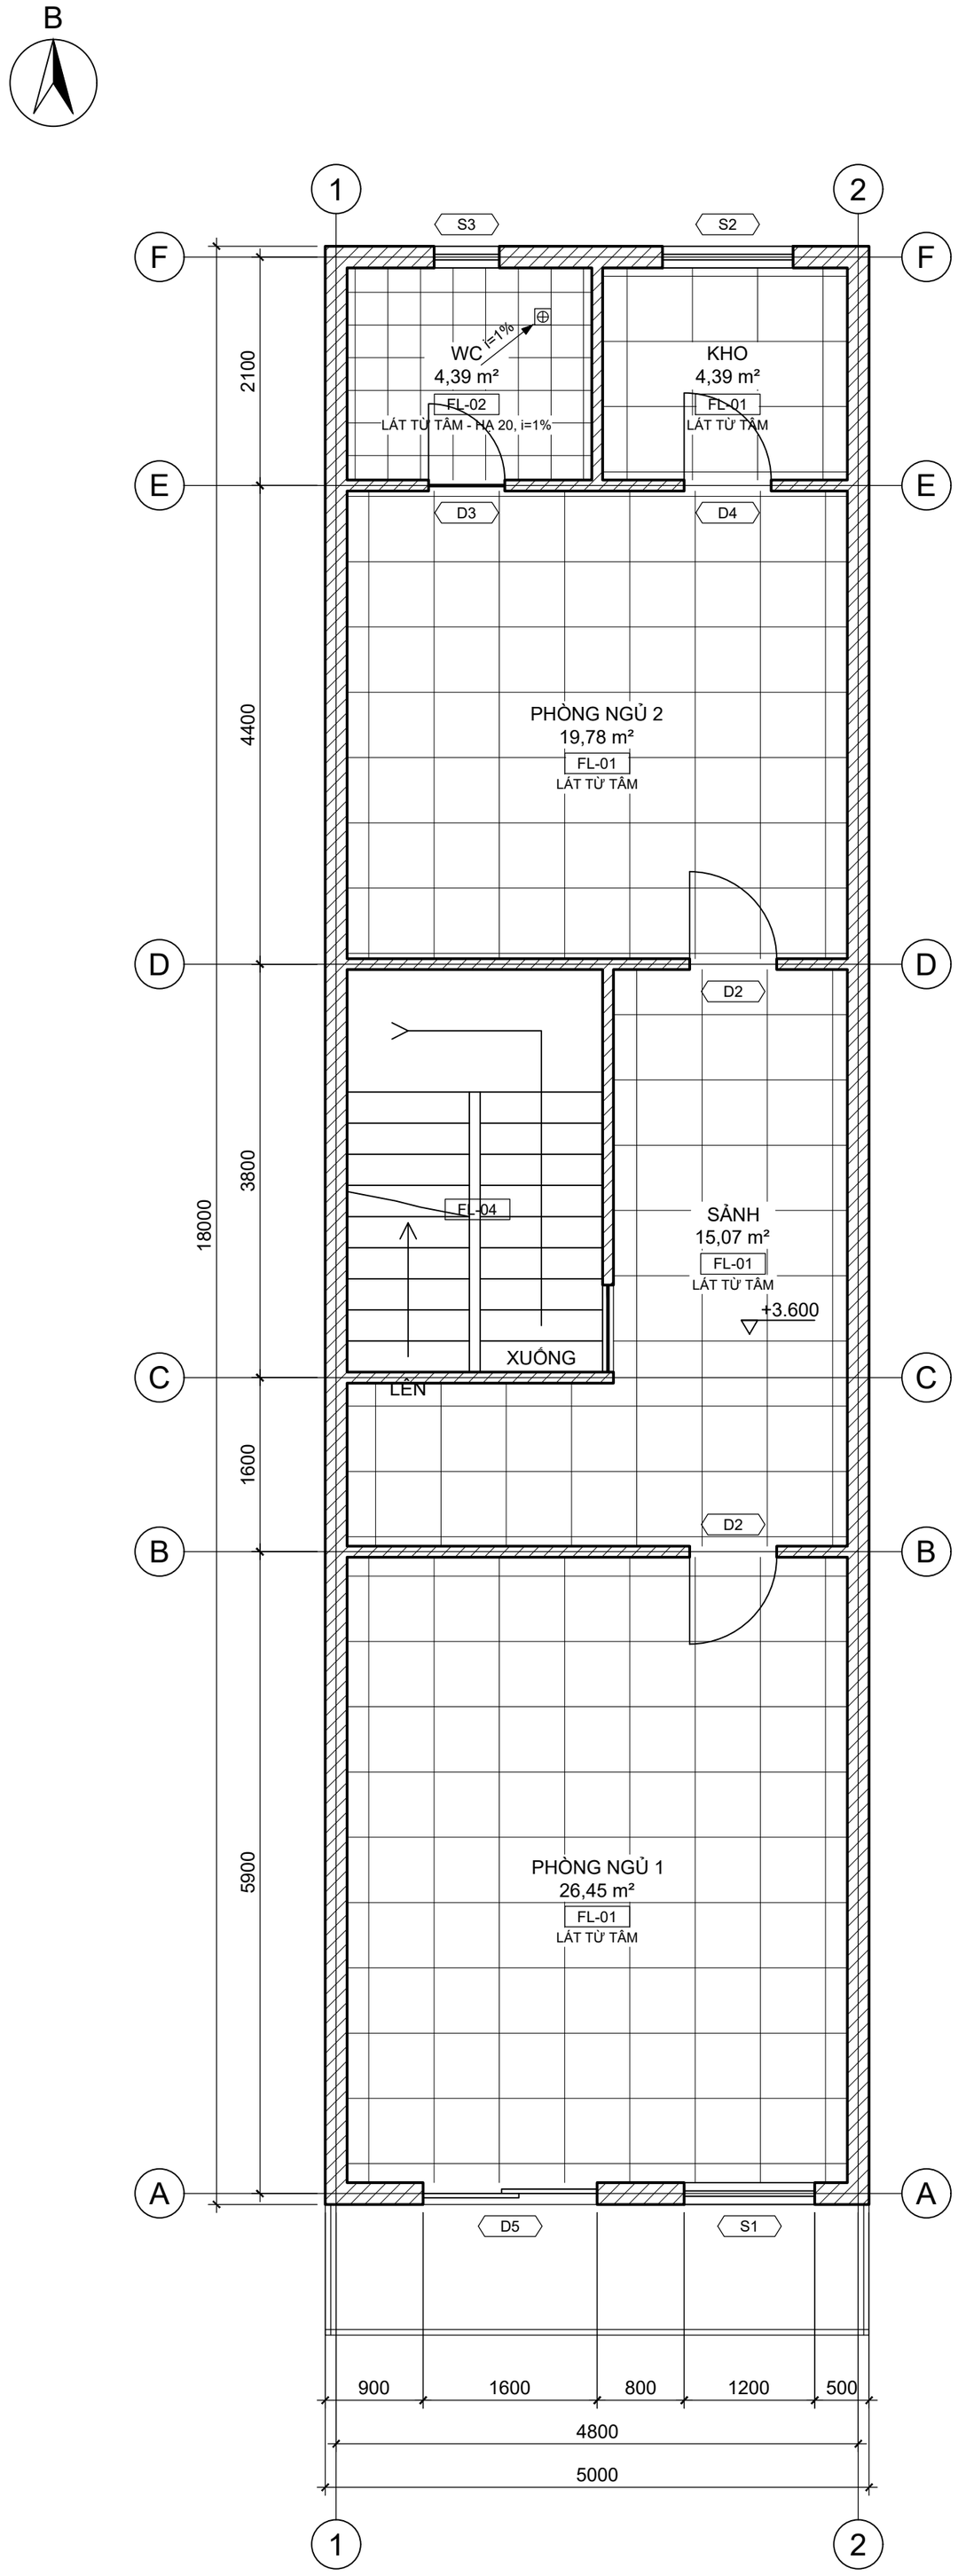

CHÚ THÍCH VẬT LIỆU SÀN

FL-01 Gạch porcelain 600x600
65,69 m² (PHÒNG NGỦ 1, SẢNH, PHÒNG NGỦ 2, KHO)

FL-04 Đá granite ốp bậc thang và chiếu nghỉ
8,70 m² (CẦU THANG)

FL-02 Gạch chống trơn 300x300
4,39 m² (WC)

Nẹp chuyển tiếp inox

Phễu thu sàn, dốc i=1% về phễu


GHI CHÚ:

1. Kích thước ghi bằng mm, cao độ ghi bằng m, tính từ mặt sàn hoàn thiện của tầng.
2. Nhà thầu kiểm tra kích thước thực tế tại công trình trước khi thi công, báo lại thiết kế khi có sai khác.
3. Vật liệu theo mã trong bảng thống kê vật liệu hoàn thiện; mẫu vật liệu trình chủ đầu tư và thiết kế duyệt trước khi thi công.
4. Gạch lát mạch 2 mm, keo chà ron màu theo mẫu duyệt; lát từ tâm phòng (ghi LÁT TỪ TÂM) hoặc từ điểm ghi trên bản vẽ.
5. Sàn khu vệ sinh hạ 20 mm, sân và ban công hạ 50 mm so với sàn trong nhà; chống thấm trước khi lát, dốc i=1% về phễu thu.
6. Nẹp chuyển tiếp inox dưới cánh cửa tại vị trí thay đổi vật liệu hoặc cao độ sàn.

MẶT BẰNG HOÀN THIỆN SÀN TẦNG 2

TỶ LỆ: 1/50

AUTOCAD MCP			
CÔNG TRÌNH: NHÀ PHỐ 5x18m, 3 TẦNG + TUM		CHỦ ĐẦU TƯ: CHỦ ĐẦU TƯ (MẪU)	
TÊN BẢN VẼ: MẶT BẰNG HOÀN THIỆN SÀN TẦNG 2			
TỶ LỆ: 1:50	NGÀY: 03/11/2026	THIẾT KẾ: AutoCAD MCP	KIỂM TRA: ...
SỐ BẢN VẼ: NT-02		LẦN SỬA: 01	TỜ:

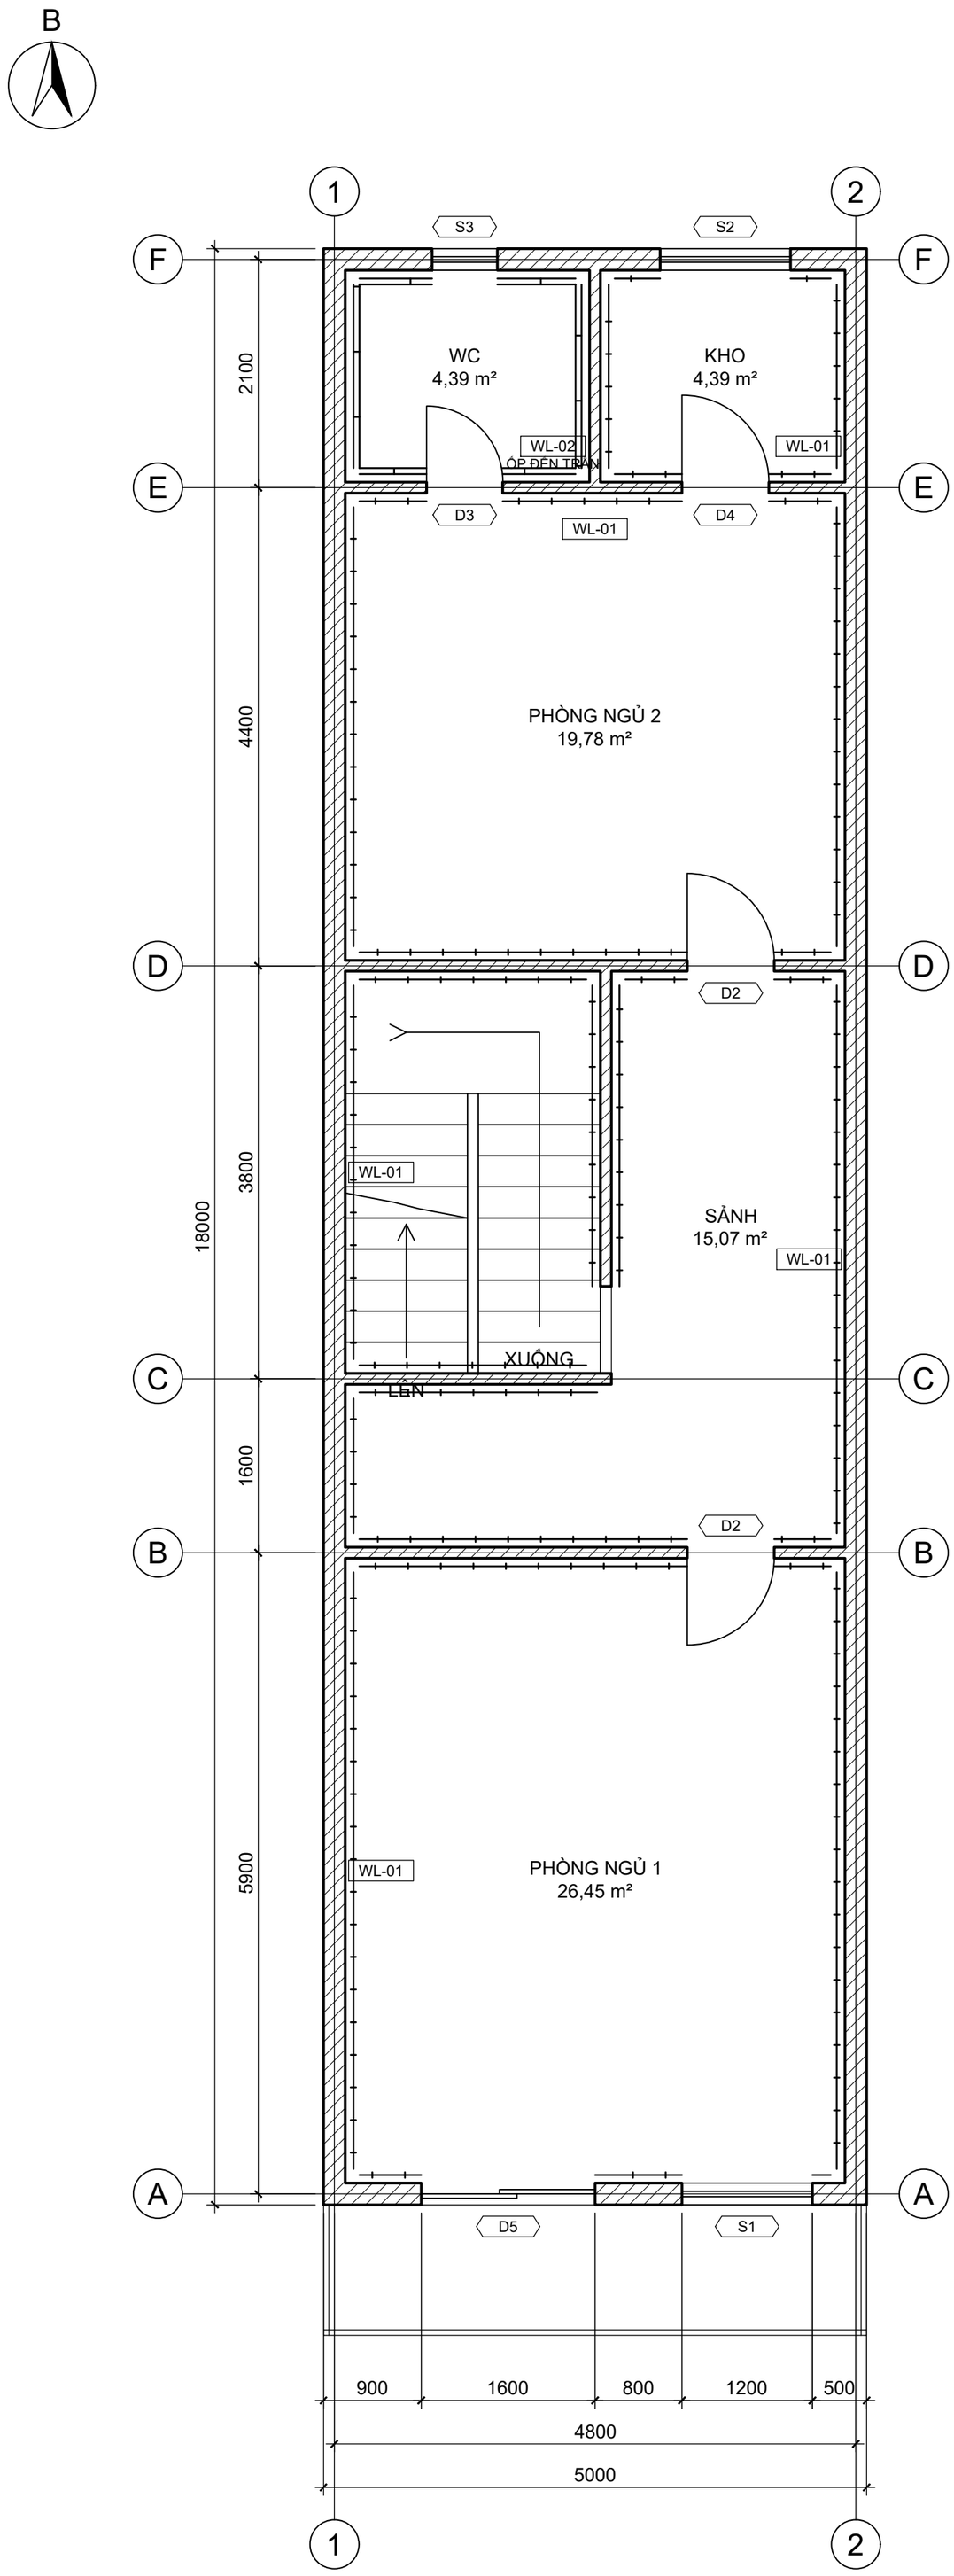

MẶT BẰNG HOÀN THIỆN TƯỜNG TẦNG 2

TỶ LỆ: 1/50

CHÚ THÍCH VẬT LIỆU TƯỜNG


WL-01 — Sơn nước hoàn thiện màu trắng
192,21 m² (PHÒNG NGỦ 1, SẢNH, CẦU THANG, PHÒNG NGỦ 2, KHO)

WL-02 — Gạch ốp tường 300x600 ốp đến trần
21,42 m² (WC)

GHI CHÚ:

1. Kích thước ghi bằng mm, cao độ ghi bằng m, tính từ mặt sàn hoàn thiện của tầng.
2. Nhà thầu kiểm tra kích thước thực tế tại công trình trước khi thi công, báo lại thiết kế khi có sai khác.
3. Vật liệu theo mã trong bảng thống kê vật liệu hoàn thiện; mẫu vật liệu trình chủ đầu tư và thiết kế duyệt trước khi thi công.
4. Tường sơn: bả matit 2 lớp, sơn lót kháng kiềm 1 lớp, sơn phủ 2 lớp theo mã màu duyệt.
5. Gạch ốp tường mạch 2 mm, ốp từ mặt sàn hoàn thiện; khu vệ sinh ốp đến trần, chống thấm chân tường cao 300 trước khi ốp.
6. Khu bếp ốp gạch từ mặt đá bếp đến đáy tủ bếp trên.

AUTOCAD MCP	
CÔNG TRÌNH: NHÀ PHỐ 5x18m, 3 TẦNG + TUM	CHỦ ĐẦU TƯ: CHỦ ĐẦU TƯ (MẪU)
TÊN BẢN VẼ: MẶT BẰNG HOÀN THIỆN TƯỜNG TẦNG 2	
TỶ LỆ: 1:50	NGÀY: 03/11/2026
THIẾT KẾ: AutoCAD MCP	KIỂM TRA: ...
SỐ BẢN VẼ: NT-03	LẦN SỬA: 01
TỜ:	

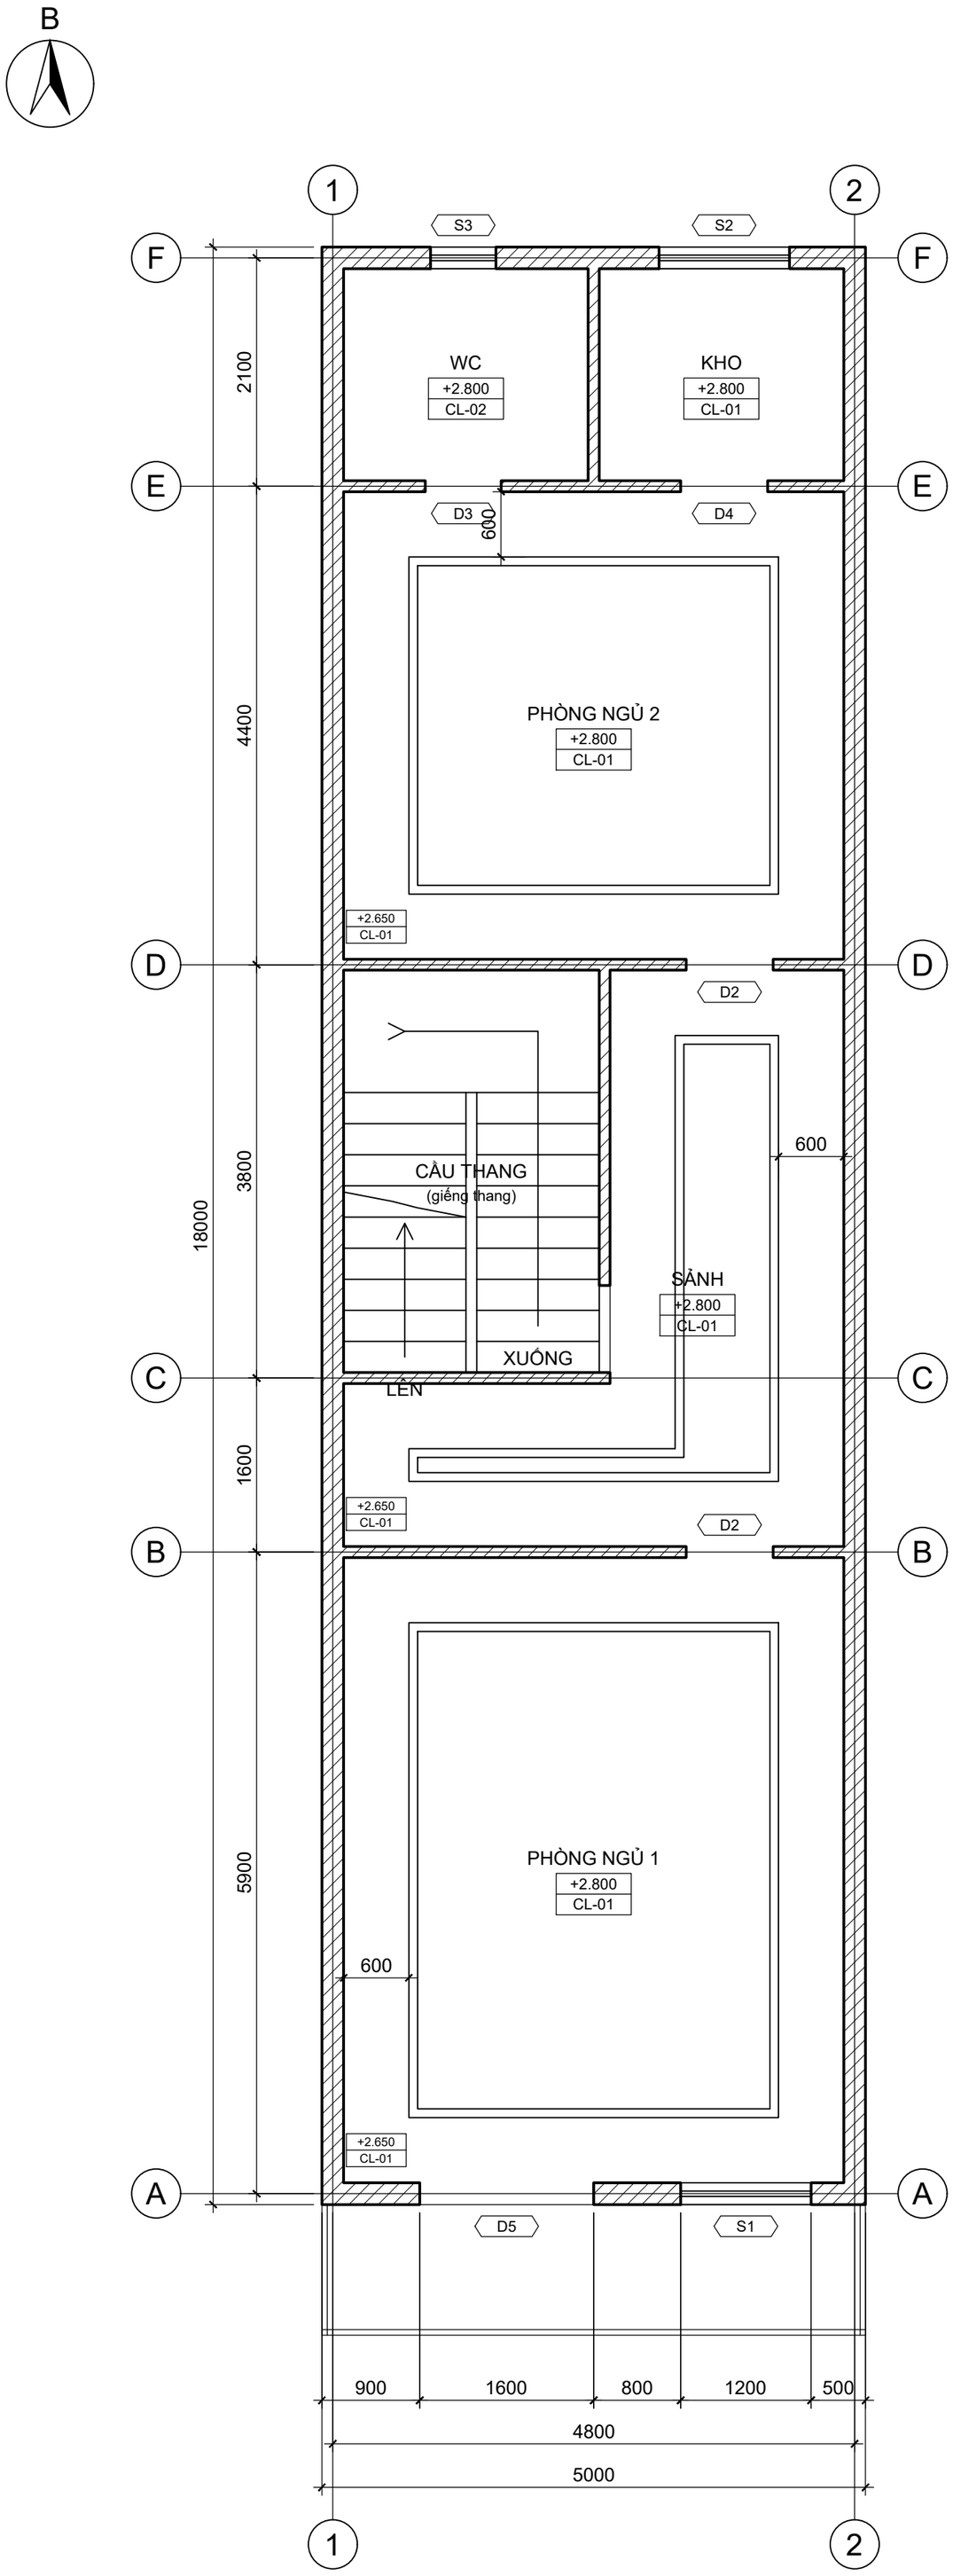

MẶT BẰNG HOÀN THIỆN TRẦN TẦNG 2

TỶ LỆ: 1/50

CHÚ THÍCH VẬT LIỆU TRẦN


CL-01 Trần thạch cao khung chìm, sơn trắng
cao độ +2.650, +2.800; 65,69 m² (PHÒNG NGỦ 1, SẢNH, PHÒNG NGỦ 2, KHO)

CL-02 Trần thạch cao chống ẩm khung chìm, sơn trắng
cao độ +2.800; 4,39 m² (WC)

GHI CHÚ:

1. Kích thước ghi bằng mm, cao độ ghi bằng m, tính từ mặt sàn hoàn thiện của tầng.
2. Nhà thầu kiểm tra kích thước thực tế tại công trình trước khi thi công, báo lại thiết kế khi có sai khác.
3. Vật liệu theo mã trong bảng thống kê vật liệu hoàn thiện; mẫu vật liệu trình chủ đầu tư và thiết kế duyệt trước khi thi công.
4. Trần thạch cao khung chìm, tấm dày 9 mm; khu ẩm ướt dùng tấm chống ẩm; bả, sơn hoàn thiện như tường.
5. Cao độ trần tính từ mặt sàn hoàn thiện; giật cấp và khe hắt đèn theo kích thước trên bản vẽ.
6. Bố trí lỗ thăm trần 600x600 tại vị trí thiết bị kỹ thuật (máy lạnh, quạt hút, van).

AUTOCAD MCP			
CÔNG TRÌNH: NHÀ PHỐ 5x18m, 3 TẦNG + TUM		CHỦ ĐẦU TƯ: CHỦ ĐẦU TƯ (MẪU)	
TÊN BẢN VẼ: MẶT BẰNG HOÀN THIỆN TRẦN TẦNG 2			
TỶ LỆ: 1:50	NGÀY: 03/11/2026	THIẾT KẾ: AutoCAD MCP	KIỂM TRA: ...
SỐ BẢN VẼ: NT-04	LẦN SỬA: 01	TỜ:	

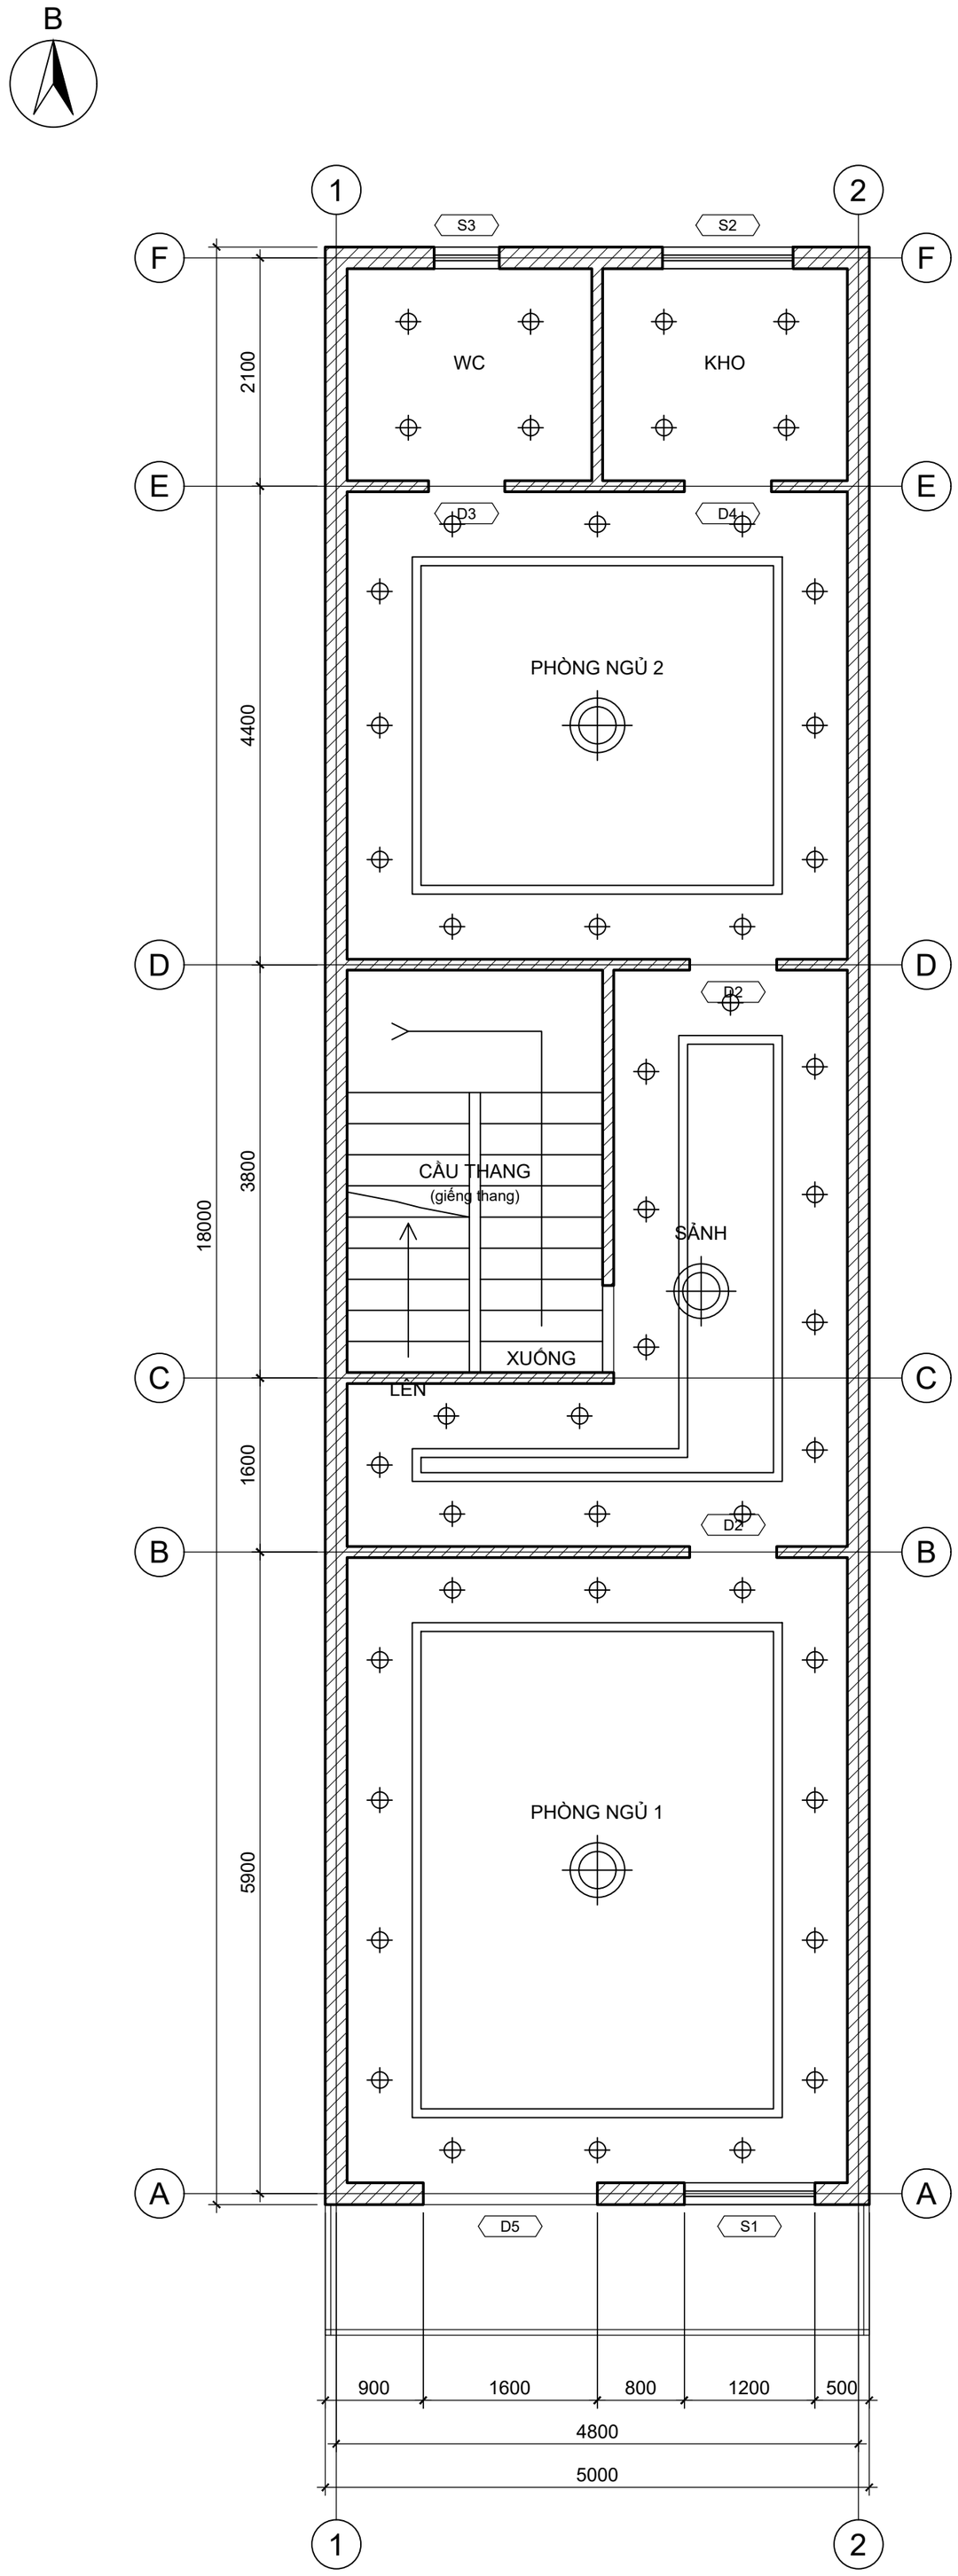

KÝ HIỆU ĐÈN

- LT-01 Đèn downlight âm trần Ø90: 48 cái
- LT-03 Đèn ốp trần: 3 cái
- LT-02 Đèn LED dây hắt trần: 42,0 m


GHI CHÚ:

1. Kích thước ghi bằng mm, cao độ ghi bằng m, tính từ mặt sàn hoàn thiện của tầng.
2. Nhà thầu kiểm tra kích thước thực tế tại công trình trước khi thi công, báo lại thiết kế khi có sai khác.
3. Vật liệu theo mã trong bảng thống kê vật liệu hoàn thiện; mẫu vật liệu trình chủ đầu tư và thiết kế duyệt trước khi thi công.
4. Vị trí đèn định vị theo tim đèn, đo từ mặt tường hoàn thiện.
5. Chủng loại, công suất, nhiệt độ màu của đèn theo bảng ký hiệu đèn và chỉ dẫn kỹ thuật.
6. Phối hợp bản vẽ điện để bố trí công tắc, ổ cắm và mạch đèn.

MẶT BẰNG BỐ TRÍ ĐÈN TẦNG 2


TỶ LỆ: 1/50

AUTOCAD MCP			
CÔNG TRÌNH: NHÀ PHỐ 5x18m, 3 TẦNG + TUM		CHỦ ĐẦU TƯ: CHỦ ĐẦU TƯ (MẪU)	
TÊN BẢN VẼ: MẶT BẰNG BỐ TRÍ ĐÈN TẦNG 2			
TỶ LỆ: 1:50	NGÀY: 03/11/2026	THIẾT KẾ: AutoCAD MCP	KIỂM TRA: ...
SỐ BẢN VẼ: NT-05	LẦN SỬA: 01	TỜ:	

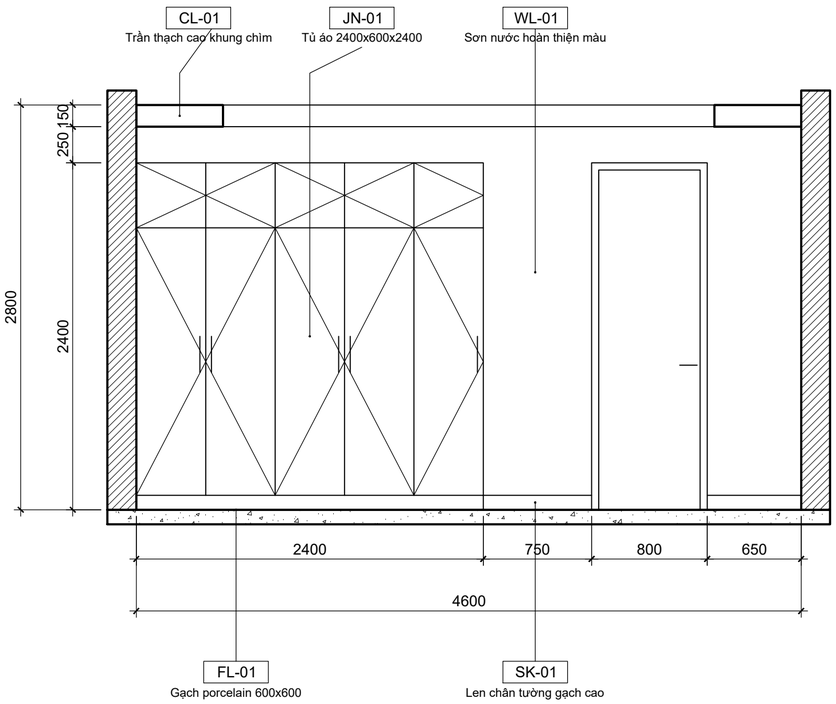

MẶT ĐỨNG A - PHÒNG NGỦ 1

TỶ LỆ: 1/30

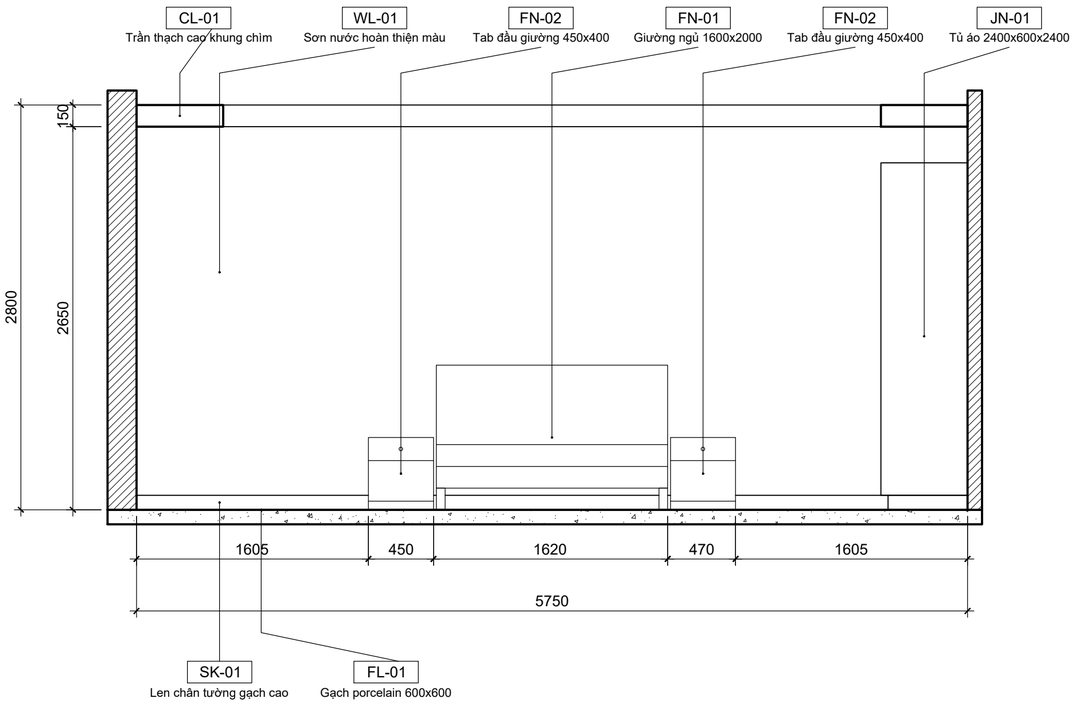

MẶT ĐỨNG D - PHÒNG NGỦ 1

TỶ LỆ: 1/30

GHI CHÚ: NHÀ THẦU THI CÔNG KIỂM TRA KÍCH THƯỚC THỰC TẾ, NẾU THẤY CÓ XUNG ĐỘT CẦN BÁO LẠI CHO THIẾT KẾ VÀ QUẢN LÝ KỸ THUẬT.

LẦN NỘP	NỘI DUNG ĐIỀU CHỈNH	NGÀY NỘP
1		
2		
3		
4		

GHI CHÚ - Note:

CHỦ ĐẦU TƯ - Client:

CHỦ ĐẦU TƯ (MẪU)

DỰ ÁN - Project:

NHÀ PHỐ 5x18m, 3 TẦNG + TUM

Mẫu minh họa

HẠNG MỤC - Item:

KIẾN TRÚC, NỘI THẤT

TƯ VẤN THIẾT KẾ - Consultant:

AUTOCAD MCP




CHỦ NHIỆM TK - Chief of Project	
CHỦ TRÌ TK - Chief of Division	
THIẾT KẾ - Designed by AutoCAD MCP	
KIỂM TRA - Checked by ...	

TÊN BẢN VẼ - Drawing name:

MẶT ĐỨNG NỘI THẤT PHÒNG NGỦ 1 TẦNG 2

SỐ HĐ - Contract No:	PHIÊN BẢN - Version 01
GIAI ĐOẠN - Phase: TKTC	KÝ HIỆU BẢN VẼ - Drawing No NT-06
TỶ LỆ - Scale: 1:30	HOÀN THÀNH - Finish: 03/11/2026

BẢNG THỐNG KÊ VẬT LIỆU HOÀN THIỆN

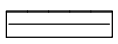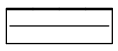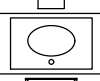MÃ	KÝ HIỆU	HẠNG MỤC	MÔ TẢ	VỊ TRÍ	ĐV	KHỐI LƯỢNG
CL-01		Trần	Trần thạch cao khung chìm, sơn trắng	TẦNG 1: PHÒNG KHÁCH, BẾP + ĂN; TẦNG 2: PHÒNG NGỦ 1, SẢNH, PHÒNG NGỦ 2, KHO; TẦNG 3: PHÒNG NGỦ 3, SẢNH, PHÒNG THỜ	m²	188,75
CL-02		Trần	Trần thạch cao chống ẩm khung chìm, sơn trắng	TẦNG 1: WC; TẦNG 2: WC; TẦNG 3: WC	m²	13,16
FL-01		Sàn	Gạch porcelain 600x600	TẦNG 1: PHÒNG KHÁCH, BẾP + ĂN; TẦNG 2: PHÒNG NGỦ 1, SẢNH, PHÒNG NGỦ 2, KHO; TẦNG 3: PHÒNG NGỦ 3, SẢNH, PHÒNG THỜ	m²	188,75
FL-02		Sàn	Gạch chống trơn 300x300	TẦNG 1: WC; TẦNG 2: WC; TẦNG 3: WC	m²	13,16
FL-03		Sàn	Gạch chống trơn ngoài trời 400x400	TẦNG 1: SÂN PHƠI; TẦNG 3: SÂN PHƠI; TUM: SÂN THƯỢNG	m²	79,74
FL-04		Sàn	Đá granite ốp bậc thang và chiếu nghỉ	TẦNG 1: CẦU THANG; TẦNG 2: CẦU THANG; TẦNG 3: CẦU THANG; TUM: CẦU THANG	m²	34,37
FN-01		Nội thất rời	Giường ngủ 1600x2000	TẦNG 2: PHÒNG NGỦ 1, PHÒNG NGỦ 2	cái	2
FN-02		Nội thất rời	Tab đầu giường 450x400	TẦNG 2: PHÒNG NGỦ 1, PHÒNG NGỦ 2	cái	4
FN-08		Nội thất rời	Bàn làm việc 1200x500	TẦNG 2: PHÒNG NGỦ 1	cái	1
JN-01		Đồ gỗ đóng tại chỗ	Tủ áo 2400x600x2400	TẦNG 2: PHÒNG NGỦ 1	cái	1
JN-07		Đồ gỗ đóng tại chỗ	Tủ áo 1800x600x2400	TẦNG 2: PHÒNG NGỦ 2	cái	1
LT-01		Đèn	Đèn downlight âm trần Ø90	TẦNG 2	cái	48
LT-02		Đèn	Đèn LED dây hắt trần	TẦNG 2	m	41,98
LT-03		Đèn	Đèn ốp trần	TẦNG 2	cái	3
SK-01		Len chân tường	Len chân tường gạch cao 100	TẦNG 1: PHÒNG KHÁCH, BẾP + ĂN, SÂN PHƠI; TẦNG 2: PHÒNG NGỦ 1, SẢNH, PHÒNG NGỦ 2, KHO; TẦNG 3: PHÒNG NGỦ 3, SẢNH, PHÒNG THỜ, SÂN PHƠI; TUM: SÂN THƯỢNG	m	216
SK-02		Len chân tường	Len đá granite cao 100 theo bậc	TẦNG 1: CẦU THANG; TẦNG 2: CẦU THANG; TẦNG 3: CẦU THANG; TUM: CẦU THANG	m	44,95
SN-01		Thiết bị vệ sinh	Bồn cầu 400x700	TẦNG 2: WC	cái	1
SN-02		Thiết bị vệ sinh	Lavabo, tủ chậu, gương 800x500	TẦNG 2: WC	cái	1
SN-03		Thiết bị vệ sinh	Khu tắm đứng, vách kính 900x900	TẦNG 2: WC	cái	1
WL-01		Tường hoàn thiện	Sơn nước hoàn thiện màu trắng	TẦNG 1: PHÒNG KHÁCH, CẦU THANG, BẾP + ĂN; TẦNG 2: PHÒNG NGỦ 1, SẢNH, CẦU THANG, PHÒNG NGỦ 2, KHO; TẦNG 3: PHÒNG NGỦ 3, SẢNH, CẦU THANG, PHÒNG THỜ; TUM: CẦU THANG	m²	560,42
WL-02		Tường hoàn thiện	Gạch ốp tường 300x600 ốp đến trần	TẦNG 1: WC; TẦNG 2: WC; TẦNG 3: WC	m²	65,94
WL-04		Tường hoàn thiện	Sơn ngoại thất màu trắng	TẦNG 1: SÂN PHƠI; TẦNG 3: SÂN PHƠI; TUM: SÂN THƯỢNG	m²	188,72

AUTOCAD MCP

CÔNG TRÌNH	CHỦ ĐẦU TƯ
NHÀ PHỐ 5x18m, 3 TẦNG + TUM	CHỦ ĐẦU TƯ (MẪU)

TÊN BẢN VẼ

BẢNG THỐNG KÊ VẬT LIỆU HOÀN THIỆN

TỶ LỆ	NGÀY	THIẾT KẾ	KIỂM TRA
1:50	03/11/2026	AutoCAD MCP	...

SỐ BẢN VẼ	LẦN SỬA	TỜ
NT-07	01	